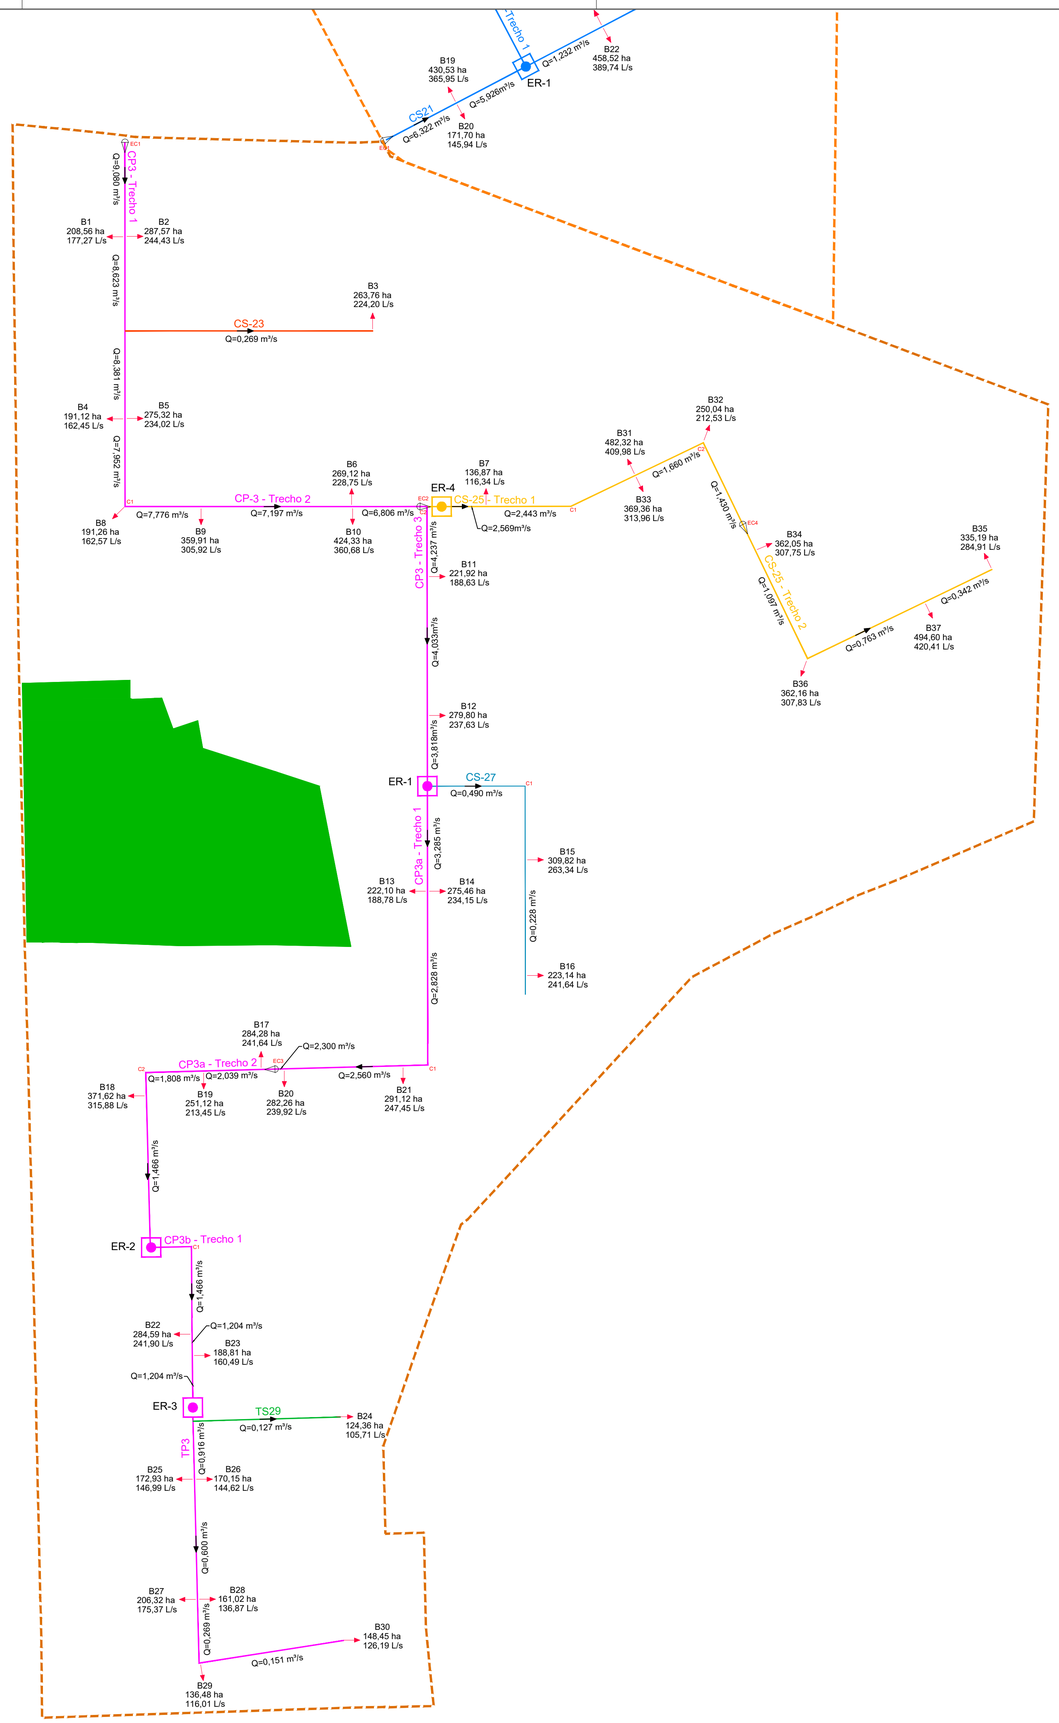


LEGENDA:

- LIMITE - JAÍBA IV
- CANAL ADUTOR - CP-3
- CANAL ADUTOR - CS-23
- CANAL ADUTOR - CS-25
- CANAL ADUTOR - CS-27
- CANAL ADUTOR - CS-29
- ÁREAS AMBIENTAIS SENSÍVEIS
- TOMADA D'ÁGUA
- ELEVATÓRIA DE RECALQUE (ER)
- SENTIDO DE ESCOAMENTO

NOTAS:

1 - VAZÃO NA PARCELA EM L/S

2 - VAZÃO NO CANAL EM M³/S

Revisão	Data	Descrição	Elab.	Verif.	Aprov.	Aut.
2	25/11/2025	Revisão da vazão unitária parcelar	AHL	HKZ	EDK	
1	13/10/2025	Revisão do parcelamento das áreas irrigáveis	AHL	HKZ	EDK	
0	29/08/2025	Emissão Inicial	AHL	HKO	EDK	

FUNDO DE DESENVOLVIMENTO DA INFRAESTRUTURA REGIONAL SUSTENTÁVEL - FDIRS

ESTRUTURAÇÃO DE PROJETO DE CONCESSÃO DO PERÍMETRO IRRIGADO DO JAÍBA (ETAPAS 3 E 4)

ANTEPROJETO

DIAGRAMA DE VAZÕES

ETAPA 4

Finalidade de Emissão	1 Para Informação	2 Para Comentários	Para Aprovação	4 Para Execução	5 Como Construído	6 Para Utilização	7 Para Providências

Moysés & Pires Projetos de Engenharia | ENGECORPS Grupo OAS | Plena Consultoria e Projetos

Data: 29/08/25	Elaboração:	Verificação:	
Escala: sem escala	Aprovação	Autorização	
Referência:	Revisão: 02	Desenho nº J4-DS-HI-0002	