

E=632500 E=635000 E=637500 E=640000 E=642500 E=645000

N=8340000 N=8337500 N=8335000 N=8332500 N=8330000 N=8327500


N=8340000 N=8337500 N=8335000 N=8332500 N=8330000 N=8327500

ARTICULAÇÃO:

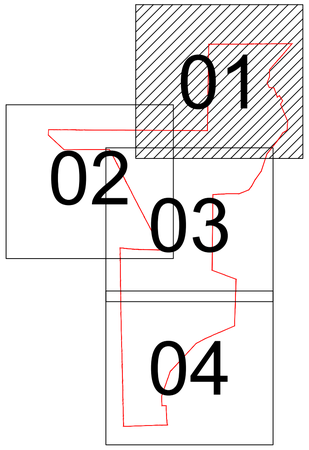

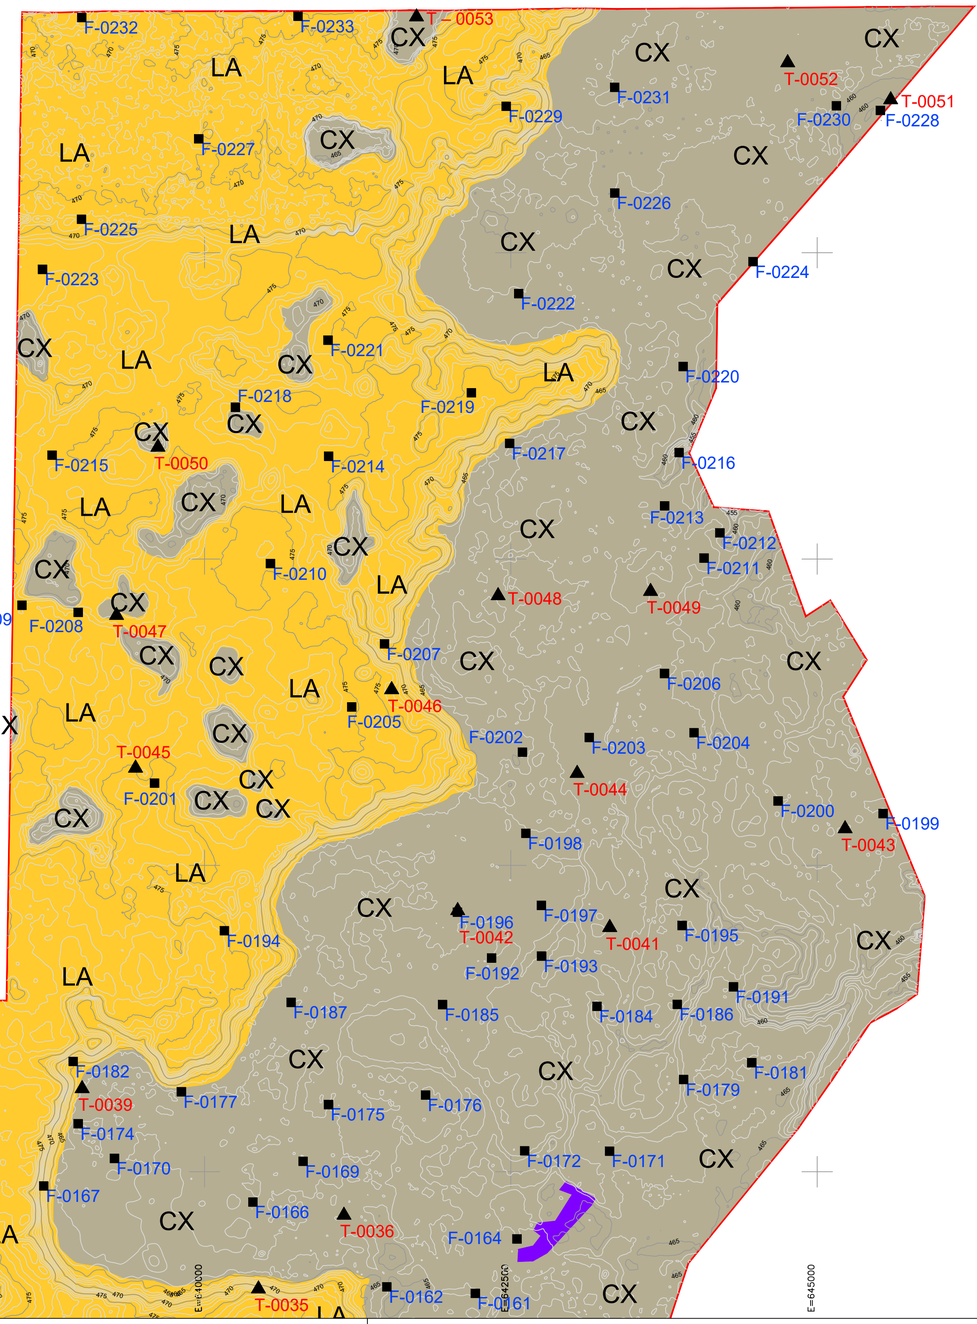

MAPA DE LOCALIZAÇÃO

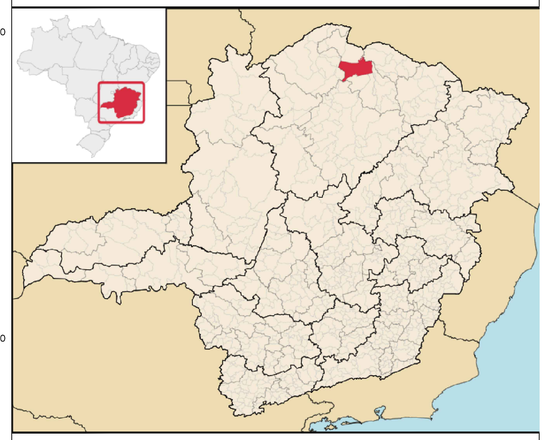

NOTAS:

1 - MEDIDAS, COORDENADAS E ELEVAÇÕES EM METRO.
2 - DATUM HORIZONTAL SIRGAS2000 - FUSO 23 - MC 45º WGr.
3 - DATUM VERTICAL: MODELO GEOIDE HGEOHNOR2020 – MARÉGRAFO IMBITUBA - SC

LEGENDA:

- PERÍMETRO DO PROJETO DE IRRIGAÇÃO JAÍBA (ETAPAS III E IV)
- CURVAS DE NÍVEL (415 / 410)
- TRINCHEIRA
- TRADAGEM

NOMENCLATURA:

- TRINCHEIRA — NÚMERO TRINCHEIRA (ex: T-001)
- TRADAGEM — NÚMERO TRADAGEM (ex: F-001)

CLASSIFICAÇÃO DE SOLOS	ÁREA (ha)	%
LATOSSOLOS AMARELOS - LA	14.982,79	50,517
CAMBISSOLOS HÁPLICOS - CX	10.209,25	34,422
LATOSSOLOS VERMELHOS - LV	3.479,30	11,731
LATOSSOLOS VERMELHO-AMARELOS - LVA	748,45	2,524
PLANOSSOLOS HÁPLICOS - SX	59,99	0,202
NEOSSOLOS FLÚVICO - RY	18,10	0,061
AFLORAMENTO ROCHOSO - AR	38,37	0,129
POVOADO	30,69	0,103
FAIXA DE DOMÍNIO RODOVIA	79,33	0,267
CANAL DE ADUÇÃO	12,14	0,041
POSTO DE GASOLINA	0,54	0,002
COPASA	0,23	0,001
TOTAL	29.659,18	100,000

Revisão	Data	Descrição	Elab.	Verif.	Aprov.	Aut.
0	XX/XX	Emissão Inicial	XXX	XXX	XXX	XXX

FUNDO DE DESENVOLVIMENTO DA INFRAESTRUTURA REGIONAL SUSTENTÁVEL - FDIRS

ESTRUTURAÇÃO DE PROJETO DE CONCESSÃO DO PERÍMETRO IRRIGADO DO JAÍBA (ETAPAS III E IV)

ANTEPROJETO

ESTUDOS PEDOLÓGICOS
MAPA DE SOLOS
COM CURVA DE NÍVEL

Finalidade de Emissão	1 Para Informação	2 Para Comentários	3 Para Aprovação	4 Para Execução	5 Como Construído	6 Para Utilização	7 Para Providências

Data: 01/09/25	Elaboração:	Verificação:	
Escala: 1:25.000	Aprovação: XXX / XXX	Autorização: XXX / XXX	
Referência:	Revisão: RV00	Desenho nº: JB_E3-4.07.PDL.DE.003	