
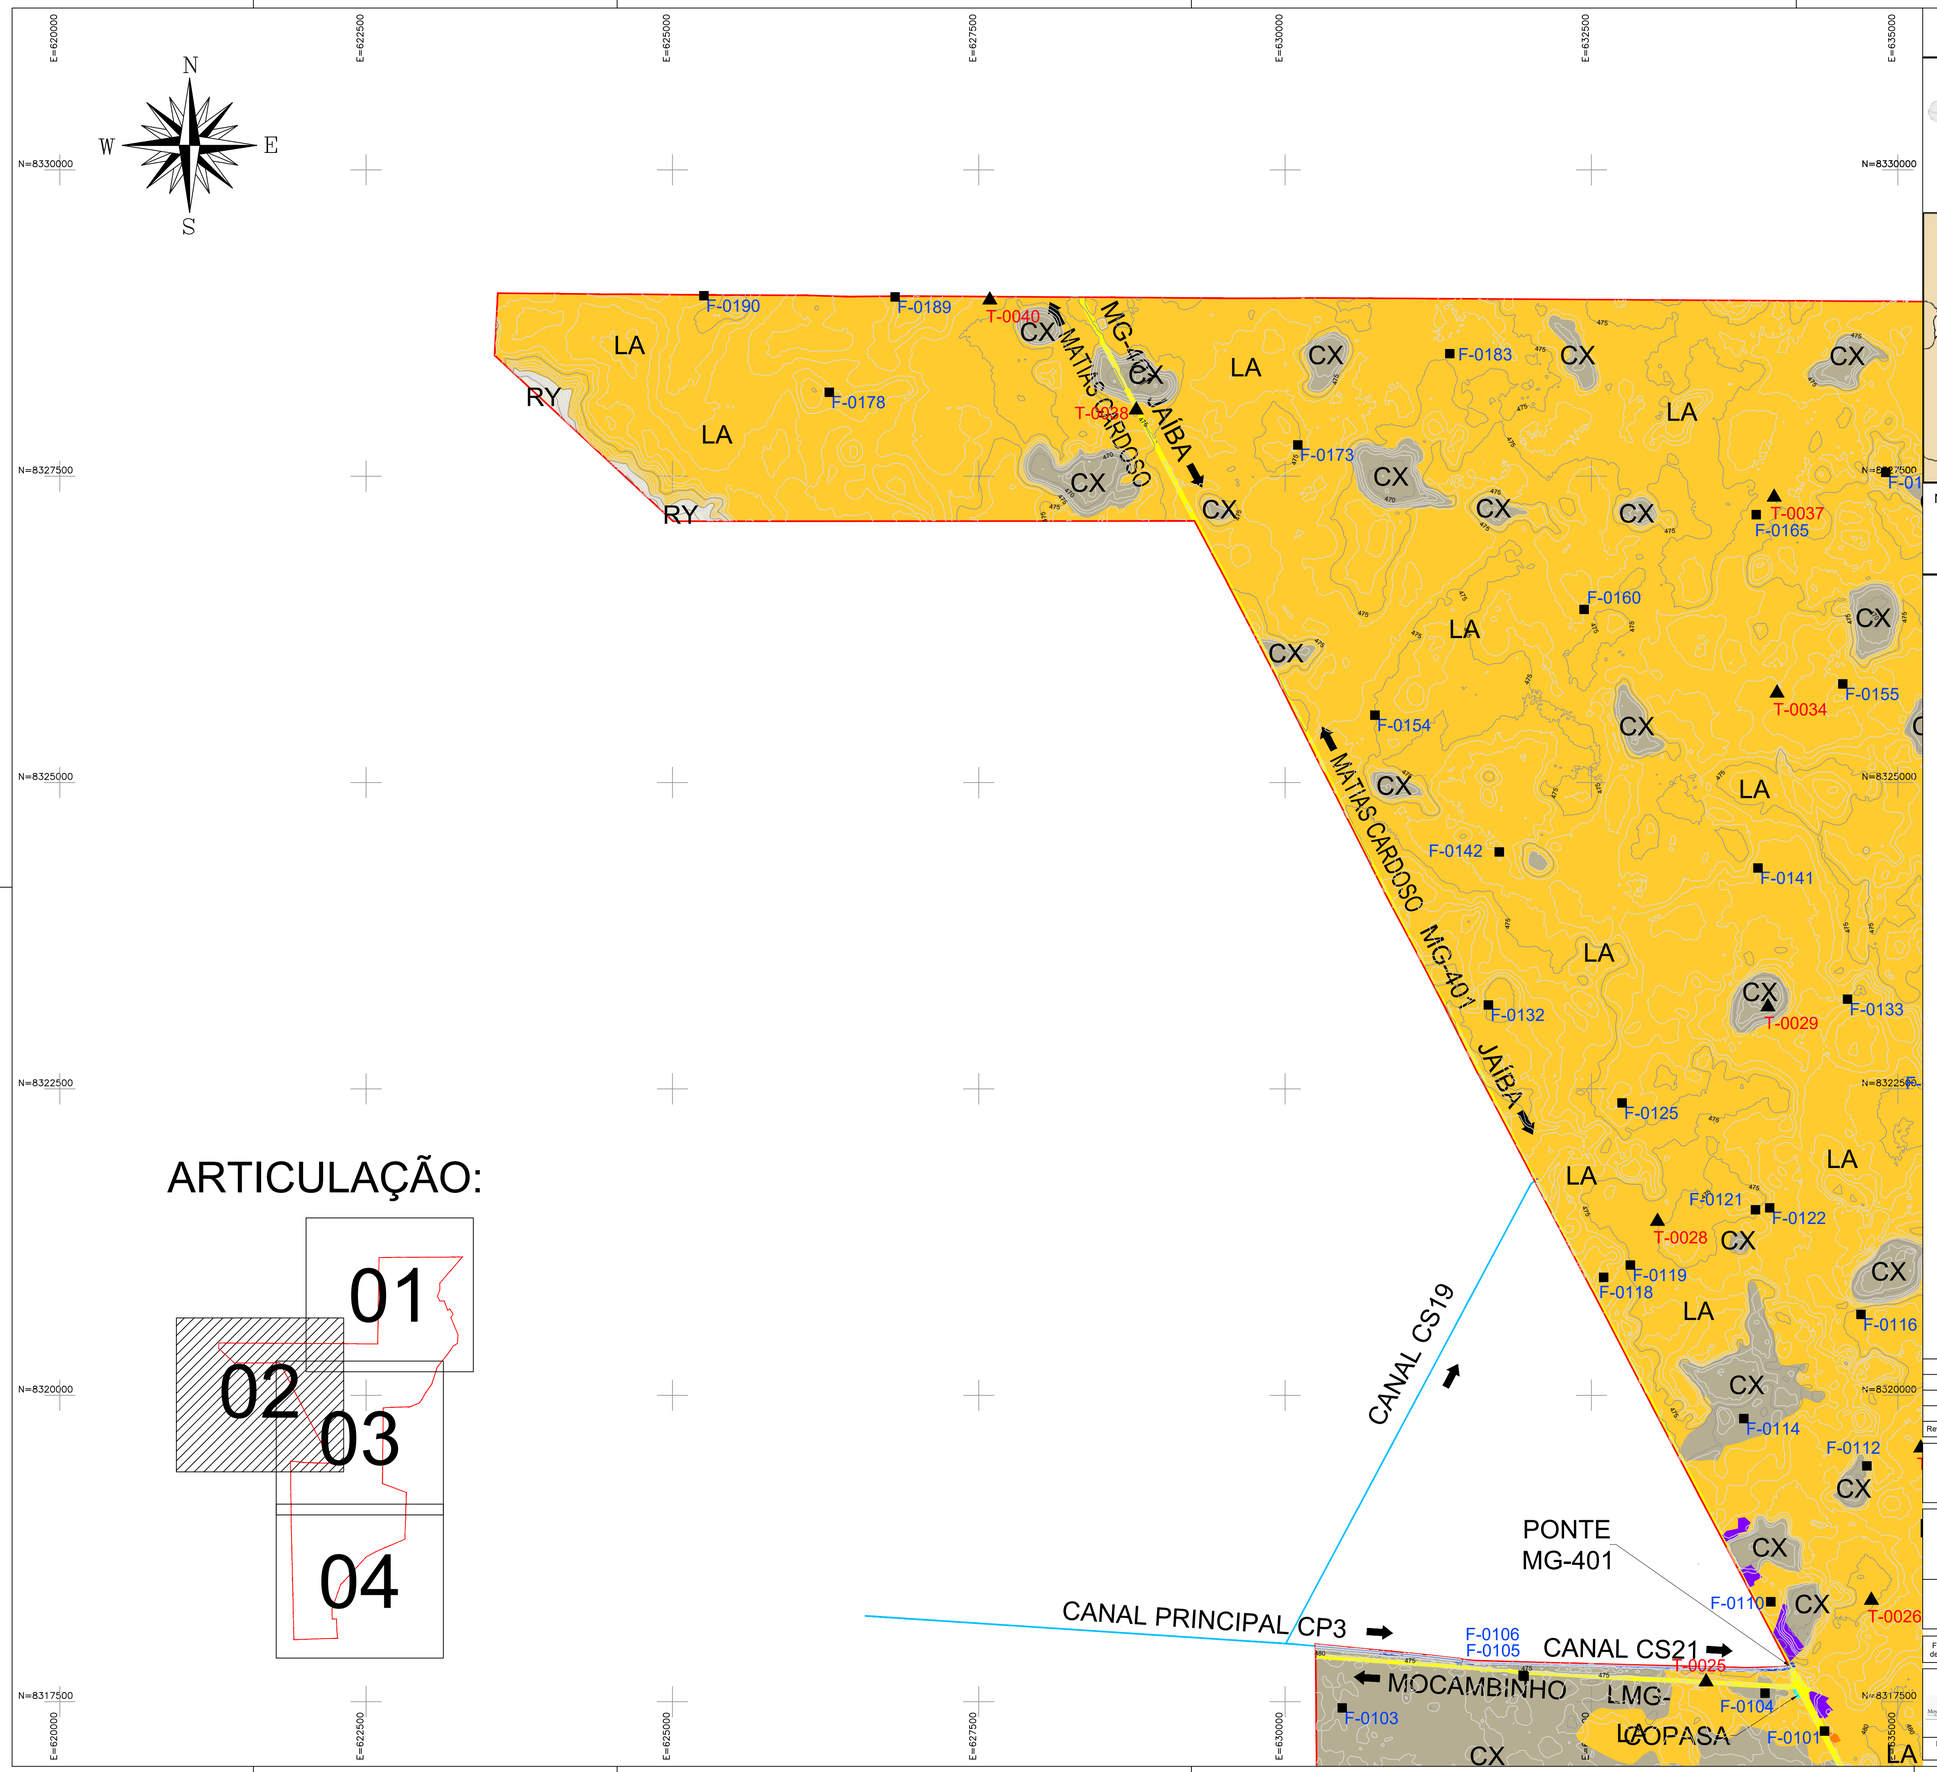


MAPA DE LOCALIZAÇÃO

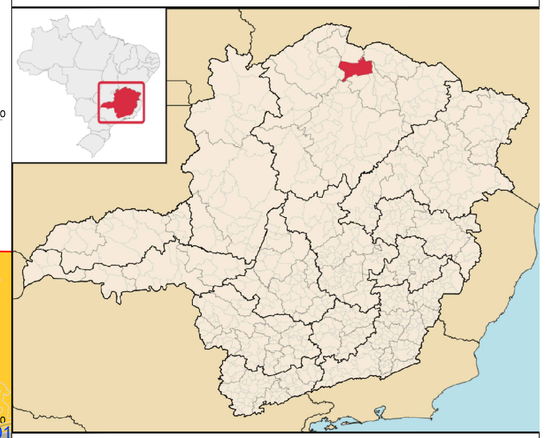

NOTAS:

1 - MEDIDAS, COORDENADAS E ELEVAÇÕES EM METRO.
2 - DATUM HORIZONTAL SIRGAS2000 - FUSO 23 - MC 45º WGr.
3 - DATUM VERTICAL: MODELO GEOIDE HGEOHNOR2020 – MARÉGRAFO IMBITUBA - SC

LEGENDA:

- PERÍMETRO DO PROJETO DE IRRIGAÇÃO JAÍBA (ETAPAS III E IV)
- CURVAS DE NÍVEL (415 / 410)
- TRINCHEIRA
- TRADAGEM

NOMENCLATURA:

- TRINCHEIRA — NÚMERO TRINCHEIRA (ex. T-001)
- TRADAGEM — NÚMERO TRADAGEM (ex. F-001)

CLASSIFICAÇÃO DE SOLOS	ÁREA (ha)	%
LATOSSOLOS AMARELOS - LA	14.982,79	50,517
CAMBISSOLOS HÁPLICOS - CX	10.209,25	34,422
LATOSSOLOS VERMELHOS - LV	3.479,30	11,731
LATOSSOLOS VERMELHO-AMARELOS - LVA	748,45	2,524
PLANOSSOLOS HÁPLICOS - SX	59,99	0,202
NEOSSOLOS FLÚVICO - RY	18,10	0,061
AFLORAMENTO ROCHOSO - AR	38,37	0,129
POVOADO	30,69	0,103
FAIXA DE DOMÍNIO RODOVIA	79,33	0,267
CANAL DE ADUÇÃO	12,14	0,041
POSTO DE GASOLINA	0,54	0,002
COPASA	0,23	0,001
TOTAL	29.659,18	100,000

ARTICULAÇÃO:

Revisão	Data		Elab.	Verif.	Aprov.	Aut.
0	XX/XX	Emissão Inicial	XXX	XXX	XXX	XXX

FUNDO DE DESENVOLVIMENTO DA INFRAESTRUTURA REGIONAL SUSTENTÁVEL - FDIRS

ESTRUTURAÇÃO DE PROJETO DE CONCESSÃO DO PERÍMETRO IRRIGADO DO JAÍBA (ETAPAS III E IV)

ANTEPROJETO

ESTUDOS PEDOLÓGICOS
MAPA DE SOLOS
COM CURVA DE NÍVEL

Finalidade de Emissão	1 Para Informação	2 Para Comentários	3 Para Aprovação	4 Para Execução	5 Como Construído	6 Para Utilização	7 Para Providências

Data: 01/09/25	Elaboração:	Verificação:	
Escala: 1:25.000	Aprovação XXX / XXX	Autorização	XXX / XXX
Referência:	Revisão: RV00	Desenho nº JB_E3-4.07.PDL.DE.003	