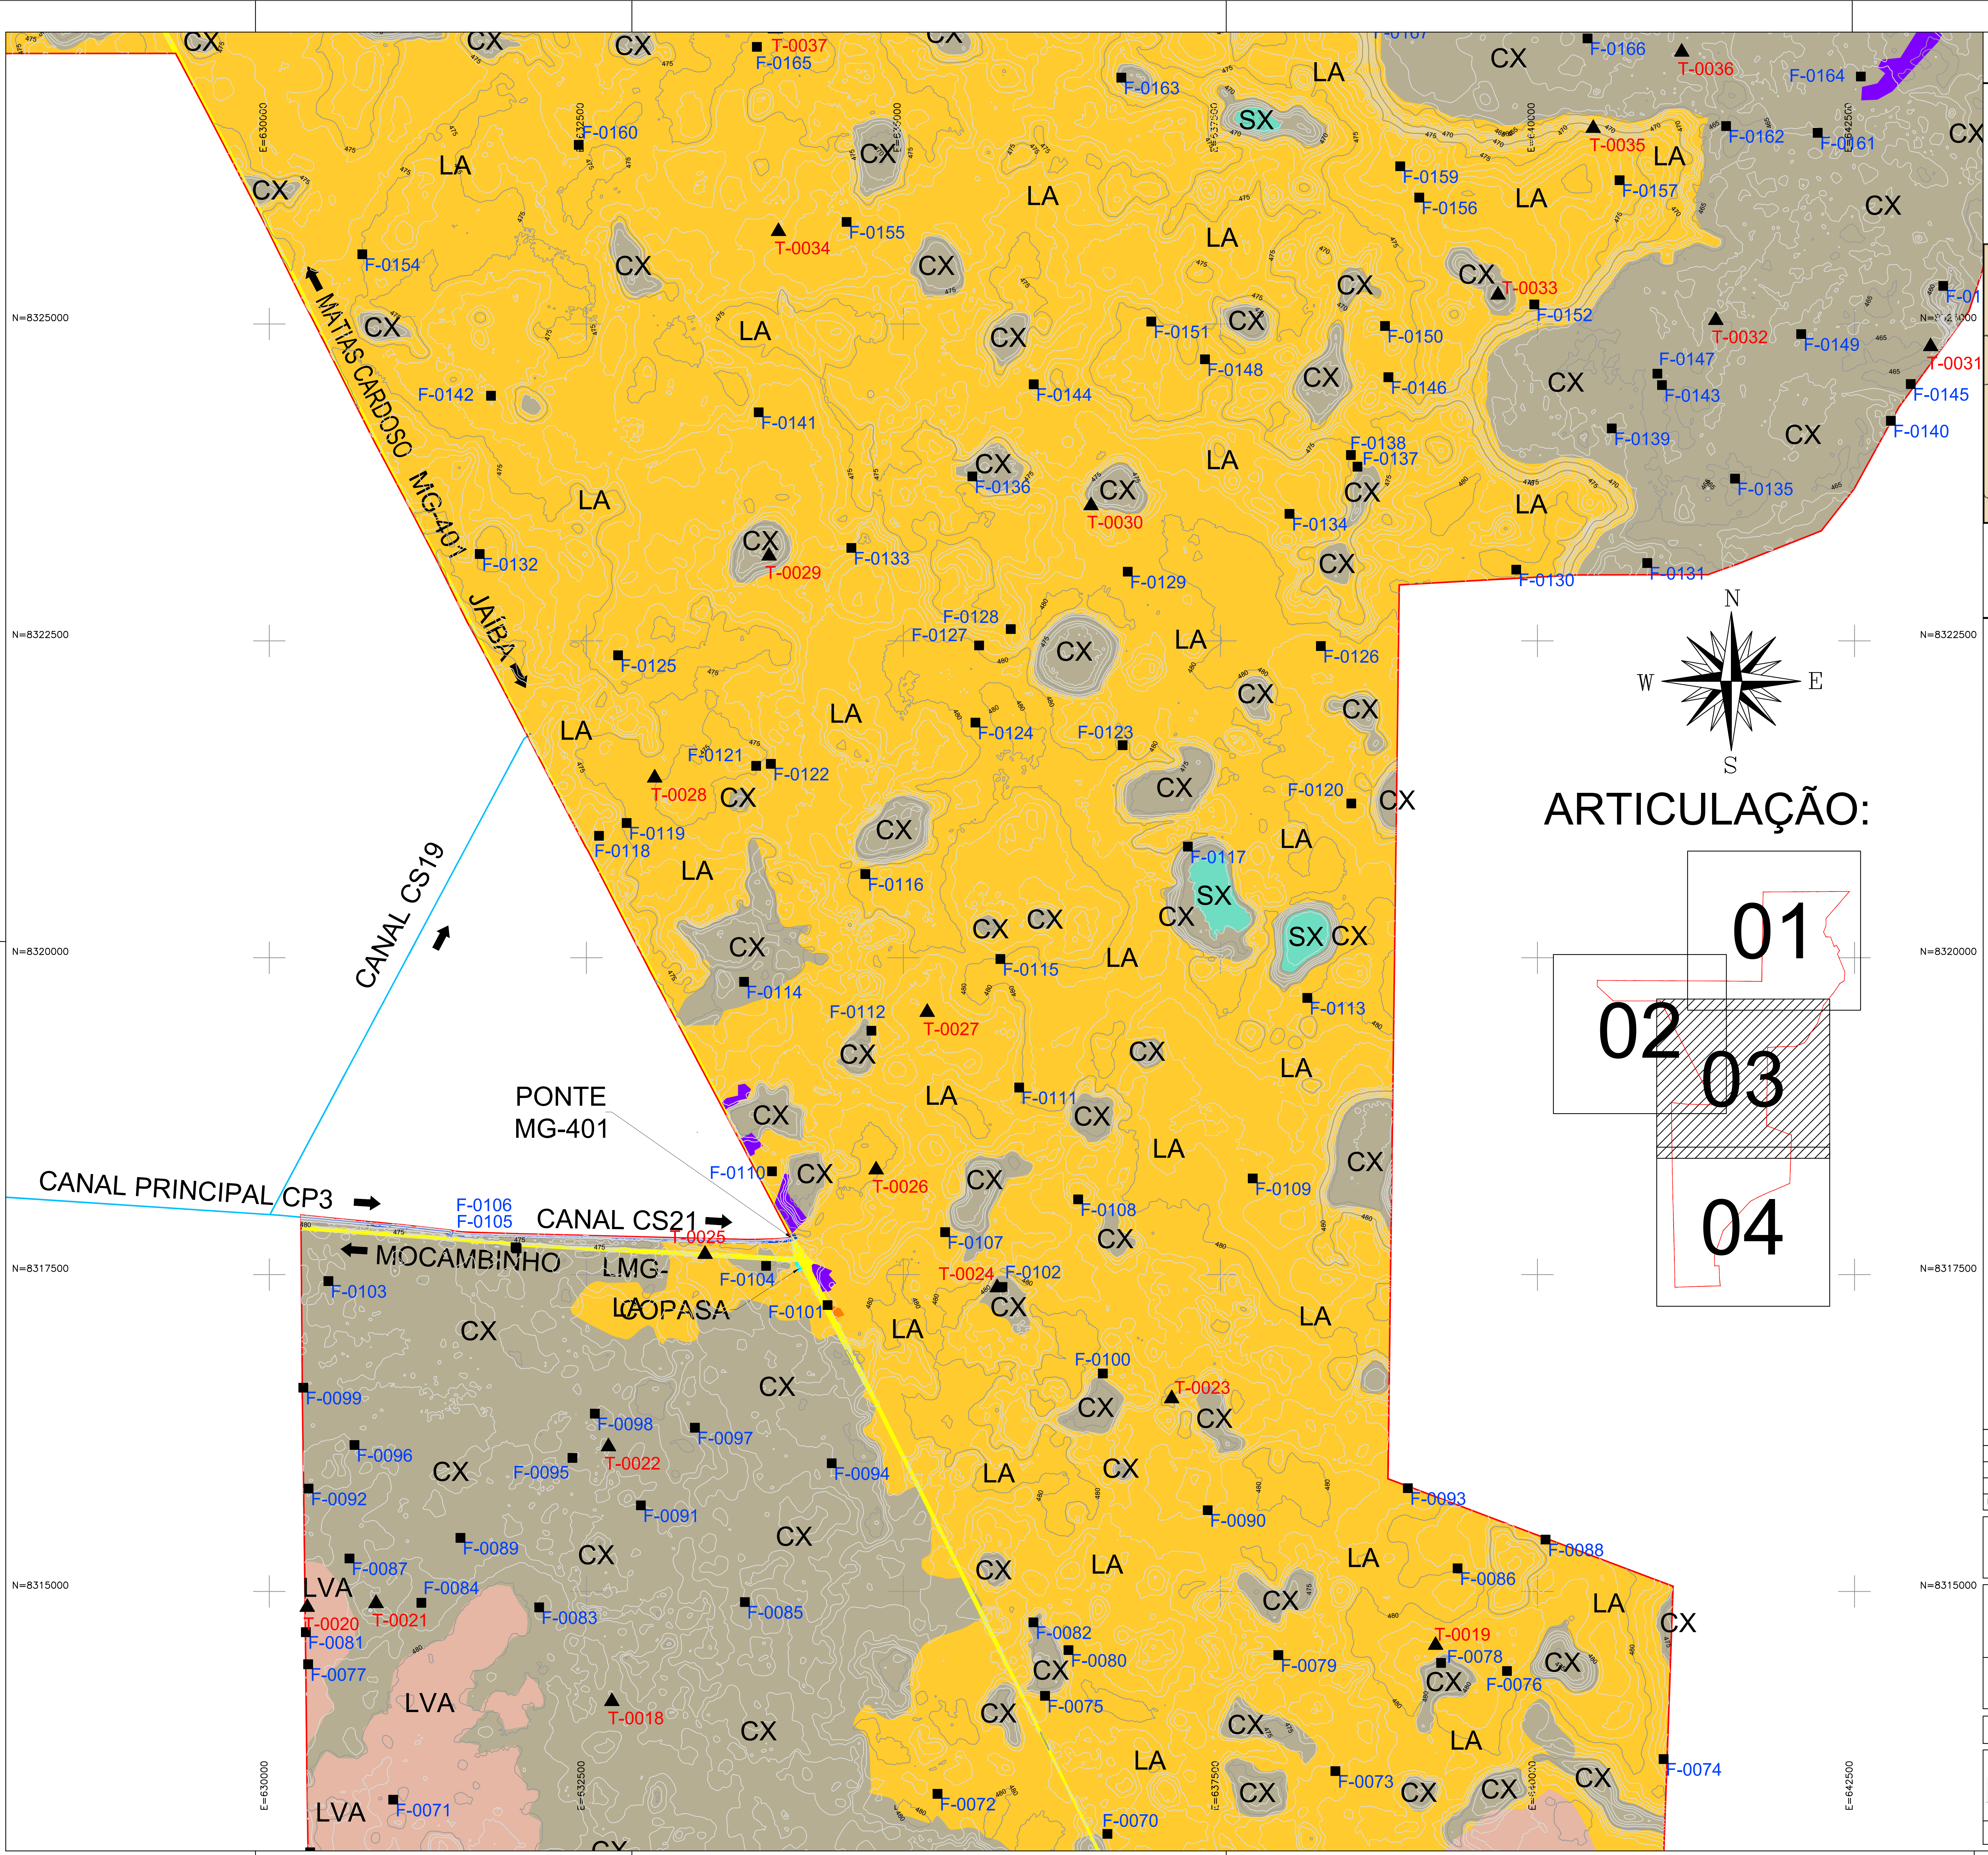
N=8325000
N=8322500
N=8320000
N=8317500
N=8315000
E=630000
E=632500
E=635000
E=637500
E=640000
E=642500
LA
CX
SX
LV
LVA
MATIAS CARDOSO
MG-401
JAÍBA
CANAL CS19
CANAL PRINCIPAL CP3
CANAL CS21
PONTE
MG-401
MOCAMBINHO
LMG-
COPASA
T-0037
T-0036
T-0035
T-0034
T-0033
T-0032
T-0031
T-0030
T-0029
T-0028
T-0027
T-0026
T-0025
T-0024
T-0023
T-0022
T-0021
T-0020
T-0019
T-0018
F-0166
F-0165
F-0164
F-0163
F-0162
F-0161
F-0160
F-0159
F-0157
F-0156
F-0155
F-0154
F-0152
F-0151
F-0150
F-0149
F-0148
F-0147
F-0146
F-0145
F-0144
F-0143
F-0142
F-0141
F-0140
F-0139
F-0138
F-0137
F-0136
F-0135
F-0134
F-0133
F-0132
F-0131
F-0130
F-0129
F-0128
F-0127
F-0126
F-0125
F-0124
F-0123
F-0122
F-0121
F-0120
F-0119
F-0118
F-0117
F-0116
F-0115
F-0114
F-0113
F-0112
F-0111
F-0110
F-0109
F-0108
F-0107
F-0106
F-0105
F-0104
F-0103
F-0102
F-0101
F-0100
F-0099
F-0098
F-0097
F-0096
F-0095
F-0094
F-0093
F-0092
F-0091
F-0090
F-0089
F-0088
F-0087
F-0086
F-0085
F-0084
F-0083
F-0082
F-0081
F-0080
F-0079
F-0078
F-0077
F-0076
F-0075
F-0074
F-0073
F-0072
F-0071
F-0070
N
S
E
W
01
02
03
04

ARTICULAÇÃO:

MAPA DE LOCALIZAÇÃO

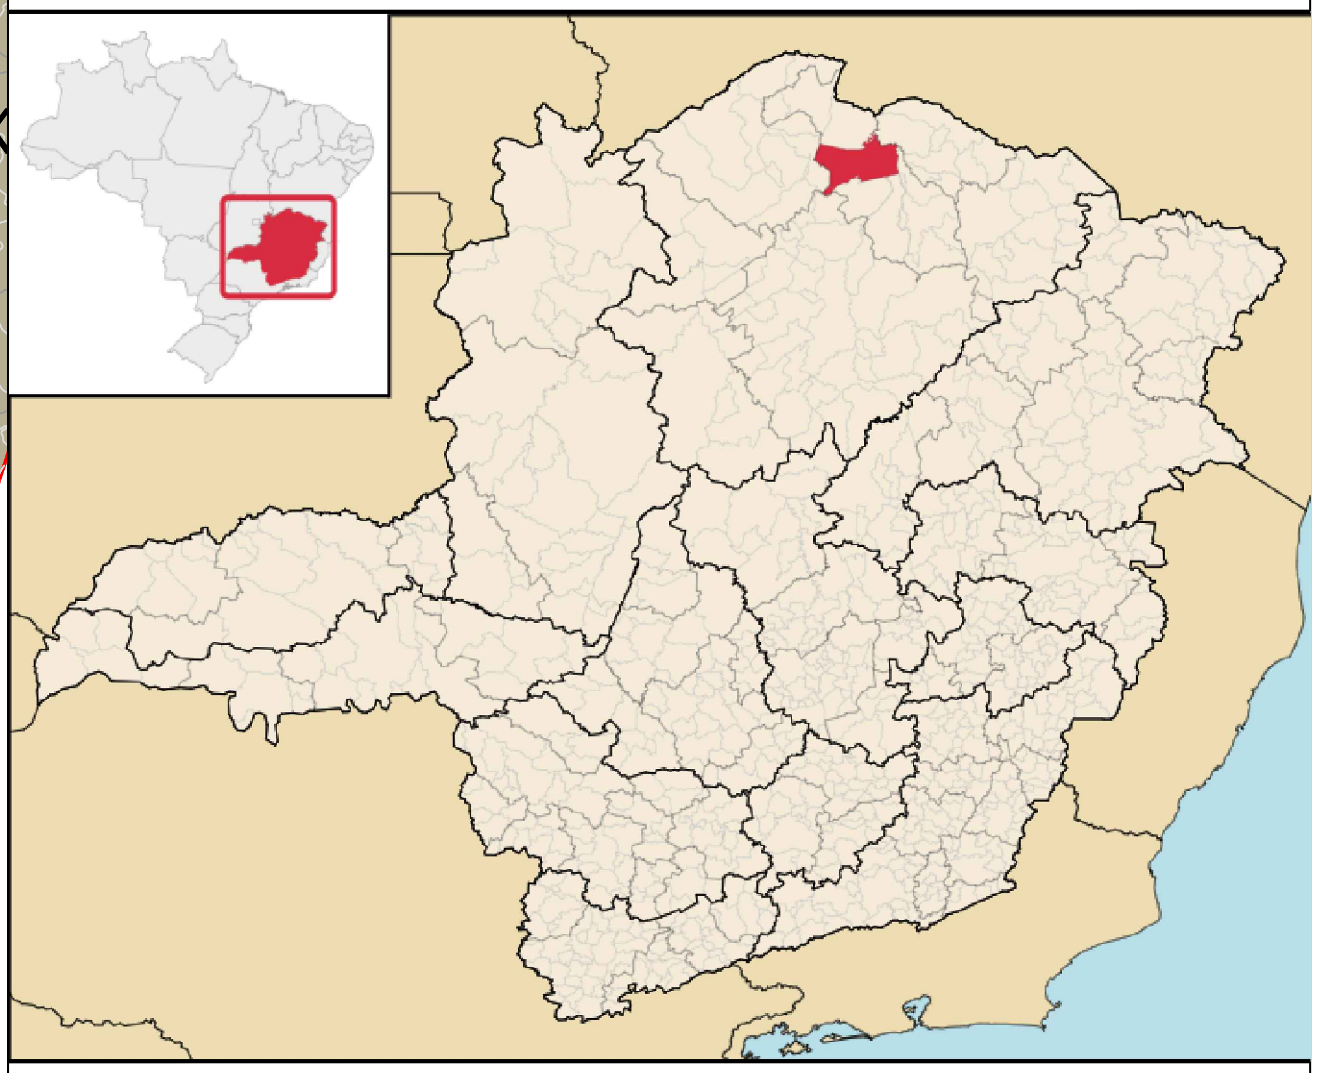

NOTAS:

1 - MEDIDAS, COORDENADAS E ELEVAÇÕES EM METRO.
2 - DATUM HORIZONTAL SIRGAS2000 - FUSO 23 - MC 45º WGr.
3 - DATUM VERTICAL: MODELO GEOIDE HGEOHNOR2020 – MARÉGRAFO IMBITUBA - SC

LEGENDA:

- PERÍMETRO DO PROJETO DE IRRIGAÇÃO JAÍBA (ETAPAS III E IV)
- 415 410 CURVAS DE NÍVEL
- ▲ TRINCHEIRA
- ■ TRADAGEM

NOMENCLATURA:

T-001 — TRINCHEIRA / NÚMERO TRINCHEIRA

F-001 — TRADAGEM / NÚMERO TRADAGEM

CLASSIFICAÇÃO DE SOLOS		ÁREA (ha)	%
🟨	LATOSSOLOS AMARELOS - LA	14.982,79	50,517
▨	CAMBISSOLOS HÁPLICOS - CX	10.209,25	34,422
🟧	LATOSSOLOS VERMELHOS - LV	3.479,30	11,731
▨	LATOSSOLOS VERMELHO-AMARELOS - LVA	748,45	2,524
🟩	PLANOSSOLOS HÁPLICOS - SX	59,99	0,202
⬜	NEOSSOLOS FLÚVICO - RY	18,10	0,061
⬛	AFLORAMENTO ROCHOSO - AR	38,37	0,129
🟪	POVOADO	30,69	0,103
🟨	FAIXA DE DOMÍNIO RODOVIA	79,33	0,267
🟦	CANAL DE ADUÇÃO	12,14	0,041
🟧	POSTO DE GASOLINA	0,54	0,002
🟦	COPASA	0,23	0,001
TOTAL		29.659,18	100,000

Revisão	Data	Descrição	Elab.	Verif.	Aprov.	Aut.
0	XX/XX	Emissão Inicial	XXX	XXX	XXX	XXX

FUNDO DE DESENVOLVIMENTO DA INFRAESTRUTURA
REGIONAL SUSTENTÁVEL - FDIRS

ESTRUTURAÇÃO DE PROJETO DE CONCESSÃO DO PERÍMETRO IRRIGADO DO JAÍBA (ETAPAS III E IV)

ANTEPROJETO

ESTUDOS PEDOLÓGICOS
MAPA DE SOLOS
COM CURVA DE NÍVEL

Finalidade de Emissão	1 Para Informação	2 Para Comentários	3 Para Aprovação	4 Para Execução	5 Como Construído	6 Para Utilização	7 Para Providências

Moysés & Pires ENGECORPS A&M Plena

Data: 01/09/25
Escala: 1:25.000
Elaboração:
Aprovação XXX XXX
Verificação:
Autorização XXX XXX
Referência:
Revisão: RV00
Desenho nº JB_E3-4.07.PDL.DE.003