



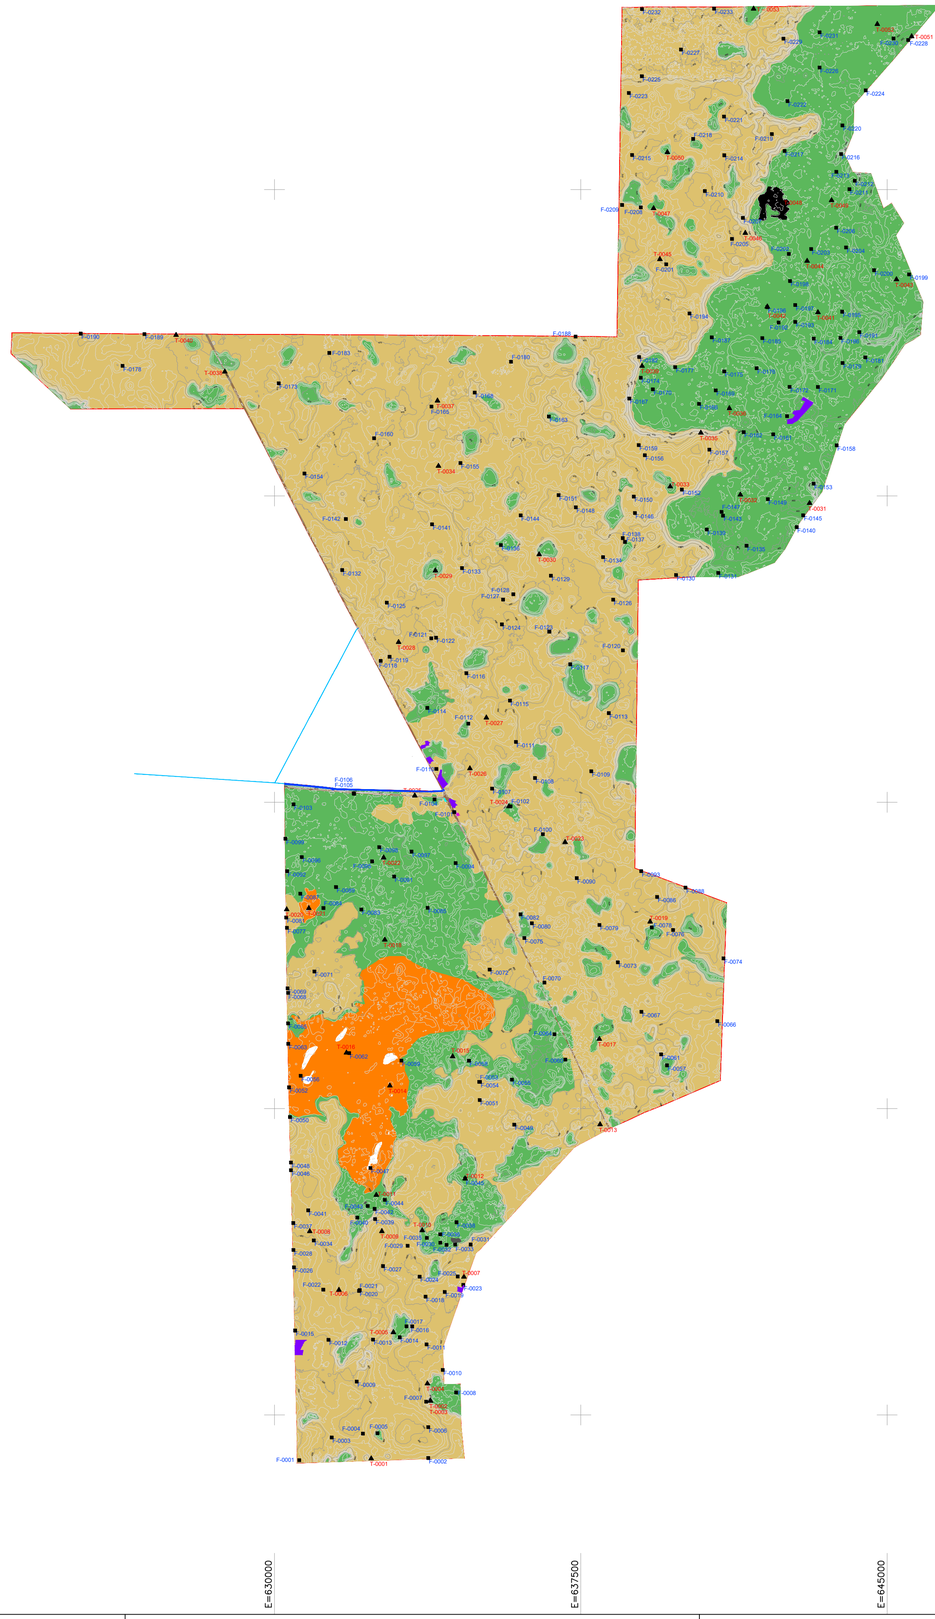

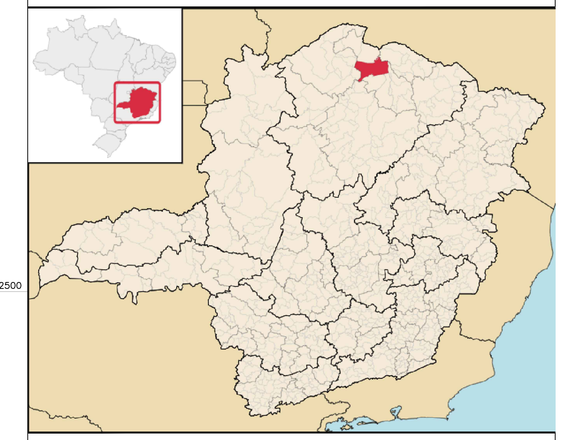

NOTAS:

1 - MEDIDAS, COORDENADAS E ELEVAÇÕES EM METRO.
2 - DATUM HORIZONTAL SIRGAS2000 - FUSO 23 - MC 45º WGr.
3 - DATUM VERTICAL: MODELO GEOIDE HGEOHNOR2020 – MARÉGRAFO IMBITUBA - SC

CLASSE DE IRRIGAÇÃO	ÁREA (ha)	%
2IA	8.984,99	30,294
2IC	19.181,50	64,673
3ZI	1.291,15	4,353
4ZC	40,24	0,136
AFLORAMENTO	38,37	0,129
POVOADO	30,69	0,103
FAIXA DE DOMÍNIO RODOVIA	79,33	0,267
CANAL DE ADUÇÃO	12,14	0,041
POSTO DE GASOLINA	0,54	0,002
COPASA	0,23	0,001
TOTAL	29.659,18	100,000

PARÂMETROS LIMITANTES REPRESENTATIVOS DO SOLO:
A - Minerologia de argila
C - Capacidade de água disponível
I - Velocidade de infiltração básica
Z - Profundidade

LEGENDA:

PERÍMETRO DO PROJETO DE IRRIGAÇÃO JAÍBA (ETAPAS III E IV)

CURVAS DE NÍVEL

TRINCHEIRA

TRADAGEM

NOMENCLATURA:

TRINCHEIRA
NÚMERO TRINCHEIRA
T-001

TRADAGEM
NÚMERO TRADAGEM
F-001

0	XX/XX	Emissão Inicial	XXX	XXX	XXX	XXX
Revisão	Data	Descrição	Elab.	Verif.	Aprov.	Aut.

FUNDO DE DESENVOLVIMENTO DA INFRAESTRUTURA REGIONAL SUSTENTÁVEL - FDIRS

ESTRUTURAÇÃO DE PROJETO DE CONCESSÃO DO PERÍMETRO IRRIGADO DO JAÍBA (ETAPAS III E IV)

ANTEPROJETO

ESTUDOS PEDOLÓGICOS
MAPA DE CLASSIFICAÇÃO DE TERRAS PARA IRRIGAÇÃO
COM CURVA DE NÍVEL

Finalidade de Emissão	1 Para Informação	2 Para Comentários	3 Para Aprovação	4 Para Execução	5 Como Construído	6 Para Utilização	7 Para Providências

Data: 01/09/25	Elaboração:		Verificação:	
Escala: 1:75.000	Aprovação	XXX / XXX	Autorização	XXX / XXX
Referência:	Revisão: RV00	Desenho nº JB_E3-4.07.PDL.DE.004		