

E=632500 E=635000 E=637500 E=640000 E=642500 E=645000

N=8340000 N=8337500 N=8335000 N=8332500 N=8330000 N=8327500

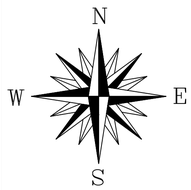

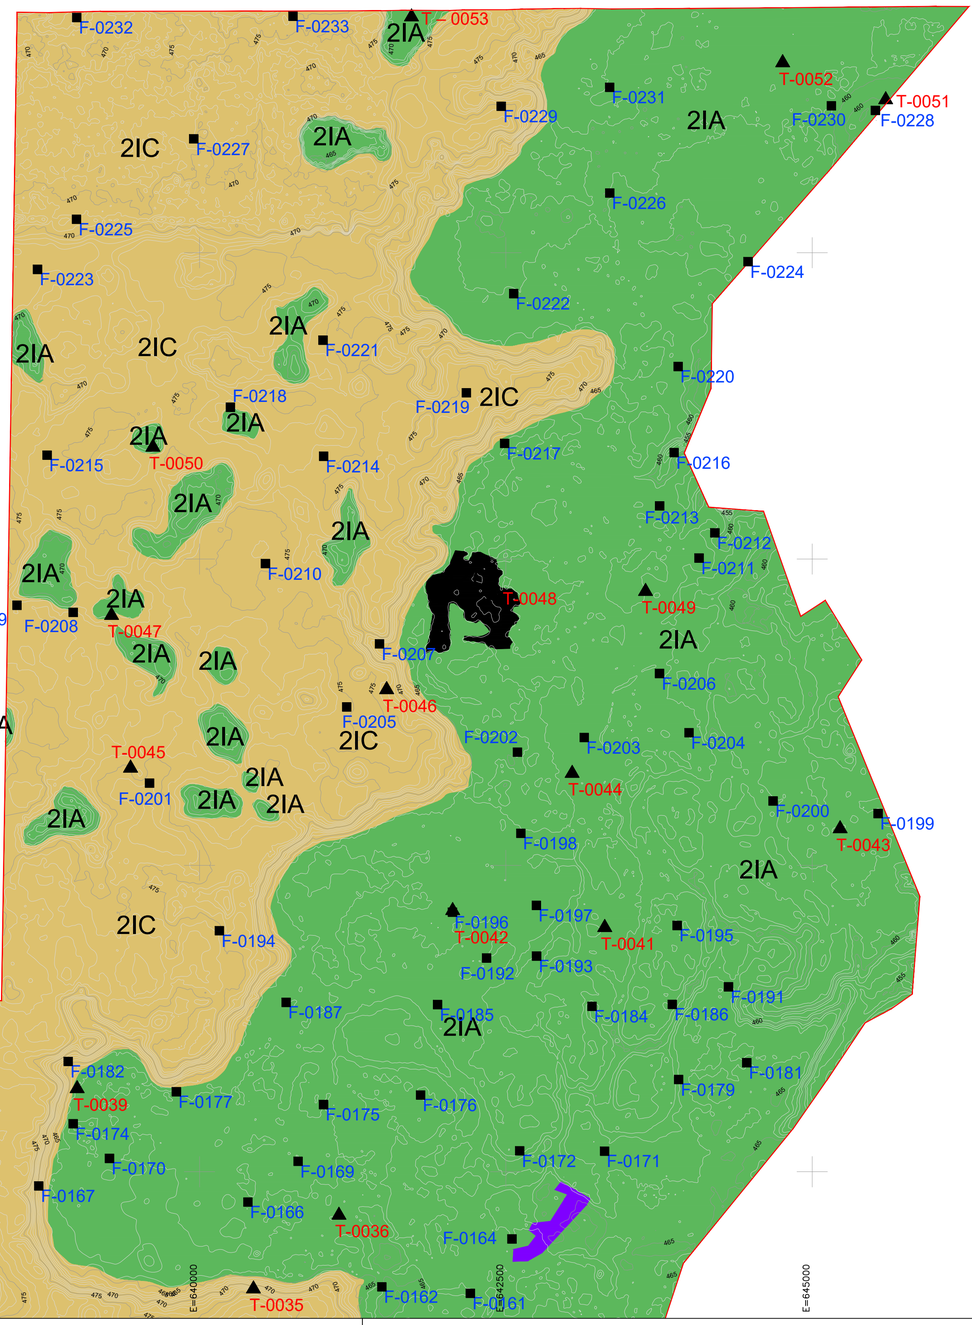


NOTAS:

1 - MEDIDAS, COORDENADAS E ELEVAÇÕES EM METRO.
2 - DATUM HORIZONTAL SIRGAS2000 - FUSO 23 - MC 45º WGr.
3 - DATUM VERTICAL: MODELO GEOIDE HGEOHNOR2020 – MARÉGRAFO IMBITUBA - SC

| CLASSE DE IRRIGAÇÃO | ÁREA (ha) | % |
|---|---|---|
| 2IA | 8.984,99 | 30,294 |
| 2IC | 19.181,50 | 64,673 |
| 3ZI | 1.291,15 | 4,353 |
| 4ZC | 40,24 | 0,136 |
| AFLORAMENTO | 38,37 | 0,129 |
| POVOADO | 30,69 | 0,103 |
| FAIXA DE DOMÍNIO RODOVIA | 79,33 | 0,267 |
| CANAL DE ADUÇÃO | 12,14 | 0,041 |
| POSTO DE GASOLINA | 0,54 | 0,002 |
| COPASA | 0,23 | 0,001 |
| TOTAL | 29.659,18 | 100,000 |

PARÂMETROS LIMITANTES REPRESENTATIVOS DO SOLO:
A - Minerologia de argila
C - Capacidade de água disponível
I - Velocidade de infiltração básica
Z - Profundidade

LEGENDA:

PERÍMETRO DO PROJETO DE IRRIGAÇÃO JAÍBA (ETAPAS III E IV)

CURVAS DE NÍVEL


TRINCHEIRA

TRADAGEM

NOMENCLATURA:

TRINCHEIRA
NÚMERO TRINCHEIRA
T-001
TRADAGEM
NÚMERO TRADAGEM
F-001

ARTICULAÇÃO:

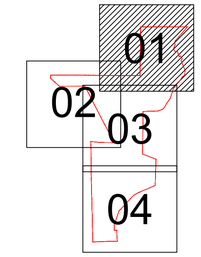


| Revisão | Data | Descrição | Elab. | Verif. | Aprov. | Aut. |
|---|---|---|---|---|---|---|
| 0 | XX/XX | Emissão Inicial | XXX | XXX | XXX | XXX |

FUNDO DE DESENVOLVIMENTO DA INFRAESTRUTURA REGIONAL SUSTENTÁVEL - FDIRS

ESTRUTURAÇÃO DE PROJETO DE CONCESSÃO DO PERÍMETRO IRRIGADO DO JAÍBA (ETAPAS III E IV)

ANTEPROJETO

ESTUDOS PEDOLÓGICOS
MAPA DE CLASSIFICAÇÃO DE TERRAS PARA IRRIGAÇÃO COM CURVA DE NÍVEL

| Finalidade de Emissão | 1 Para Informação | 2 Para Comentários | 3 Para Aprovação | 4 Para Execução | 5 Como Construído | 6 Para Utilização | 7 Para Providências |
|---|---|---|---|---|---|---|---|

| | | | |
|---|---|---|---|
| Data: 01/09/25 | Elaboração: | Verificação: | |
| Escala: 1:25.000 | Aprovação: XXX / XXX | Autorização: XXX / XXX | |
| Referência: | Revisão: RV00 | Desenho nº: JB_E3-4.07.PDL.DE.006 | |