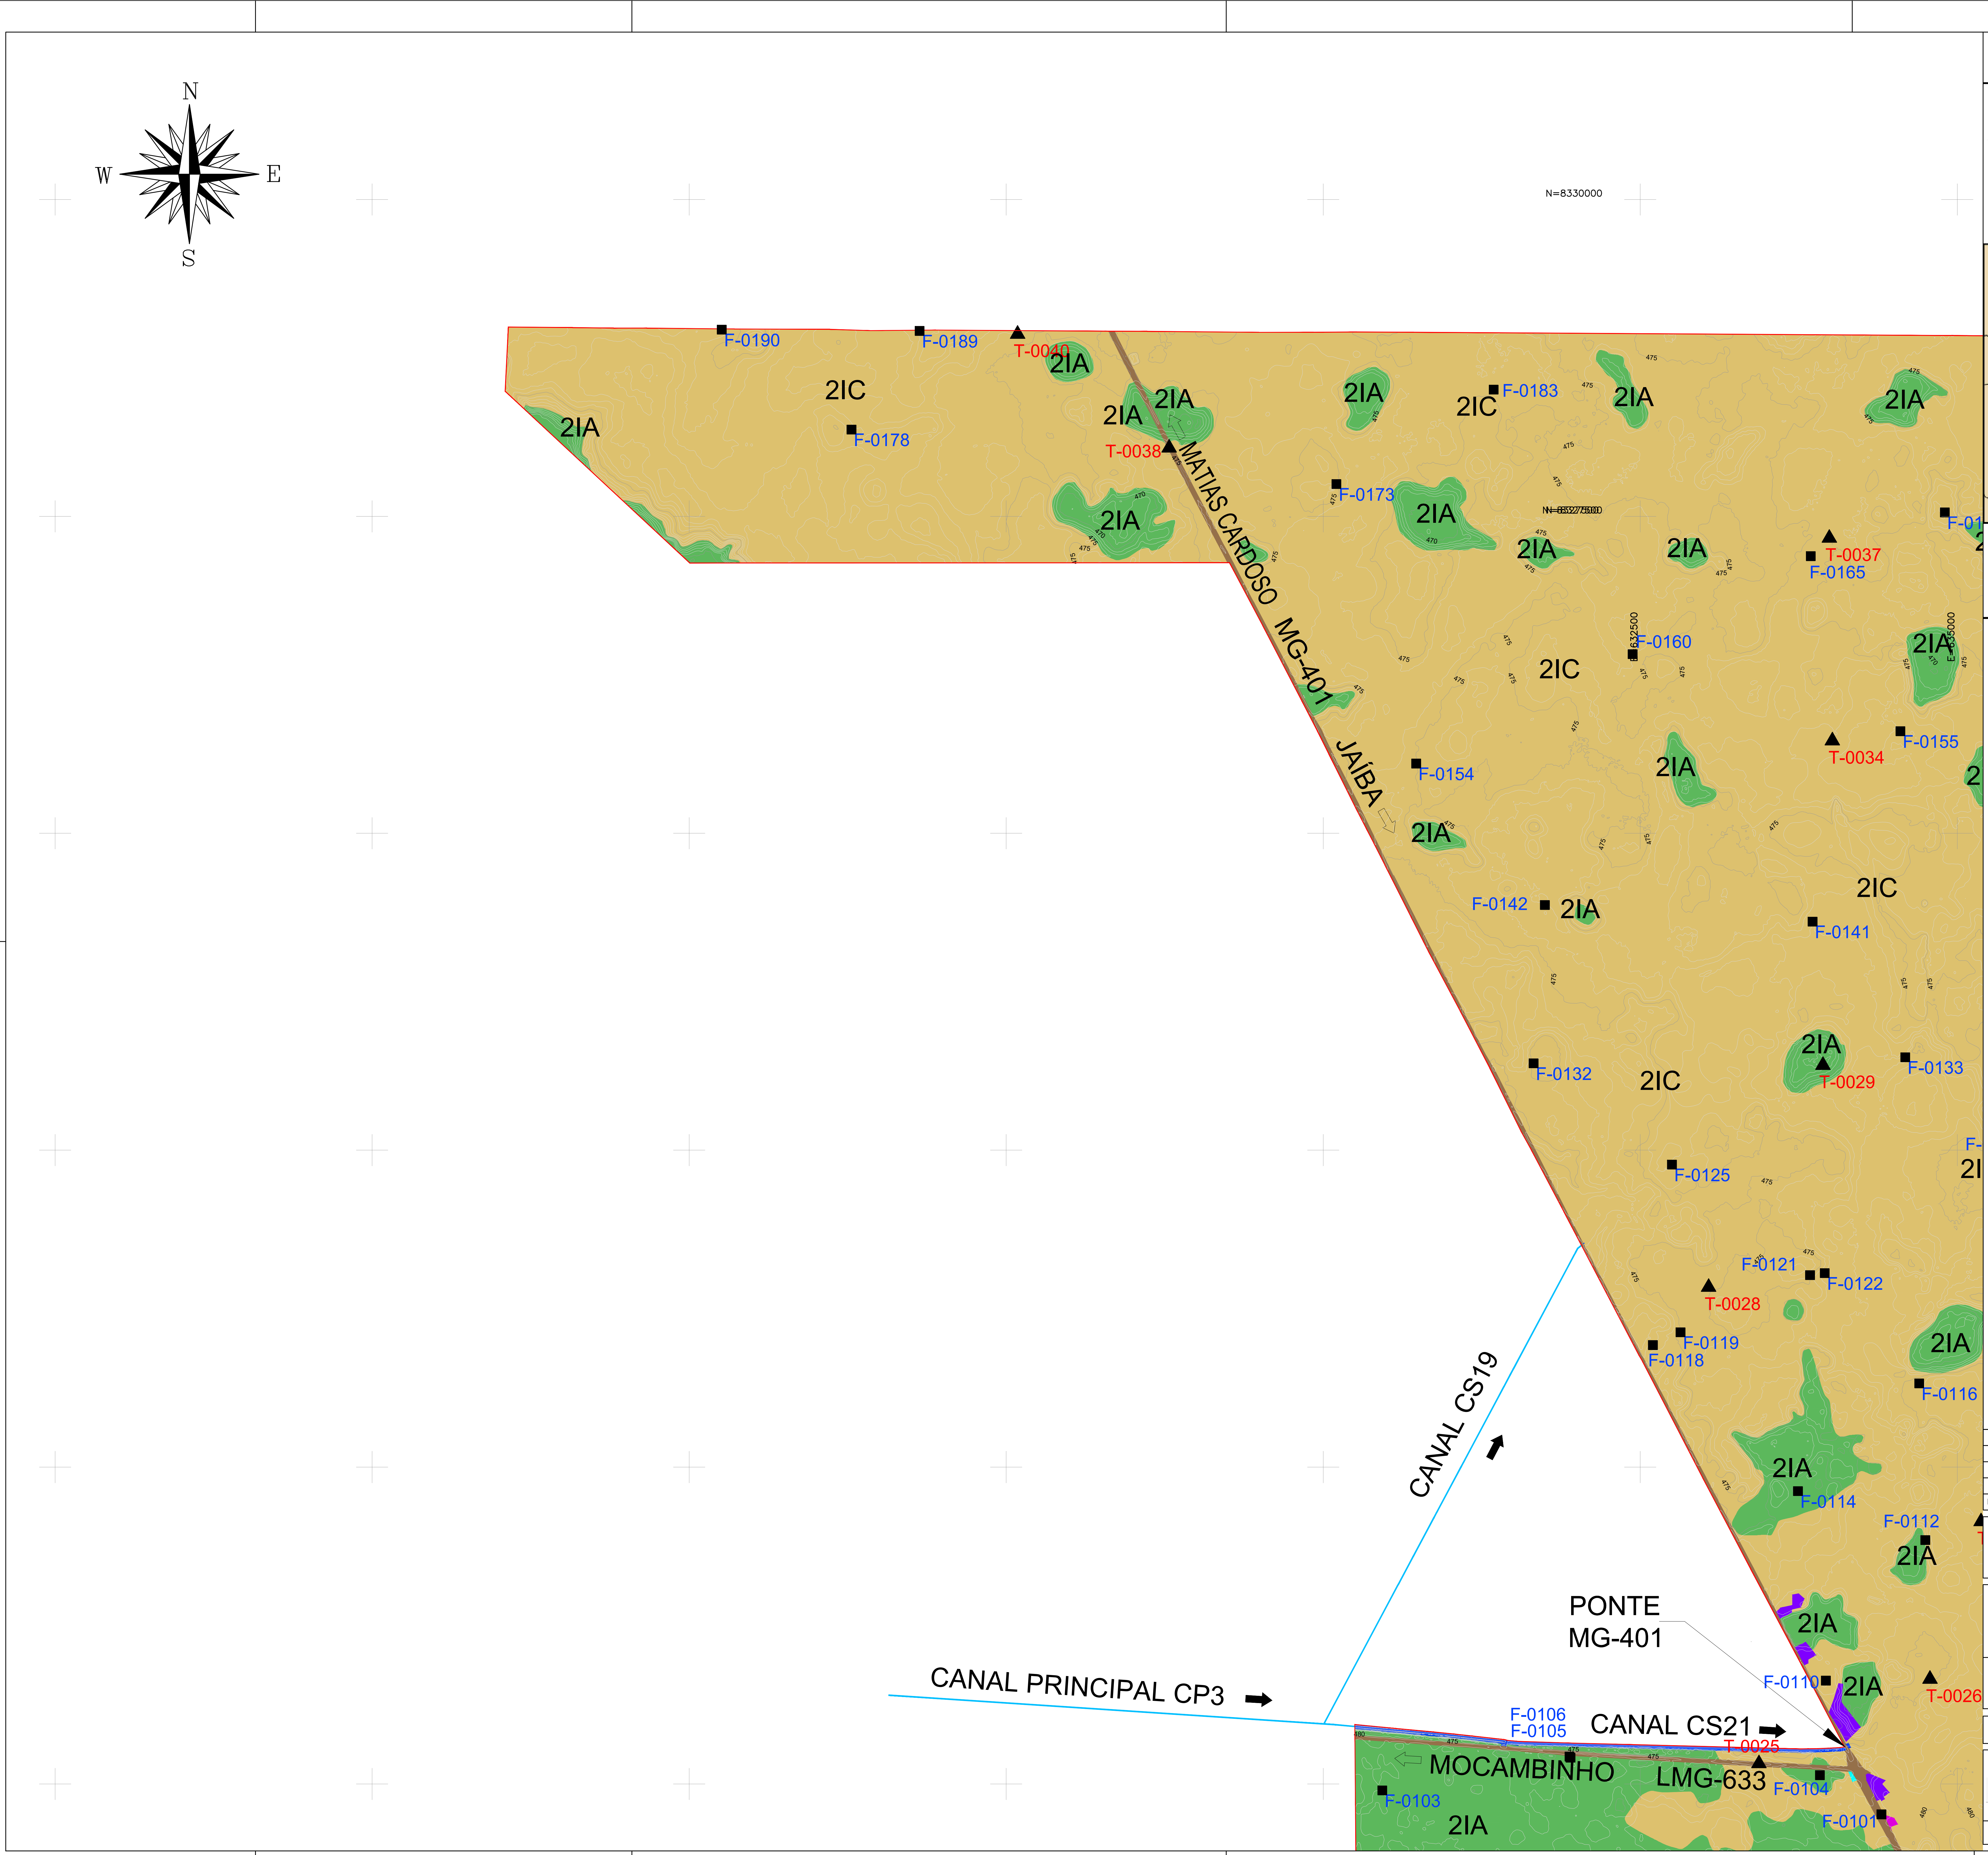
N
W
E
S
N=8330000
N=8327500
E=632500
E=635000
F-0190
F-0189
T-0040
2IA
2IC
F-0178
2IA
2IA
2IA
T-0038
2IA
MATIAS CARDOSO MG-401 JAÍBA
2IA
2IC
F-0183
2IA
2IA
F-0173
2IA
2IA
2IA
T-0037
F-0165
F-01
2IA
2IC
F-0160
F-0155
T-0034
2IA
F-0154
2IA
F-0142
2IA
2IC
F-0141
2IA
T-0029
F-0133
F-0132
2IC
F-0125
F-0121
F-0122
T-0028
F-0119
F-0118
2IA
F-0116
2IA
F-0114
F-0112
2IA
2IA
F-0110
2IA
T-0026
CANAL CS19
CANAL PRINCIPAL CP3
PONTE MG-401
CANAL CS21
F-0106
F-0105
T-0025
MOCAMBINHO
LMG-633
F-0104
F-0103
2IA
F-0101
475
470
480

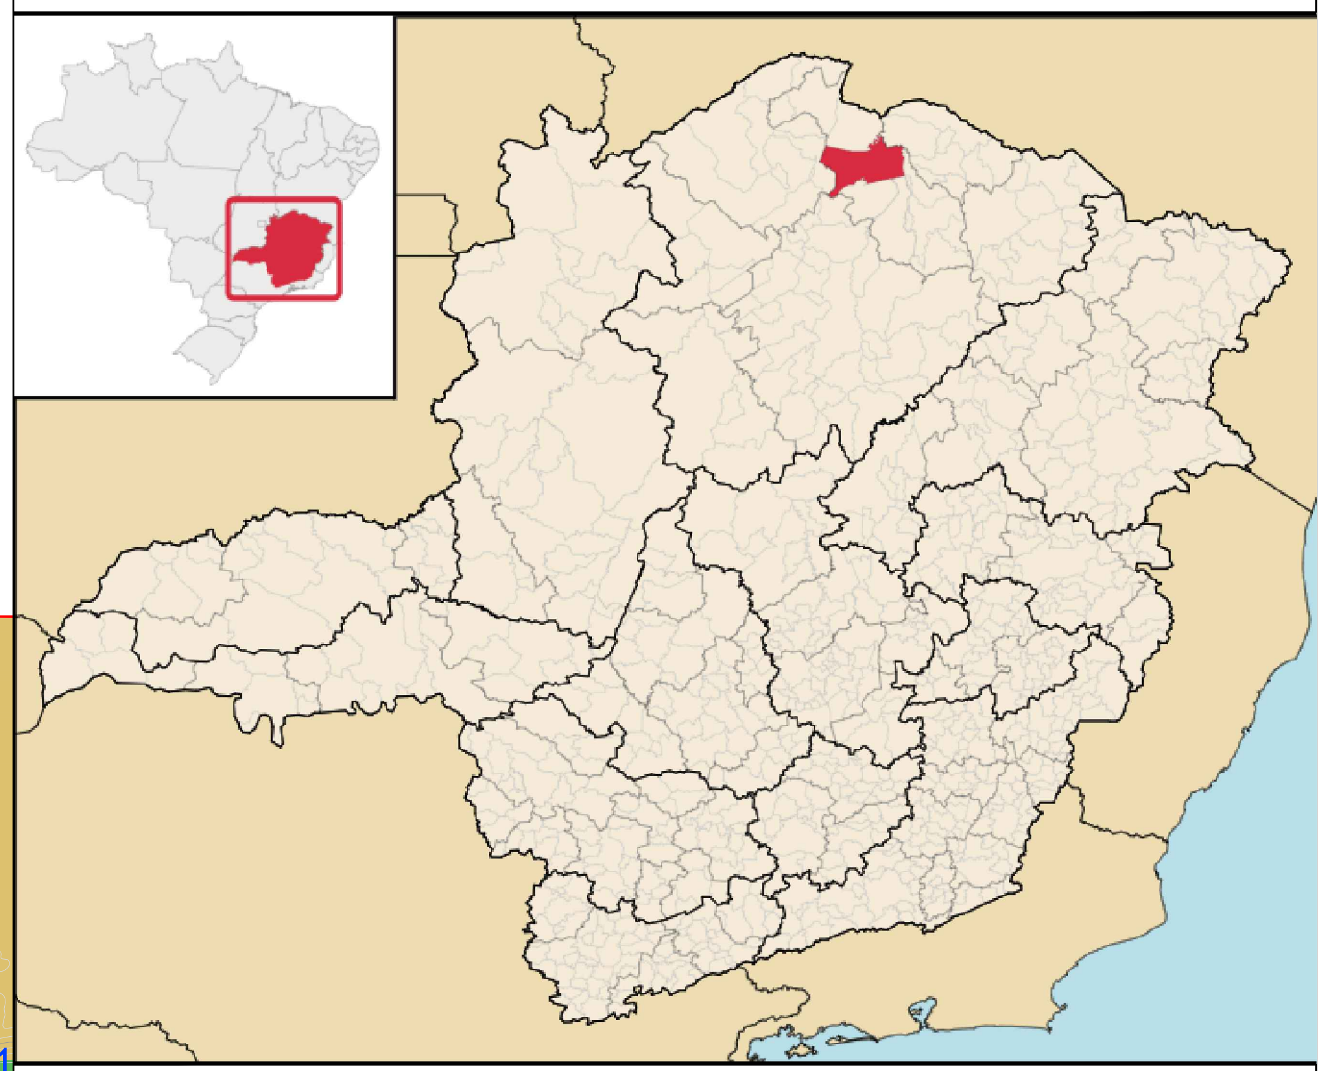

NOTAS:

1 - MEDIDAS, COORDENADAS E ELEVAÇÕES EM METRO.
2 - DATUM HORIZONTAL SIRGAS2000 - FUSO 23 - MC 45º WGr.
3 - DATUM VERTICAL: MODELO GEOIDE HGEOHNOR2020 – MARÉGRAFO IMBITUBA - SC

CLASSE DE IRRIGAÇÃO		ÁREA (ha)	%
🟩	2IA	8.984,99	30,294
🟨	2IC	19.181,50	64,673
🟧	3ZI	1.291,15	4,353
⬛	4ZC	40,24	0,136
⬛	AFLORAMENTO	38,37	0,129
🟪	POVOADO	30,69	0,103
🟫	FAIXA DE DOMÍNIO RODOVIA	79,33	0,267
🟦	CANAL DE ADUÇÃO	12,14	0,041
🟪	POSTO DE GASOLINA	0,54	0,002
🟦	COPASA	0,23	0,001
TOTAL		29.659,18	100,000

PARÂMETROS LIMITANTES REPRESENTATIVOS DO SOLO:
A - Minerologia de argila
C - Capacidade de água disponível
I - Velocidade de infiltração básica
Z - Profundidade

LEGENDA:

PERÍMETRO DO PROJETO DE IRRIGAÇÃO JAÍBA (ETAPAS III E IV)
415 410 CURVAS DE NÍVEL
▲ TRINCHEIRA
■ TRADAGEM

NOMENCLATURA:

TRINCHEIRA
NÚMERO TRINCHEIRA
T-001

TRADAGEM
NÚMERO TRADAGEM
F-001

ARTICULAÇÃO:

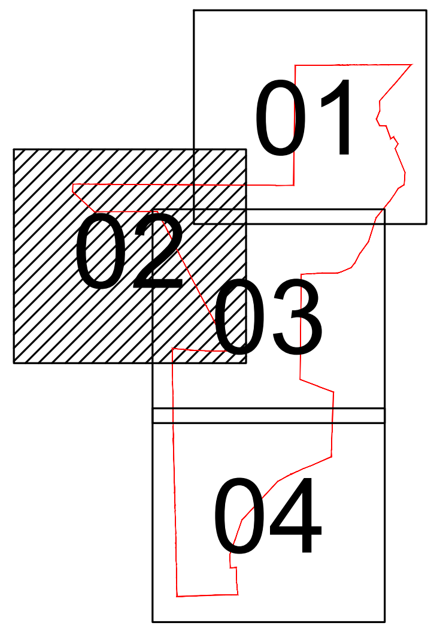

Revisão	Data	Descrição	Elab.	Verif.	Aprov.	Aut.
0	XX/XX	Emissão Inicial	XXX	XXX	XXX	XXX

FUNDO DE DESENVOLVIMENTO DA INFRAESTRUTURA
REGIONAL SUSTENTÁVEL - FDIRS

ESTRUTURAÇÃO DE PROJETO DE CONCESSÃO DO PERÍMETRO IRRIGADO DO JAÍBA (ETAPAS III E IV)

ANTEPROJETO

ESTUDOS PEDOLÓGICOS

MAPA DE CLASSIFICAÇÃO DE TERRAS PARA IRRIGAÇÃO
COM CURVA DE NÍVEL

Finalidade de Emissão	1 Para Informação	2 Para Comentários	3 Para Aprovação	4 Para Execução	5 Como Construído	6 Para Utilização	7 Para Providências

MP Moysés & Pires — ENGECORPS — A&M Plena

Data: 01/09/25
Escala: 1:25.000
Elaboração:
Verificação:
Aprovação: XXX XXX
Autorização: XXX XXX
Referência:
Revisão: RV00
Desenho nº JB_E3-4.07.PDL.DE.006