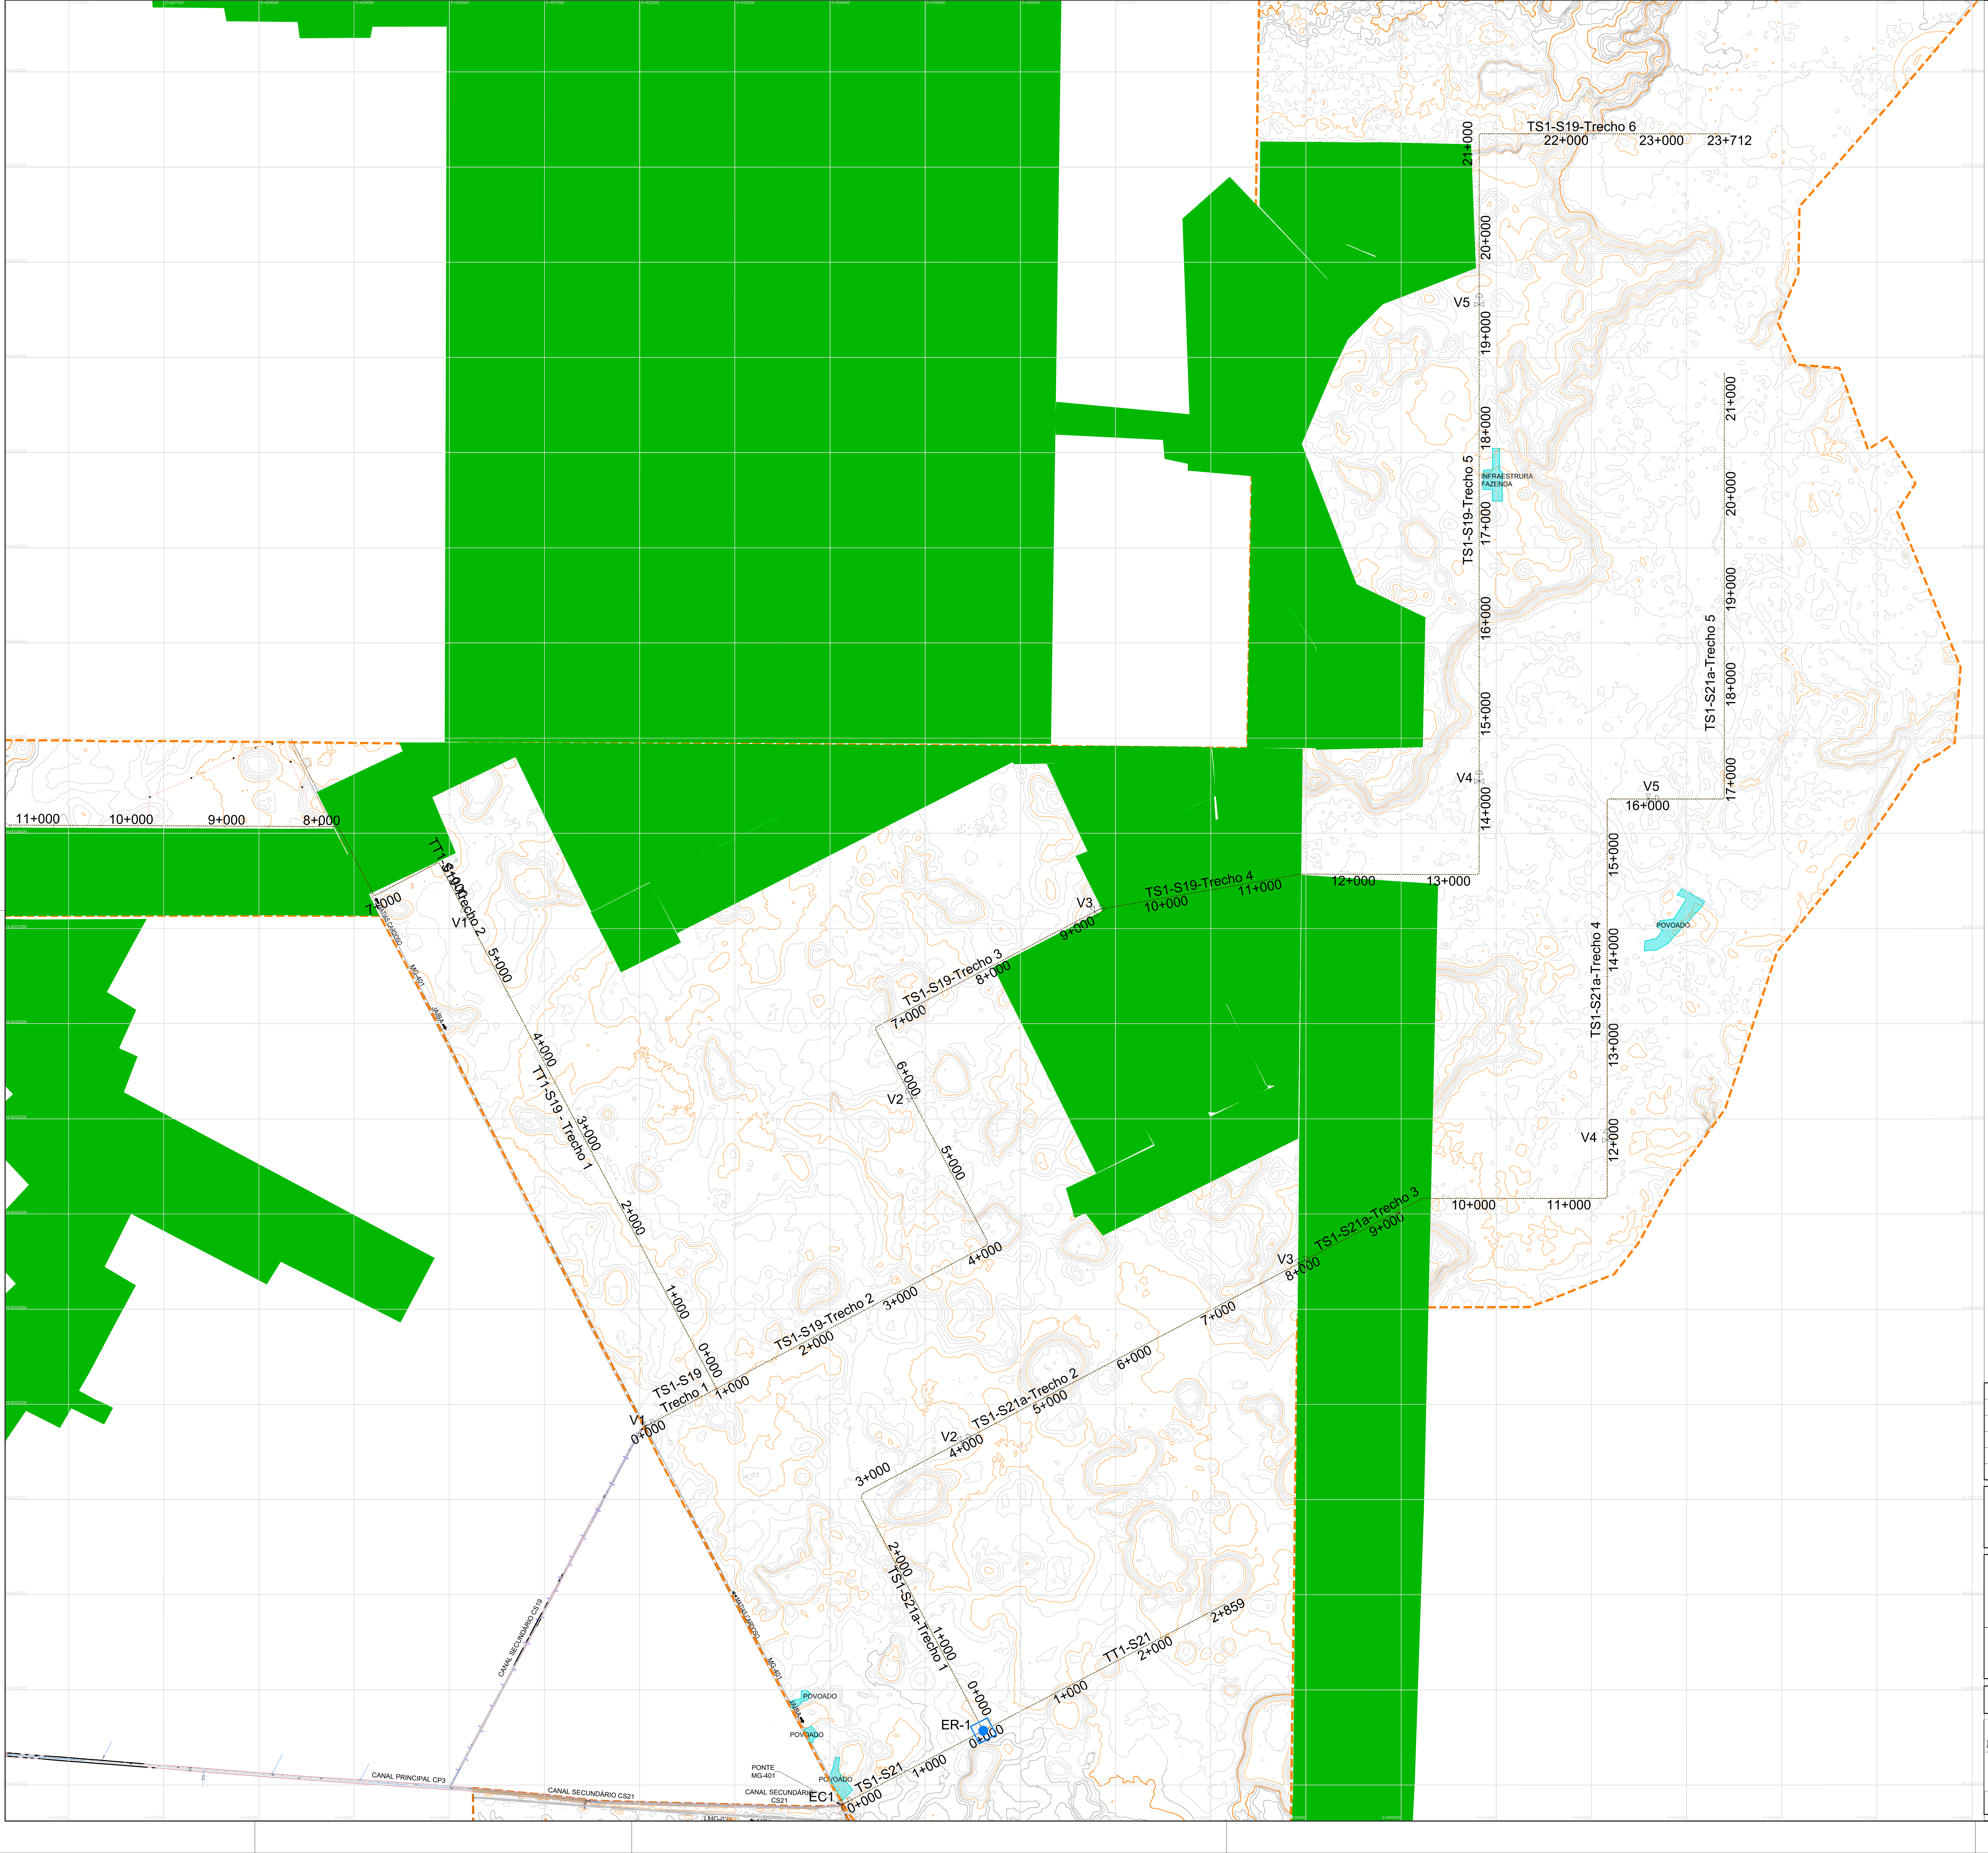

LEGENDA:

- - - LIMITE - JAÍBA III
☐ TUBO ADUTOR
🟩 ÁREAS AMBIENTAIS SENSÍVEIS
● ELEVATÓRIA DE RECALQUE (ER-1)
⧖ VÁLVULA DE CONTROLE (V)

NOTAS:

1 - ÁREA IRRIGADA DOS LOTES EM HECTARES (93% ÁREA BRUTA IRRIGÁVEL);
2 - MEDIDAS EM METRO, EXCETO INDICAÇÃO CONTRÁRIA;
3 - ESTAQUEMANTO INDICADO EM km.

0	19/09/2025	Emissão Inicial	AHL	HKO	EDK	
Revisão	Data	Descrição	Elab.	Verif.	Aprov.	Aut.

FUNDO DE DESENVOLVIMENTO DA INFRAESTRUTURA
REGIONAL SUSTENTÁVEL - FDIRS

ESTRUTURAÇÃO DE PROJETO DE CONCESSÃO DO
PERÍMETRO IRRIGADO DO JAÍBA (ETAPAS 3 E 4)

ANTEPROJETO

ALTERNATIVA 2 - SISTEMA ADUTOR POR TUBO
ETAPA 3

Finalidade de Emissão	1 Para Informação	2 Para Comentários	▨3 Para Aprovação	4 Para Execução	5 Como Construído	6 Para Utilização	7 Para Providências

Moysés & Pires Sociedade de advogados
ENGECORPS GrupoTYPSA
A&M
Plena Consultoria e Projetos

Data: 29/08/25
Escala: sem escala
Elaboração:
Verificação:
Aprovação
Autorização
Referência:
Revisão: 00
Desenho nº J3-DS-HI-0005-00