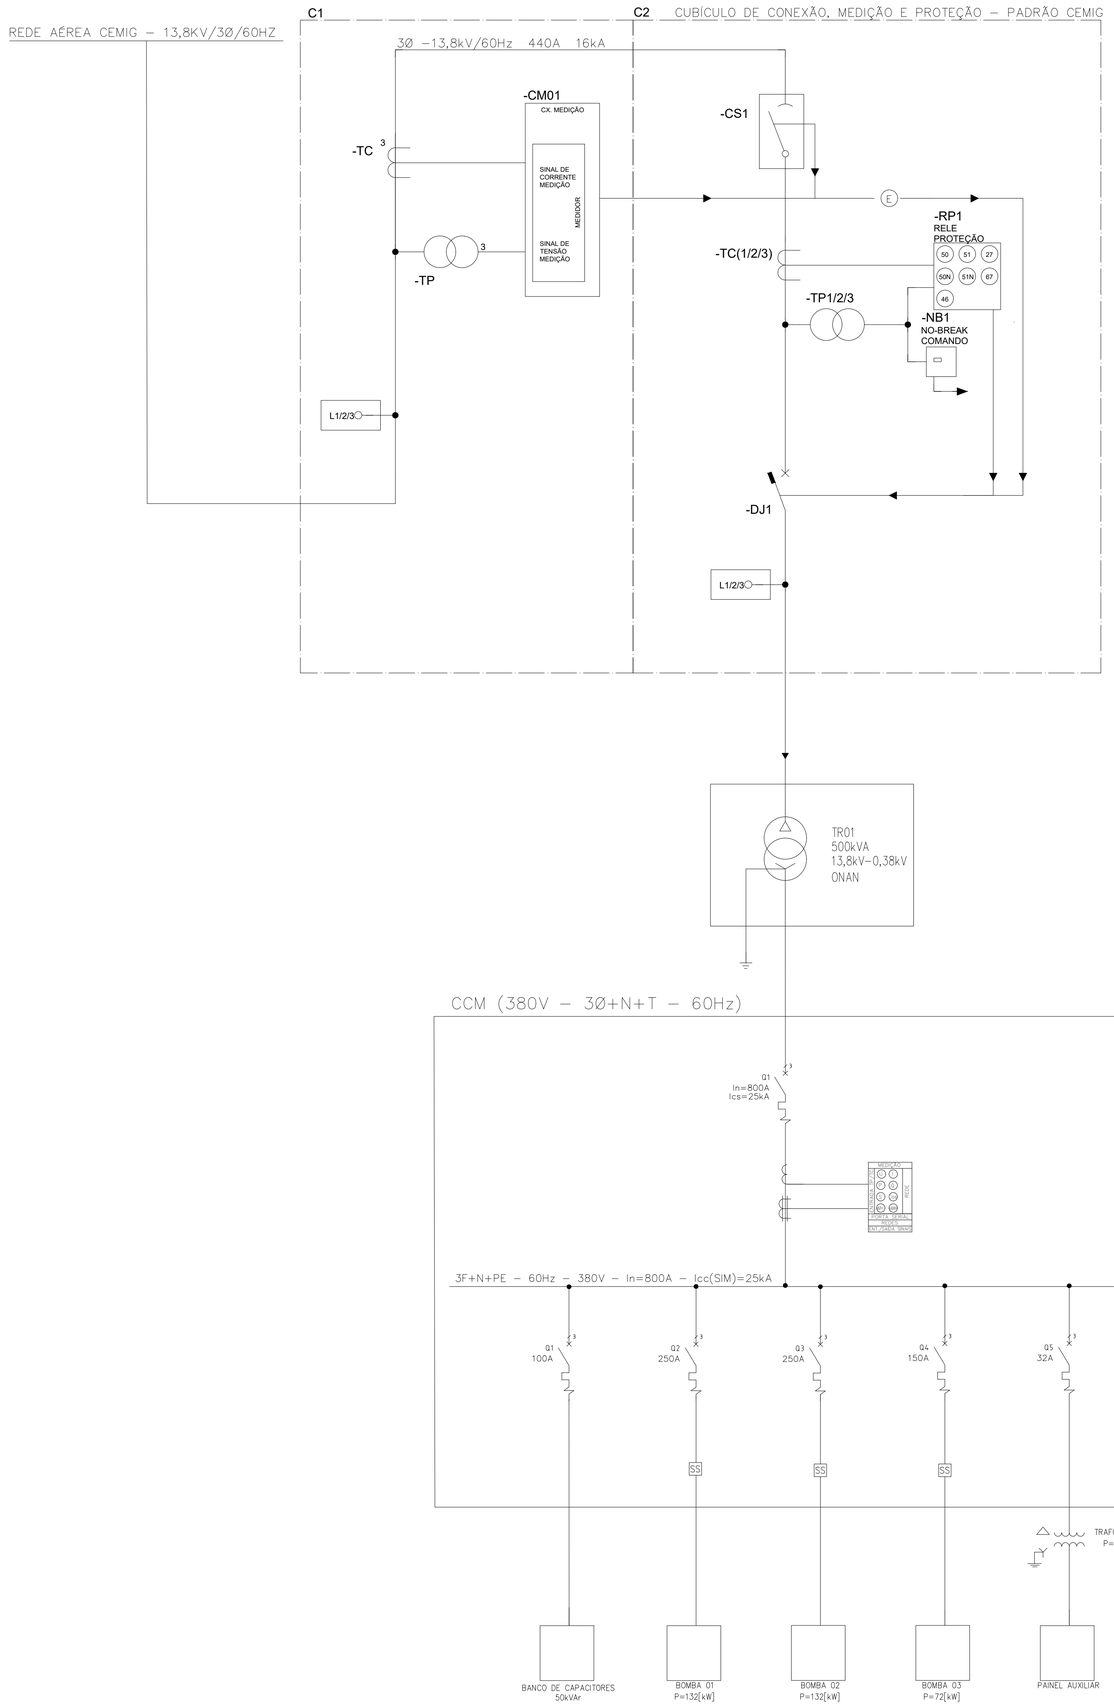


LEGENDA

- TRANSFORMADOR DE FORÇA
- SECCIONADOR
- DISJUNTOR DE CAIXA ABERTA
- SOFT STARTER
- RELÉ DE PROTEÇÃO
- -TC — TRANSFORMADOR DE CORRENTE
- CAIXA DE MEDIÇÃO COM MEDIDOR PADRÃO CEMIG
- TRANSFORMADOR DE POTENCIAL
- L1/2/3 — ISOLADOR
- NOBREAK
- CARGA ELÉTRICA
- TRANSFORMADOR AUXILIAR
- -DJ1 — DISJUNTOR DE MÉDIA TENSÃO

NOTAS:

1- A CABINE DE ENTRADA, PROTEÇÃO E MEDIÇÃO DEVE SER DE ACORDO COM A NORMA DE DISTRIBUIÇÃO ND-5.3 DA CEMIG

Revisão	Data	Descrição	Elab.	Verif.	Aprov.	Aut.
2	23/03/26	Revisado Conforme Comentado	MDCS	AG	ET	
1	19/02/26	Revisado Conforme Comentado	FS	AG	ET	
0	15/12/25	Emissão Inicial	FS	AG	ET	

FUNDO DE DESENVOLVIMENTO DA INFRAESTRUTURA REGIONAL SUSTENTÁVEL - FDIRS

ESTRUTURAÇÃO DE PROJETO DE CONCESSÃO DO PERÍMETRO IRRIGADO DO JAÍBA (ETAPAS 3 E 4)
ANTEPROJETO

DIAGRAMA UNFILAR
ESTAÇÃO DE RECALQUE ER1 - ETAPA 3

Finalidade de Emissão	Para Informação	2 Para Comentários	3 Para Aprovação	4 Para Execução	5 Como Construído	6 Para Utilização	7 Para Providências

Data: 23/03/26	Elaboração:		Verificação:
Escala: S/E	Aprovação		Autorização
Referência: EGC006-EL3-0001	Revisão: 2	Desenho nº EGC006-EL2-0001	