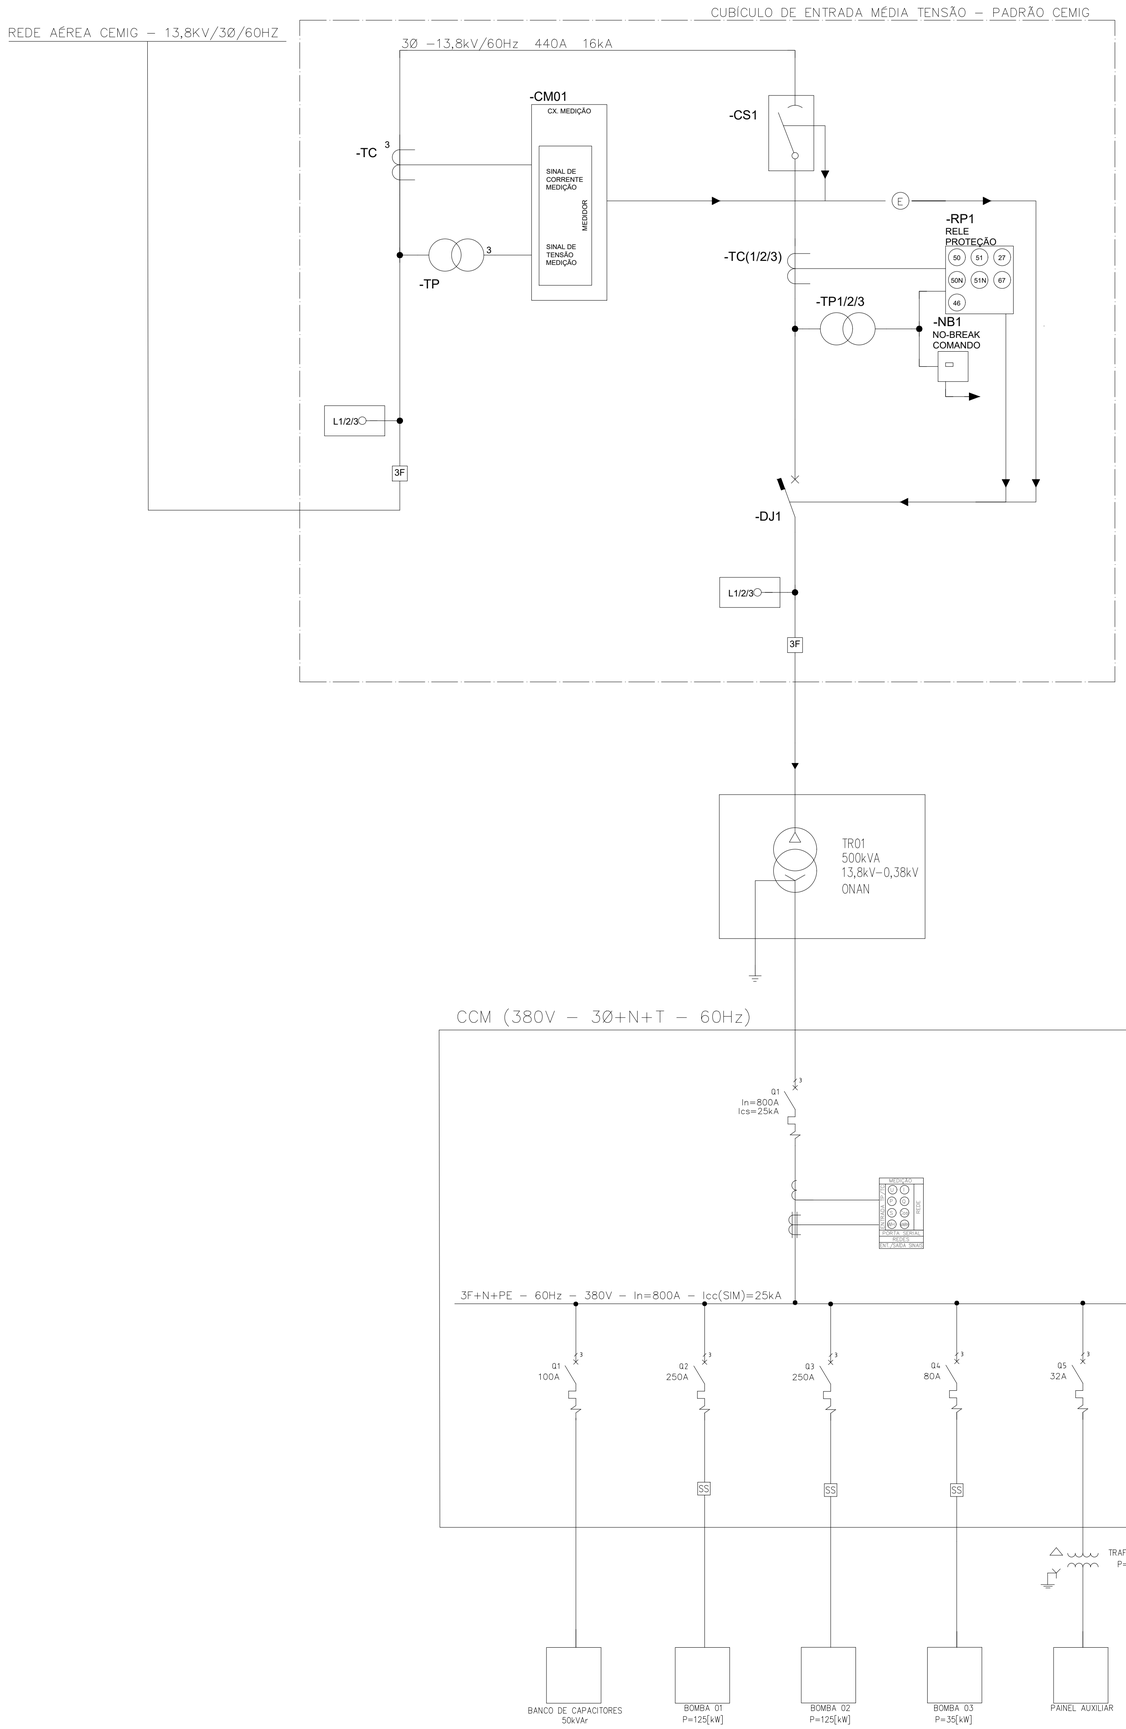



## LEGENDA

- TRANSFORMADOR DE FORÇA
- SECCIONADOR
- DISJUNTOR DE CAIXA ABERTA
- SOFT STARTER
- RELÉ DE PROTEÇÃO
- -TC — TRANSFORMADOR DE CORRENTE
- -CM01 CX. MEDIÇÃO — SINAL DE CORRENTE MEDIÇÃO — MEDIDOR — SINAL DE TENSÃO MEDIÇÃO — CAIXA DE MEDIÇÃO COM MEDIDOR PADRÃO CEMIG
- TRANSFORMADOR DE POTENCIAL
- L1/2/3 — ISOLADOR
- NOBREAK
- CARGA ELÉTRICA
- TRANSFORMADOR AUXILIAR
- DISJUNTOR DE MÉDIA TENSÃO

NOTAS:

1- A CABINE DE ENTRADA, PROTEÇÃO E MEDIÇÃO DEVE SER DE ACORDO COM A NORMA DE DISTRIBUIÇÃO ND-5.3 DA CEMIG

| Revisão | Data | Descrição | Elab. | Verif. | Aprov. | Aut. |
|---|---|---|---|---|---|---|
| | | | | | | |
| | | | | | | |
| 2 | 24/03/26 | Revisão Conforme Comentado | FS | LAT | ET | |
| 1 | 19/02/26 | Revisão Conforme Comentado | FS | LAT | ET | |
| 0 | 15/12/25 | Emissão Inicial | FS | LAT | ET | |

FUNDO DE DESENVOLVIMENTO DA INFRAESTRUTURA REGIONAL SUSTENTÁVEL - FDIRS

ESTRUTURAÇÃO DE PROJETO DE CONCESSÃO DO PERÍMETRO IRRIGADO DO JAÍBA (ETAPAS 3 E 4)

ANTEPROJETO

DIAGRAMA UNIFILAR

ESTAÇÃO DE RECALQUE ER1 - ETAPA 4

Finalidade de Emissão: Para Informação | 2 Para Comentários | 3 Para Aprovação | 4 Para Execução | 5 Como Construído | 6 Para Utilização | 7 Para Providências

MP Moyses & Pires — ENGECORPS Consórcio — ASA — Plena Consultoria e Projetos

Data: 19/02/26 | Elaboração: | Verificação:

Escala: S/E | Aprovação | Autorização

Referência: EGC006-EL3-0002 | Revisão: 1 | Desenho nº EGC006-EL2-0002