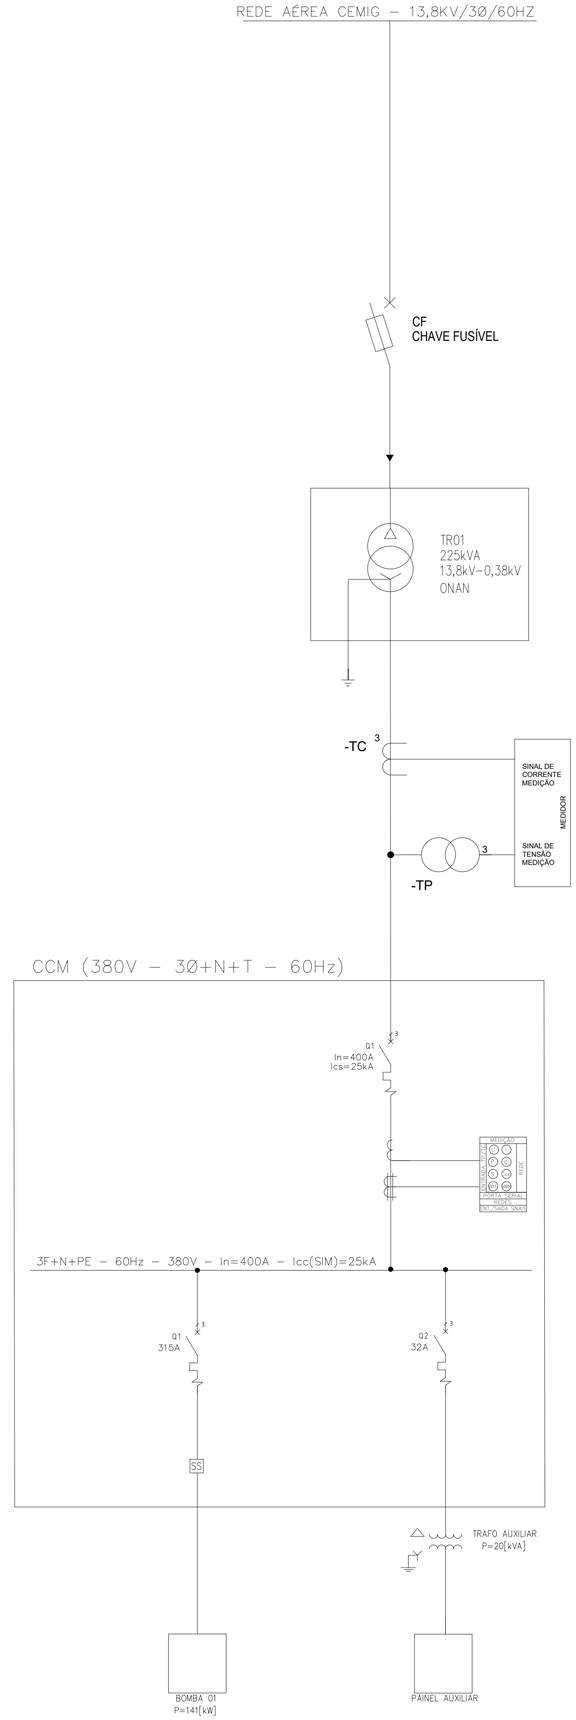


LEGENDA

- TRANSFORMADOR DE FORÇA
- TRANSFORMADOR DE POTENCIAL
- DISJUNTOR DE CAIXA ABERTA
- SOFT STARTER
- RELÉ DE PROTEÇÃO
- -TC — TRANSFORMADOR DE CORRENTE
- CARGA ELÉTRICA
- TRANSFORMADOR AUXILIAR
- CHAVE FUSÍVEL

NOTAS:

1- A CABINE DE ENTRADA, PROTEÇÃO E MEDIÇÃO DEVE SER DE ACORDO COM A NORMA DE DISTRIBUIÇÃO ND-5.3 DA CEMIG

Revisão	Data	Descrição	Elab.	Verif.	Aprov.	Aut.
2	24/03/26	Revisado Conforme Comentado	FS	LAT	ET	
1	19/02/26	Revisado Conforme Comentado	FS	LAT	ET	
0	15/12/25	Emissão Inicial	FS	LAT	ET	

FUNDO DE DESENVOLVIMENTO DA INFRAESTRUTURA REGIONAL SUSTENTÁVEL - FDIRS

ESTRUTURAÇÃO DE PROJETO DE CONCESSÃO DO PERÍMETRO IRRIGADO DO JAÍBA (ETAPAS 3 E 4)

ANTEPROJETO

DIAGRAMA UNFILAR

ESTAÇÃO DE RECALQUE ER2 - ETAPA 4

Finalidade de Emissão	Para Informação	2 Para Comentários	3 Para Aprovação	4 Para Execução	5 Como Construído	6 Para Utilização	7 Para Providências

MP Moysés & Pires Engenharia e Projetos — ENGECORPS Consultoria — Plena Consultoria e Projetos

Data: 19/02/26	Elaboração:	Verificação:	
Escala: S/E	Aprovação	Autorização	
Referência: EGC006-EL3-0003	Revisão: 1	Desenho nº	EGC006-EL2-0003