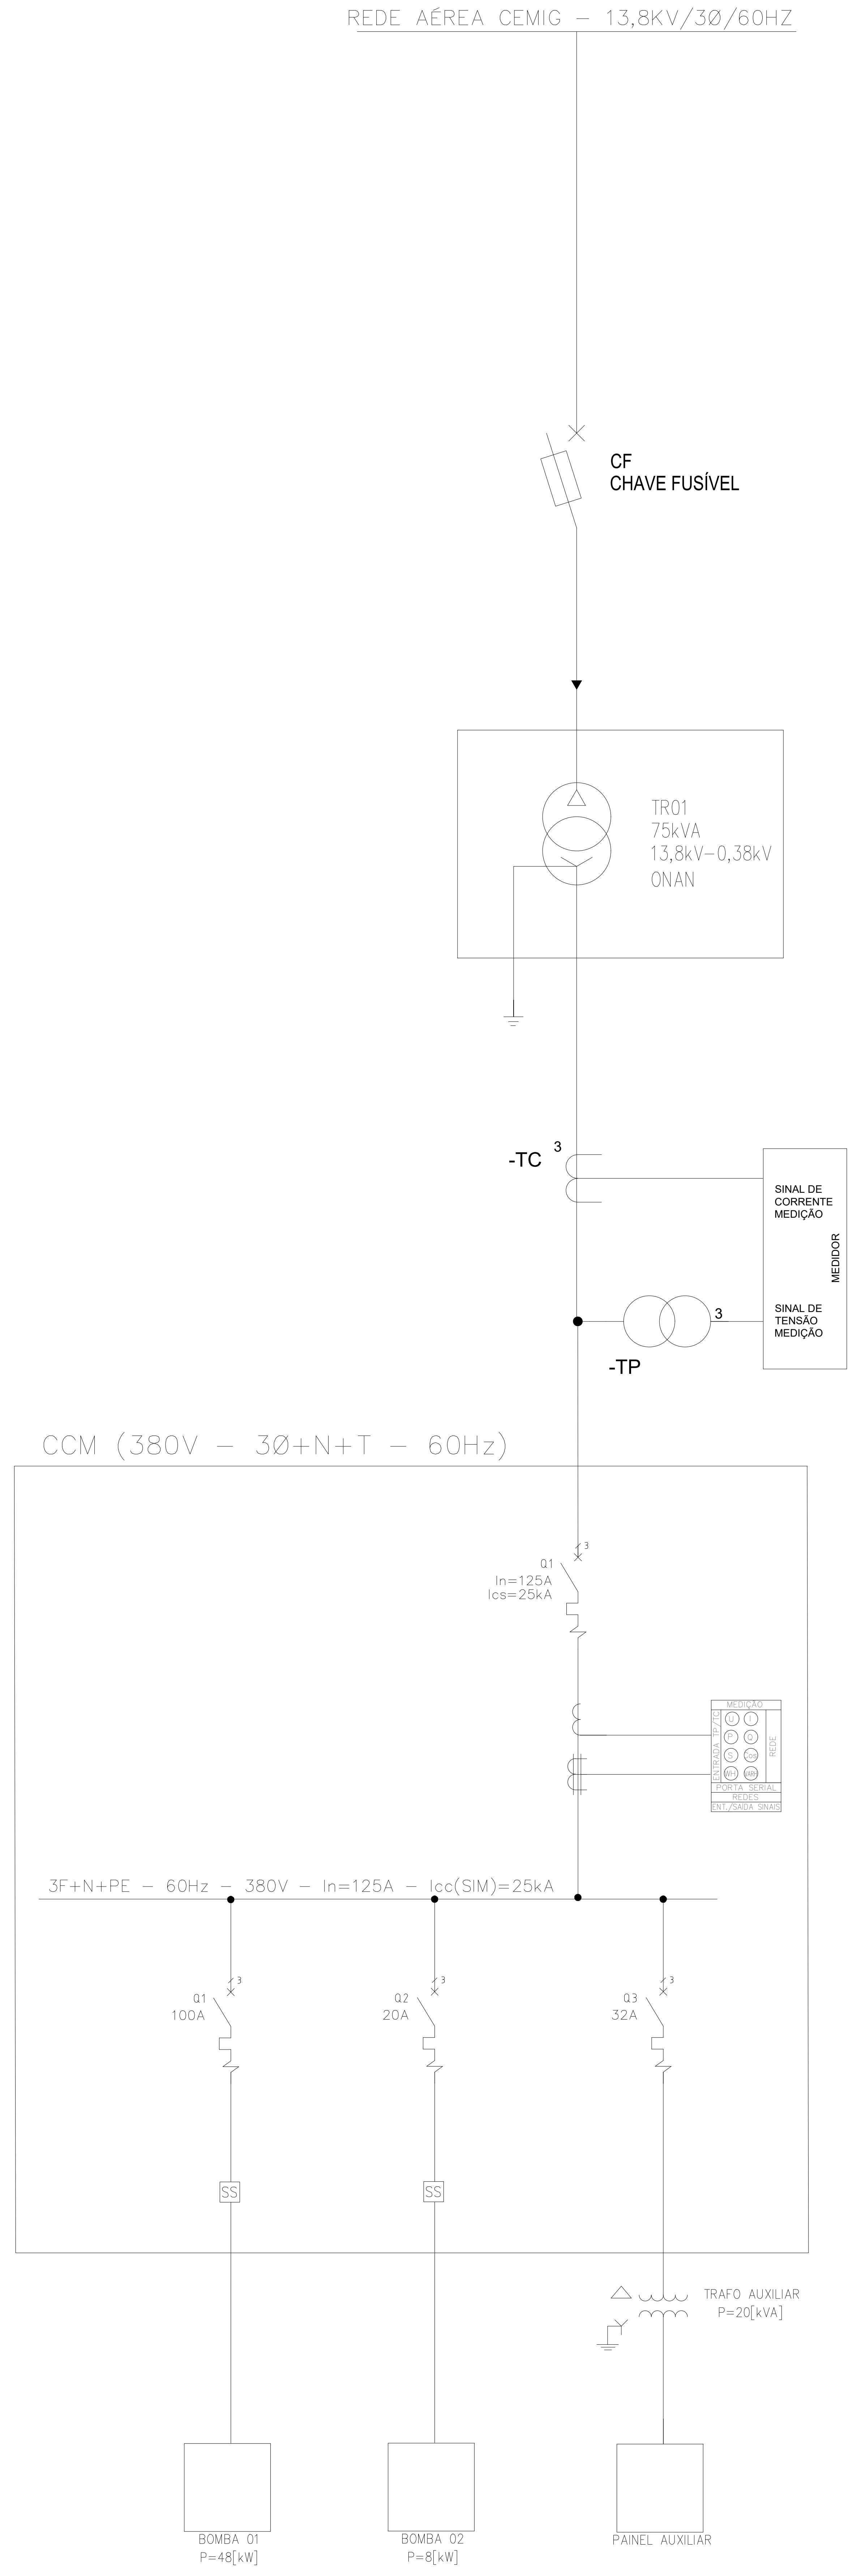
REDE AÉREA CEMIG – 13,8KV/3Ø/60HZ
CF
CHAVE FUSÍVEL
TR01
75kVA
13,8kV–0,38kV
ONAN
-TC
3
SINAL DE CORRENTE MEDIÇÃO
MEDIDOR
SINAL DE TENSÃO MEDIÇÃO
3
-TP
CCM (380V – 3Ø+N+T – 60Hz)
3
Q1
In=125A
Ics=25kA
MEDIÇÃO
ENTRADA TP/TC
U
I
P
Q
S
Cos
WH
VARH
REDE
PORTA SERIAL
REDES
ENT./SAIDA SINAIS
3F+N+PE – 60Hz – 380V – In=125A – Icc(SIM)=25kA
3
Q1
100A
3
Q2
20A
3
Q3
32A
SS
SS
TRAFO AUXILIAR
P=20[kVA]
BOMBA 01
P=48[kW]
BOMBA 02
P=8[kW]
PAINEL AUXILIAR

LEGENDA

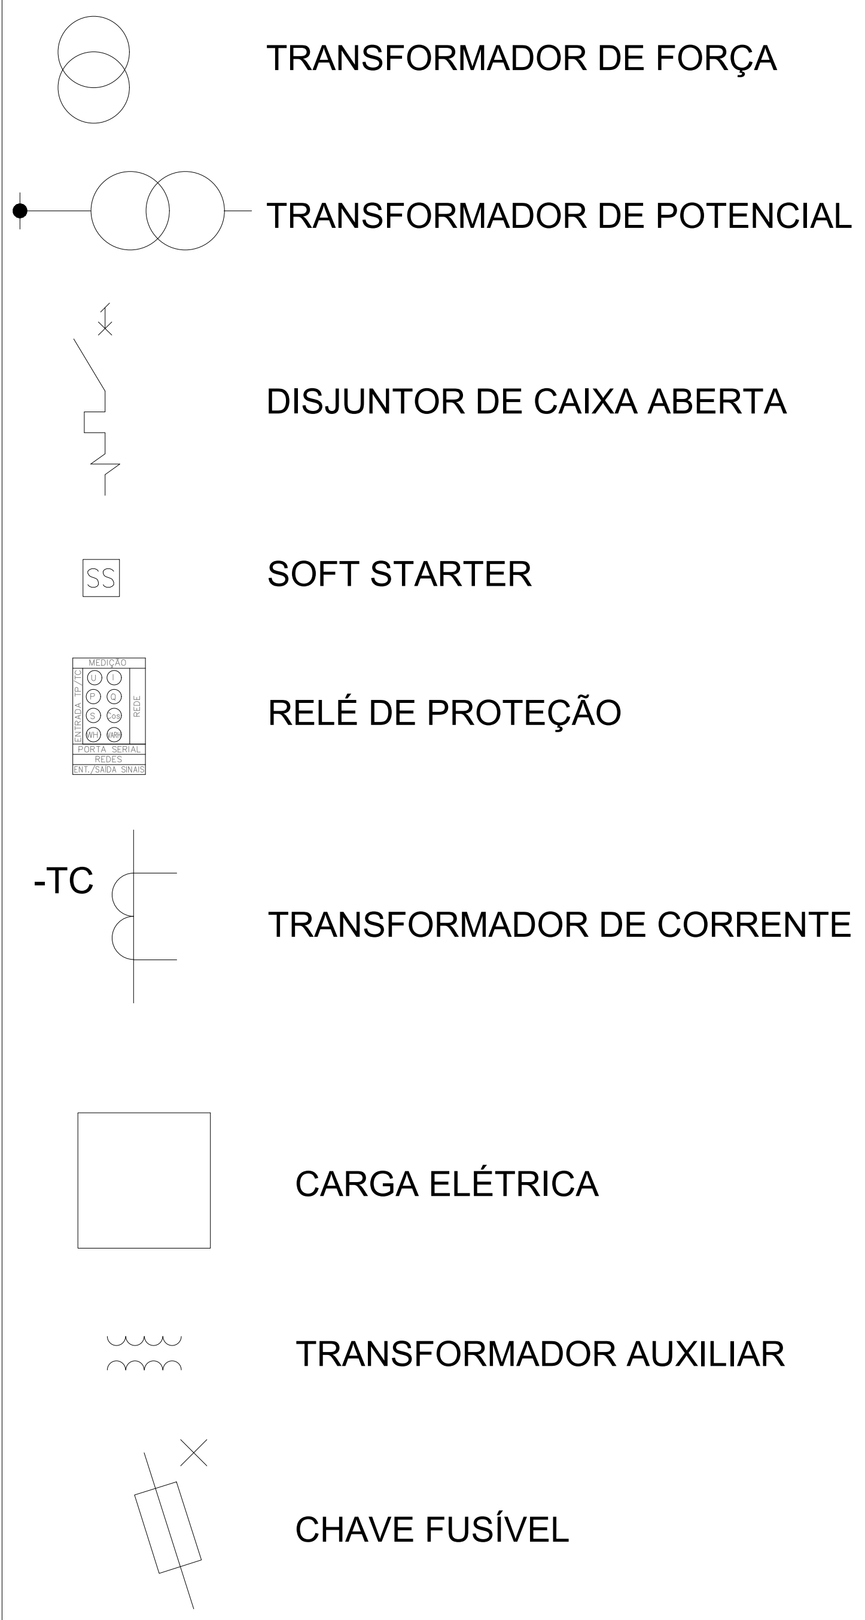

TRANSFORMADOR DE FORÇA
TRANSFORMADOR DE POTENCIAL
DISJUNTOR DE CAIXA ABERTA
SOFT STARTER
RELÉ DE PROTEÇÃO
TRANSFORMADOR DE CORRENTE
CARGA ELÉTRICA
TRANSFORMADOR AUXILIAR
CHAVE FUSÍVEL

NOTAS:

1- A CABINE DE ENTRADA, PROTEÇÃO E MEDIÇÃO DEVE SER DE ACORDO COM A NORMA DE DISTRIBUIÇÃO ND-5.3 DA CEMIG

Revisão	Data	Descrição	Elab.	Verif.	Aprov.	Aut.
2	24/03/26	Revisado Conforme Comentado	FS	LAT	ET	
1	19/02/26	Revisado Conforme Comentado	FS	LAT	ET	
0	15/12/25	Emissão Inicial	FS	LAT	ET	

FUNDO DE DESENVOLVIMENTO DA INFRAESTRUTURA
REGIONAL SUSTENTÁVEL - FDIRS

ESTRUTURAÇÃO DE PROJETO DE CONCESSÃO DO
PERÍMETRO IRRIGADO DO JAÍBA (ETAPAS 3 E 4)
ANTEPROJETO

DIAGRAMA UNFILAR
ESTAÇÃO DE RECALQUE ER3 - ETAPA 4

Finalidade de Emissão	▨ 1 Para Informação	2 Para Comentários	3 Para Aprovação	4 Para Execução	5 Como Construído	6 Para Utilização	7 Para Providências

Moysés & Pires ENGECORPS A&M Plena Consultoria e Projetos	Data: 19/02/26	Elaboração:	Verificação:
	Escala: S/E	Aprovação	Autorização
Referência: EGC006-EL3-0004		Revisão: 1	Desenho nº EGC006-EL2-0004