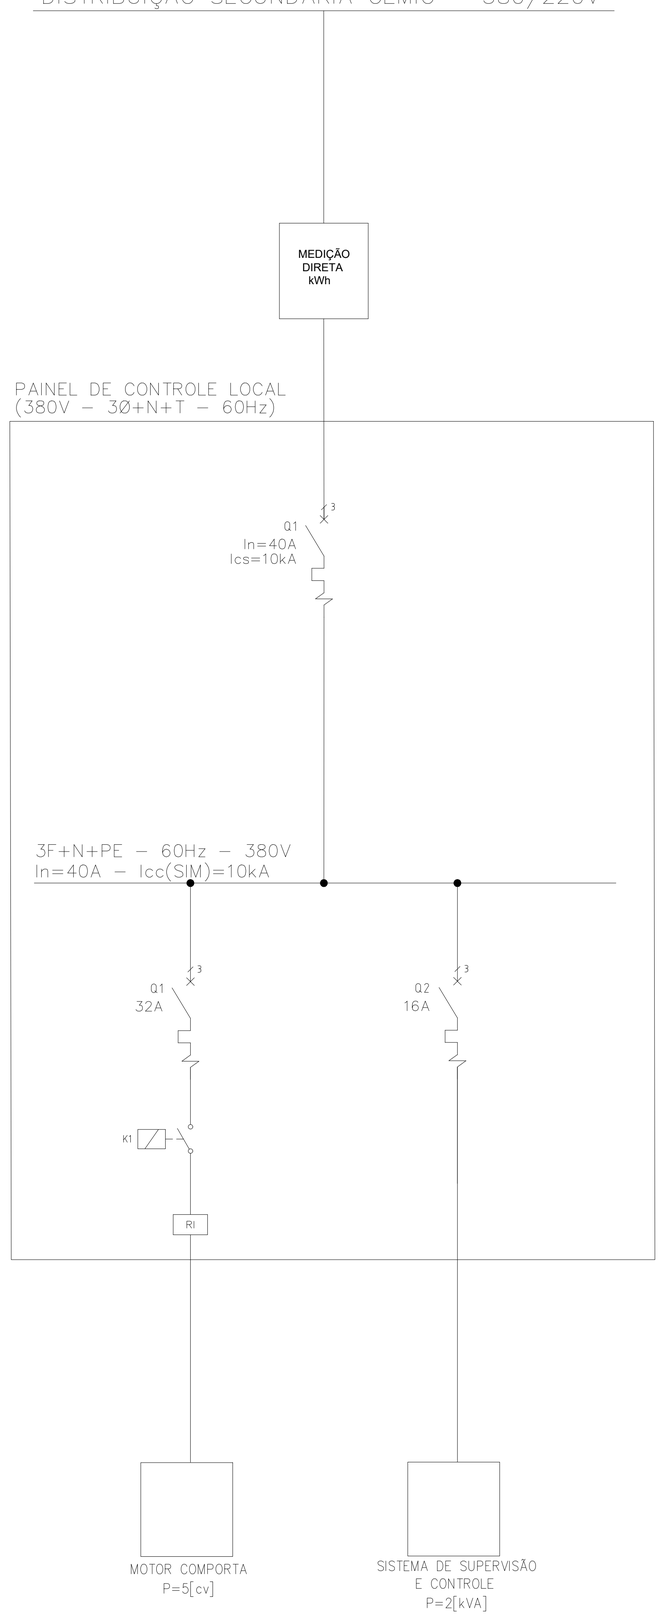


LEGENDA

DISJUNTOR DE CAIXA ABERTA

CONTATOR

MEDIÇÃO DIRETA kWh — CAIXA DE MEDIÇÃO DIRETA - PADRÃO CEMIG

RI — RELÉ TÉRMICO

CARGA ELÉTRICA

NOTAS:

1- O PAINEL DE MEDIÇÃO DEVE SER DE ACORDO COM A NORMA DE DISTRIBUIÇÃO ND-5.1 DA CEMIG

Revisão	Data	Descrição	Elab.	Verif.	Aprov.	Aut.
2	24/03/26	Revisado Conforme Comentado	FS	AG	ET	
1	19/02/26	Revisado Conforme Comentado	FS	AG	ET	
0	15/12/25	Emissão Inicial	FS	AG	ET	

FUNDO DE DESENVOLVIMENTO DA INFRAESTRUTURA REGIONAL SUSTENTÁVEL - FDIRS

ESTRUTURAÇÃO DE PROJETO DE CONCESSÃO DO PERÍMETRO IRRIGADO DO JAÍBA (ETAPAS 3 E 4)

ANTEPROJETO

DIAGRAMA UNFILAR GERAL

ESTAÇÃO DE RECALQUE ER3 - ETAPA 4

Finalidade de Emissão: Para Informação | 2 Para Comentários | 3 Para Aprovação | 4 Para Execução | 5 Como Construído | 6 Para Utilização | 7 Para Providências

MP Moysés & Pires; ENGECORPS; Plena Consultoria e Projetos

Data: 19/02/26 | Elaboração: | Verificação:

Escala: S/E | Aprovação | Autorização

Referência: EGC006-EL3-0006 | Revisão: 1 | Desenho nº EGC006-EL2-0006