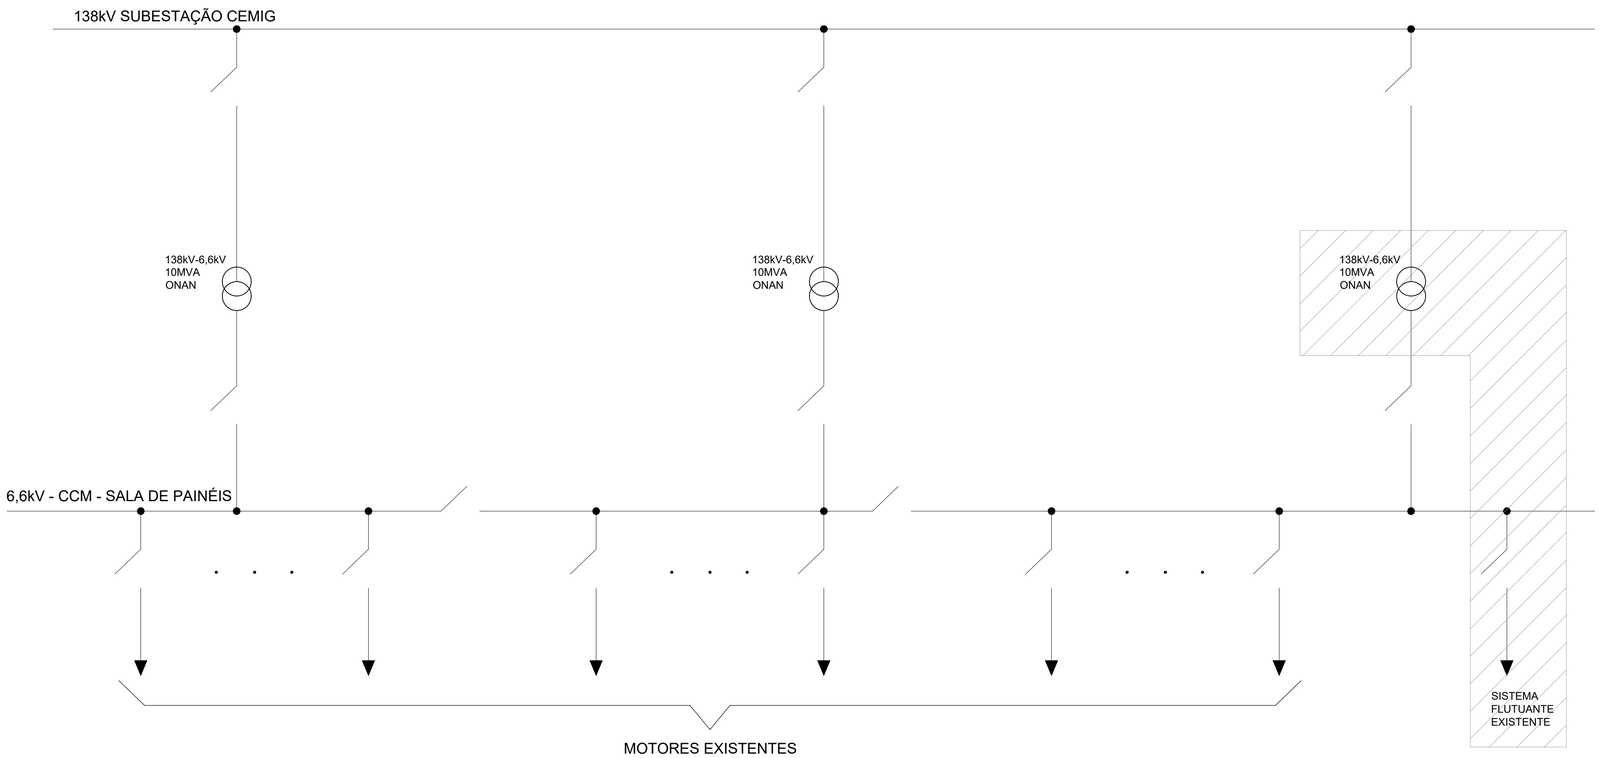



LEGENDA

TRANSFORMADOR DE FORÇA

DISJUNTOR

ALIMENTADOR

EQUIPAMENTOS A SEREM INSTALADOS

NOTAS:

1- EQUIPAMENTOS A SEREM INSTALADOS REPRESENTADOS EM HACHURA;

2- VALORES NOMINAIS DEVEM SER CONFIRMADOS EM ETAPAS POSTERIORES.

| Revisão | Data | Descrição | Elab. | Verif. | Aprov. | Aut. |
|---|---|---|---|---|---|---|
| | | | | | | |
| 2 | 24/03/26 | Revisado Conforme Comentado | MDCS | AG | ET | |
| 1 | 19/02/26 | Revisado Conforme Comentado | MDCS | AG | ET | |
| 0 | 16/12/25 | Emissão Inicial | MDCS | AG | ET | |

FUNDO DE DESENVOLVIMENTO DA INFRAESTRUTURA REGIONAL SUSTENTÁVEL - FDIRS

ESTRUTURAÇÃO DE PROJETO DE CONCESSÃO DO PERÍMETRO IRRIGADO DO JAÍBA (ETAPAS 3 E 4)

ANTEPROJETO

DIAGRAMA UNFILAR DE MÉDIA E BAIXA TENSÃO

ESTAÇÃO DE BOMBEAMENTO - EB1

| Finalidade de Emissão | Para Informação | 2 Para Comentários | 3 Para Aprovação | 4 Para Execução | 5 Como Construído | 6 Para Utilização | 7 Para Providências |
|---|---|---|---|---|---|---|---|

| | | | |
|---|---|---|---|
| Data: 19/02/26 | Elaboração: | | Verificação: |
| Escala: S/E | Aprovação | | Autorização |
| Referência: EGC006-EL3-1001 | Revisão: 1 | Desenho nº | EGC006-EL2-1001 |