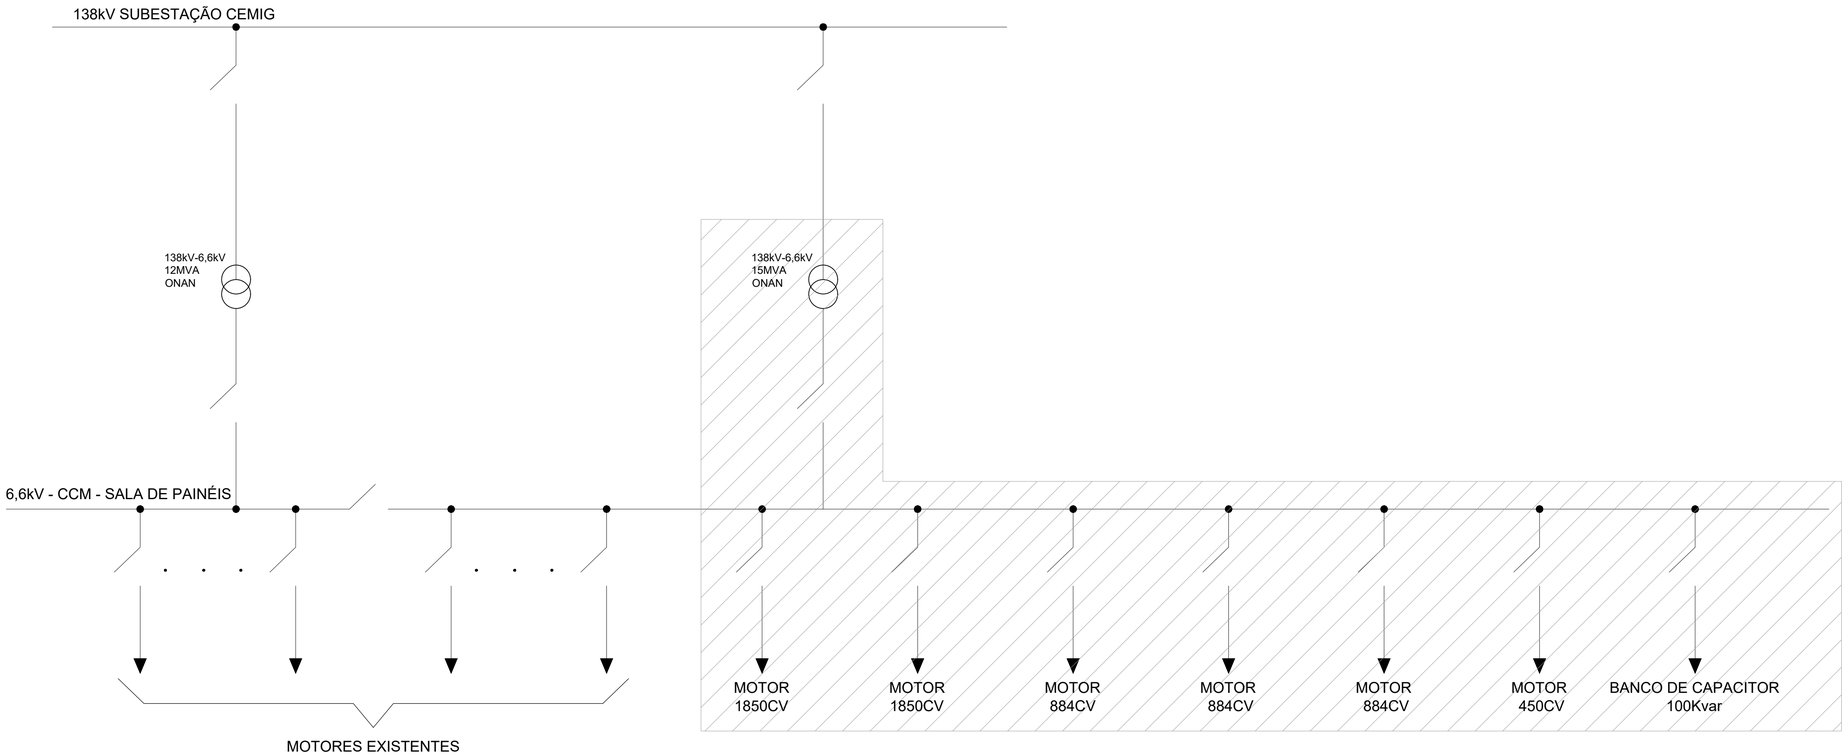


LEGENDA

TRANSFORMADOR DE FORÇA

DISJUNTOR

ALIMENTADOR

EQUIPAMENTOS A SEREM INSTALADOS

NOTAS:

1- EQUIPAMENTOS A SEREM INSTALADOS REPRESENTADOS EM HACHURA;

2- VALORES NOMINAIS DEVEM SER CONFIRMADOS EM ETAPAS POSTERIORES.

Revisão	Data	Descrição	Elab.	Verif.	Aprov.	Aut.
3	24/03/26	Revisado Conforme Comentado	MDCS	AG	ET	
2	26/02/26	Revisado Conforme Comentado	MDCS	AG	ET	
1	19/02/26	Revisado Conforme Comentado	MDCS	AG	ET	
0	16/12/25	Emissão Inicial	MDCS	AG	ET	

FUNDO DE DESENVOLVIMENTO DA INFRAESTRUTURA REGIONAL SUSTENTÁVEL - FDIRS

ESTRUTURAÇÃO DE PROJETO DE CONCESSÃO DO PERÍMETRO IRRIGADO DO JAÍBA (ETAPAS 3 E 4)

ANTEPROJETO

DIAGRAMA UNFILAR DE MÉDIA E BAIXA TENSÃO

ESTAÇÃO DE BOMBEAMENTO - EB2

Finalidade de Emissão	Para Informação	2 Para Comentários	3 Para Aprovação	4 Para Execução	5 Como Construído	6 Para Utilização	7 Para Providências

MP Moyses & Pires / ENGECORPS / MSM / Plena	Data: 26/02/26	Elaboração:	Verificação:
	Escala: S/E	Aprovação	Autorização
Referência: EGC006-EL3-1002	Revisão: 2	Desenho nº EGC006-EL2-1002	