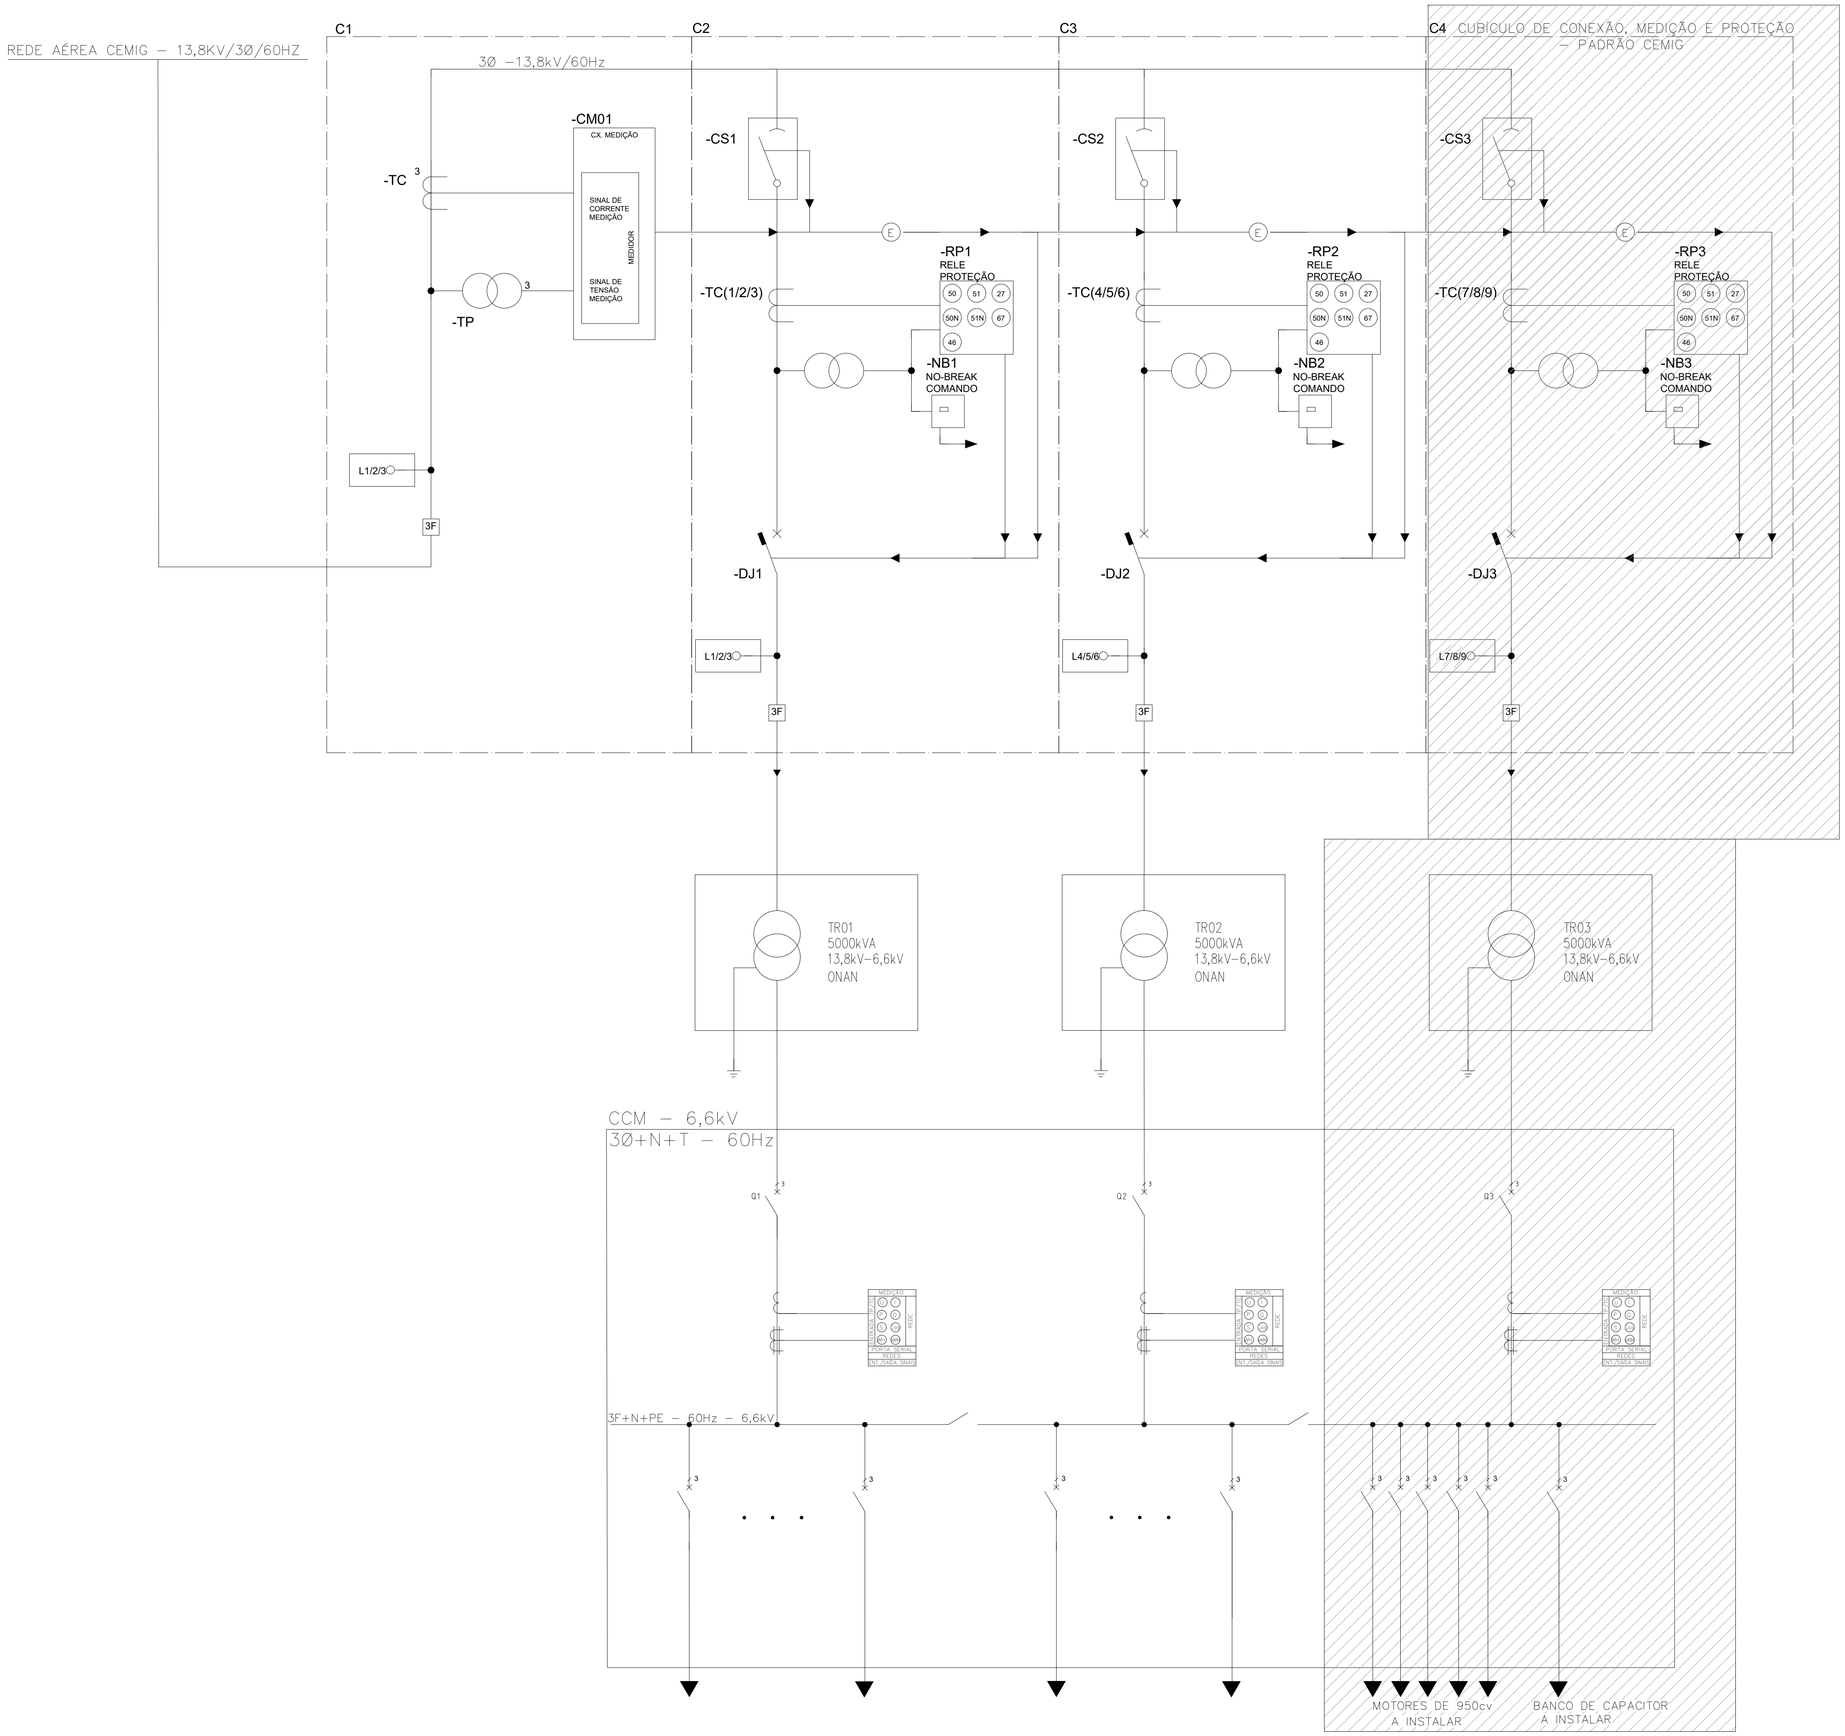


LEGENDA

- TRANSFORMADOR DE FORÇA
- SECCIONADOR
- DISJUNTOR DE CAIXA ABERTA
- SOFT STARTER
- RELÉ DE PROTEÇÃO
- -TC — TRANSFORMADOR DE CORRENTE
- -CM01 CX. MEDIÇÃO — CAIXA DE MEDIÇÃO COM MEDIDOR PADRÃO CEMIG
- TRANSFORMADOR DE POTENCIAL
- L1/2/3 — ISOLADOR
- NOBREAK
- CARGA ELÉTRICA
- TRANSFORMADOR AUXILIAR
- DISJUNTOR DE MÉDIA TENSÃO
- ALIMENTADOR
- EQUIPAMENTOS A SEREM INSTALADOS

NOTAS:

1- EQUIPAMENTOS A SEREM INSTALADOS REPRESENTADOS EM HACHURA;

2- VALORES NOMINAIS DEVEM SER CONFIRMADOS EM ETAPAS POSTERIORES.

Revisão	Data	Descrição	Elab.	Verif.	Aprov.	Aut.
3	24/03/26	Revisado Conforme Comentado	FS	AG	ET	
2	26/02/26	Revisado Conforme Comentado	FS	AG	ET	
1	19/02/26	Revisado Conforme Comentado	FS	AG	ET	
0	15/12/25	Emissão Inicial	FS	AG	ET	

FUNDO DE DESENVOLVIMENTO DA INFRAESTRUTURA REGIONAL SUSTENTÁVEL - FDIRS

ESTRUTURAÇÃO DE PROJETO DE CONCESSÃO DO PERÍMETRO IRRIGADO DO JAÍBA (ETAPAS 3 E 4)

ANTEPROJETO

DIAGRAMA UNFILAR DE MÉDIA E BAIXA TENSÃO
ESTAÇÃO DE BOMBEAMENTO - EB3

Finalidade de Emissão	Para Informação	2 Para Comentários	3 Para Aprovação	4 Para Execução	5 Como Construído	6 Para Utilização	7 Para Providências

MP Moyses & Pires / ENGECORPS / MA / Plena	Data: 26/02/26	Elaboração:	Verificação:
	Escala: S/E	Aprovação	Autorização
Referência: EGC006-EL3-1003	Revisão: 2	Desenho nº	EGC006-EL2-1003