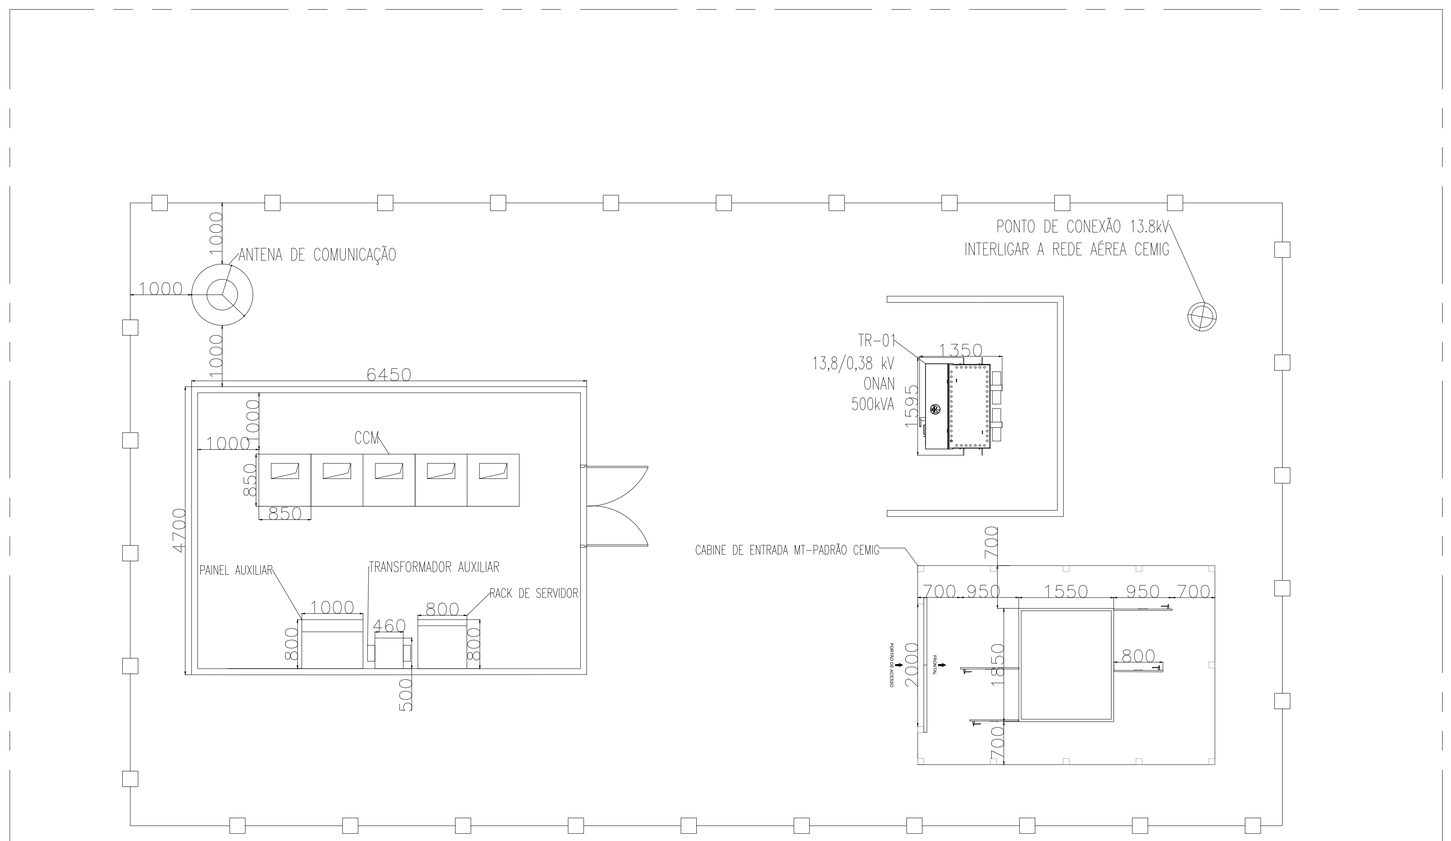


ARRANJO DE EQUIPAMENTOS – ER1

1:50

LEGENDA

- PAINEL AUXILIAR
- RACK DE SERVIDOR
- TRANSFORMADOR AUXILIAR
- CCM
- TRANSFORMADOR
- CABINE DE ENTRADA MT-PADRÃO CEMIG
- ANTENA DE COMUNICAÇÃO
- PONTO DE CONEXÃO

NOTAS

1– A CABINE DE ENTRADA, PROTEÇÃO E MEDIÇÃO DEVE SER DE ACORDO COM NORMA DE DISTRIBUIÇÃO ND–5.3 DA CEMIG.
2– COTAS EM MILÍMETROS, EXCETO ONDE INDICAÇÃO.

Revisão	Data	Descrição	Elab.	Verif.	Aprov.	Aut.
2	23/03/26	Revisado Conforme Comentado	RSS	AG	ET	
1	19/02/26	Revisado Conforme Comentado	RSS	AG	ET	
0	19/12/25	Emissão Inicial	RSS	AG	ET	

FUNDO DE DESENVOLVIMENTO DA INFRAESTRUTURA REGIONAL SUSTENTÁVEL - FDIRS

ESTRUTURAÇÃO DE PROJETO DE CONCESSÃO DO PERÍMETRO IRRIGADO DO JAÍBA (ETAPAS 3 E 4)

ANTEPROJETO

LAYOUT DE EQUIPAMENTOS

ESTAÇÃO DE RECALQUE ER1 - ETAPA 4

Finalidade de Emissão	1 Para Informação	2 Para Comentários	3 Para Aprovação	4 Para Execução	5 Como Construído	6 Para Utilização	7 Para Providências

Data: 19/12/2025	Elaboração:		Verificação:
Escala: H= 1:50 V= 1:50	Aprovação		Autorização
Referência: EGC006–EL2–0002	Revisão: 0	Desenho nº EGC006–EL3–0002	