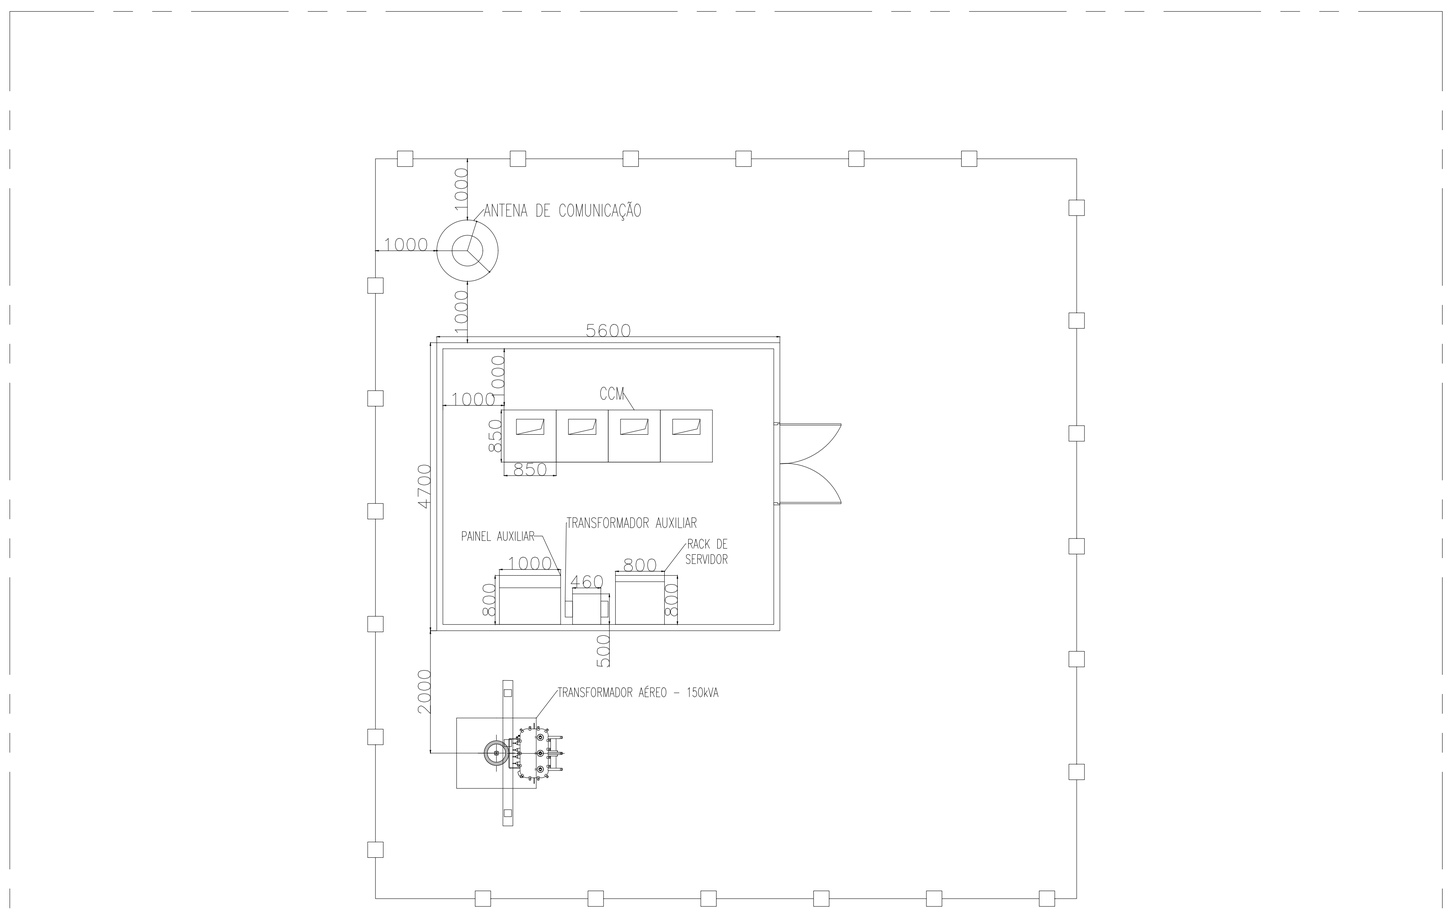


ARRANJO DE EQUIPAMENTOS – ER4

1:50

LEGENDA

PAINEL AUXILIAR

RACK DE SERVIDOR

TRANSFORMADOR AUXILIAR

CCM

TRANSFORMADOR AÉREO

ANTENA DE COMUNICAÇÃO

NOTAS

1– A CABINE DE ENTRADA, PROTEÇÃO E MEDIÇÃO DEVE SER DE ACORDO COM NORMA DE DISTRIBUIÇÃO ND–5.3 DA CEMIG.
2– COTAS EM MILIMETROS, EXCETO ONDE INDICAÇÃO.

Revisão	Data	Descrição	Elab.	Verif.	Aprov.	Aut.
2	23/03/26	Revisado Conforme Comentado	RSS	AG	ET	
1	19/02/26	Revisado Conforme Comentado	RSS	AG	ET	
0	19/12/25	Emissão Inicial	RSS	AG	ET	

FUNDO DE DESENVOLVIMENTO DA INFRAESTRUTURA REGIONAL SUSTENTÁVEL - FDIRS

ESTRUTURAÇÃO DE PROJETO DE CONCESSÃO DO PERÍMETRO IRRIGADO DO JAÍBA (ETAPAS 3 E 4)

ANTEPROJETO

LAYOUT DE EQUIPAMENTOS

ESTAÇÃO DE RECALQUE ER4 - ETAPA 4

Finalidade de Emissão	Para Informação	2 Para Comentários	3 Para Aprovação	4 Para Execução	5 Como Construído	6 Para Utilização	7 Para Providências

Moysés & Pires / ENGECORPS	Data: 19/12/2025	Elaboração:	Verificação:
	Escala: H= 1:50 V= 1:50	Aprovação	Autorização
Referência: EGC006–EL2–0005	Revisão: 0	Desenho nº	EGC006–EL3–0005