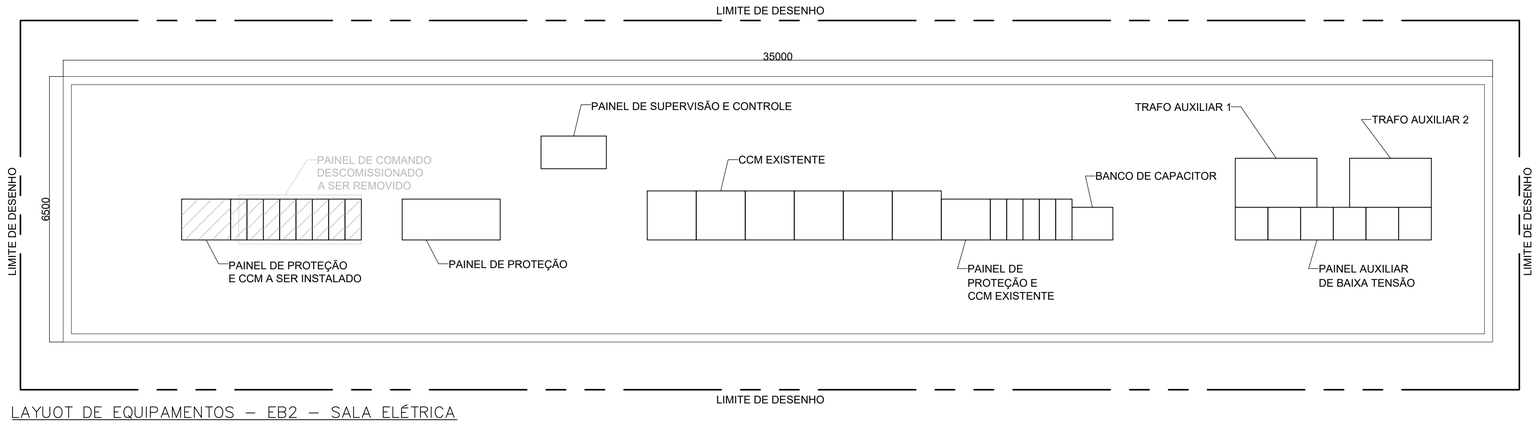


LAYUOT DE EQUIPAMENTOS – EB2 – SALA ELÉTRICA

1: 75

LEGENDA

EQUIPAMENTO EXISTENTE, CONFORME INDICAÇÃO

EQUIPAMENTO A SER INSTALADO, CONFORME INDICAÇÃO

EQUIPAMENTO A SER REMOVIDO, CONFORME INDICAÇÃO

NOTAS:

1- COTAS EM MILÍMETROS, EXCETO ONDE INDICAÇÃO.

Revisão	Data	Descrição	Elab.	Verif.	Aprov.	Aut.
1	23/03/26	Revisado Conforme Comentado	MDCS	AG	ET	
0	16/12/25	Emissão Inicial	MDCS	AG	ET	

FUNDO DE DESENVOLVIMENTO DA INFRAESTRUTURA REGIONAL SUSTENTÁVEL - FDIRS

ESTRUTURAÇÃO DE PROJETO DE CONCESSÃO DO PERÍMETRO IRRIGADO DO JAÍBA (ETAPAS 3 E 4)

ANTEPROJETO

LAYOUT DE EQUIPAMENTOS

ESTAÇÃO DE BOMBEAMENTO - EB2

Finalidade de Emissão	Para Informação	2 Para Comentários	3 Para Aprovação	4 Para Execução	5 Como Construído	6 Para Utilização	7 Para Providências

Moysés & Pires / Engecorps / Plena	Data: 23/03/26	Elaboração:	Verificação:
	Escala: S/E	Aprovação	Autorização
Referência: EGC006-EL2-1002	Revisão: 1	Desenho nº EGC006-EL3-1002	