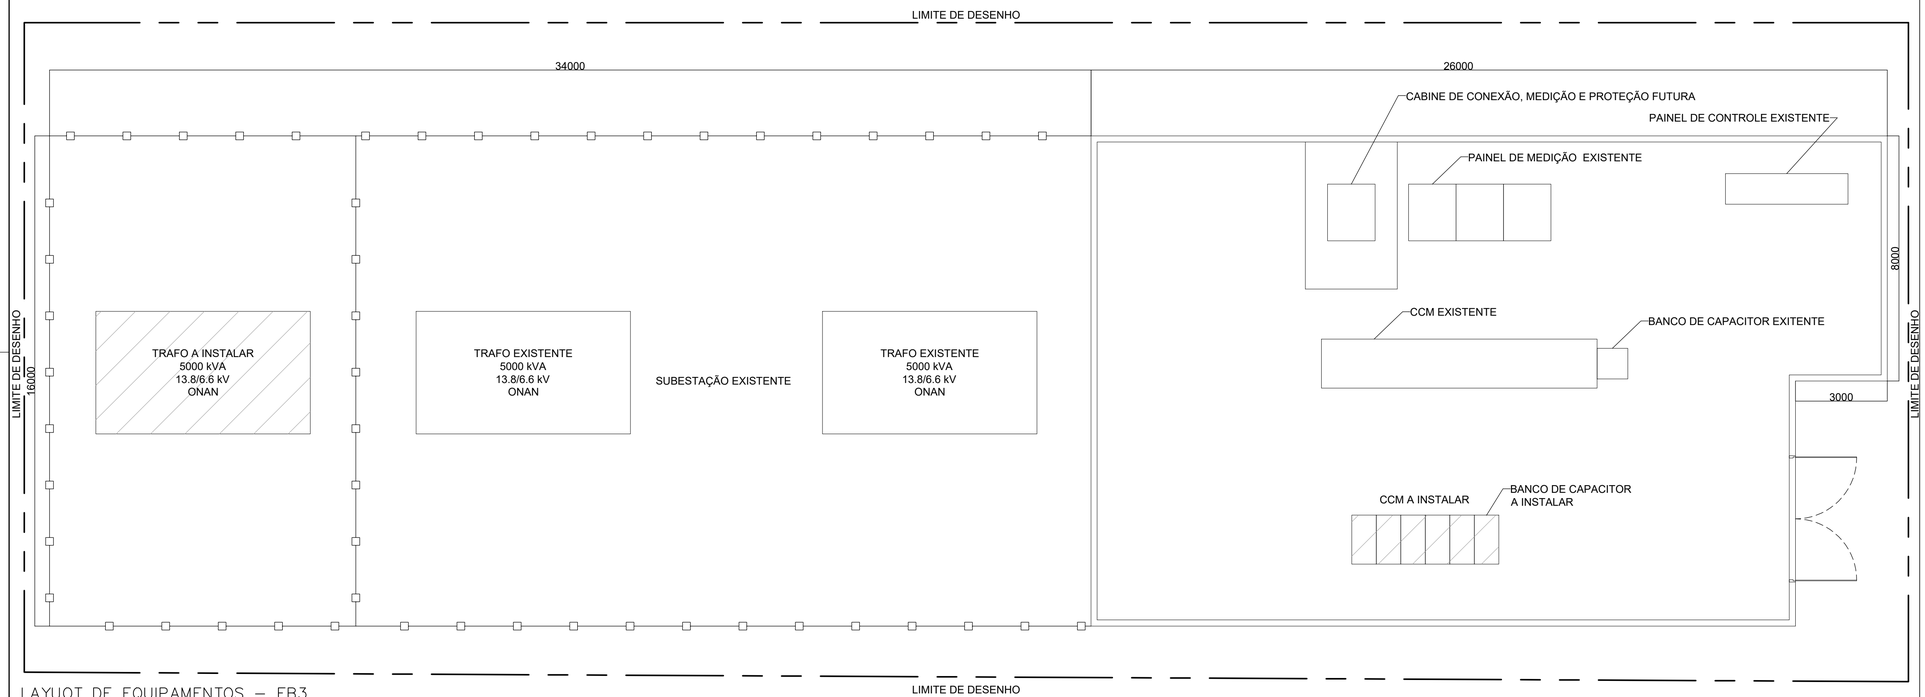


LAYUOT DE EQUIPAMENTOS – EB3

1:100

EQUIPAMENTO EXISTENTE, CONFORME INDICAÇÃO

EQUIPAMENTO A SER INSTALADO, CONFORME INDICAÇÃO

EQUIPAMENTO A SER REMOVIDO, CONFORME INDICAÇÃO

NOTAS:

1- A CABINE DE ENTRADA, PROTEÇÃO E MEDIÇÃO DEVE SER DE ACORDO COM A NORMA DE DISTRIBUIÇÃO ND-5.3 DA CEMIG.

2- COTAS EM MILÍMETROS, EXCETO ONDE INDICAÇÃO.

Revisão	Data	Descrição	Elab.	Verif.	Aprov.	Aut.
2	23/03/26	Revisado Conforme Comentado	MDCS	AG	ET	
1	26/02/26	Revisado Conforme Comentado	MDCS	AG	ET	
0	16/12/25	Emissão Inicial	MDCS	AG	ET	

FUNDO DE DESENVOLVIMENTO DA INFRAESTRUTURA REGIONAL SUSTENTÁVEL - FDIRS

ESTRUTURAÇÃO DE PROJETO DE CONCESSÃO DO PERÍMETRO IRRIGADO DO JAÍBA (ETAPAS 3 E 4)

ANTEPROJETO

LAYOUT DE EQUIPAMENTOS

ESTAÇÃO DE BOMBEAMENTO - EB3

Finalidade de Emissão	Para Informação	2 Para Comentários	3 Para Aprovação	4 Para Execução	5 Como Construído	6 Para Utilização	7 Para Providências

Data: 23/03/26	Elaboração:		Verificação:
Escala: S/E	Aprovação		Autorização
Referência: EGC006-EL2-1003	Revisão: 2	Desenho nº	EGC006-EL3-1003