
B13
B12
B11
B10
B9
B8
B7
B6
B5
B4
B3
B2
B1
B29
B28
B27
B30
B26
B24
B32
B25
B31
02
MG-401
JAÍBA
CANAL SECUNDÁRIO CS19
CANAL PRINCIPAL CP3
CANAL SECUNDÁRIO CS21
LMG-633
MOCAMBINHO
PONTE MG-401
POVOADO
COPASA
POSTO DE GASOLINA
E=630000
E=631000
E=632000
E=633000
E=634000
E=635000
E=636000
E=637000
E=640000
N=8331000
N=8330000
N=8329000
N=8328000
N=8327000
N=8326000
N=8325000
N=8324000
N=8323000
N=8322000
N=8321000
N=8320000
N=8319000
E=622000
E=623000
E=624000

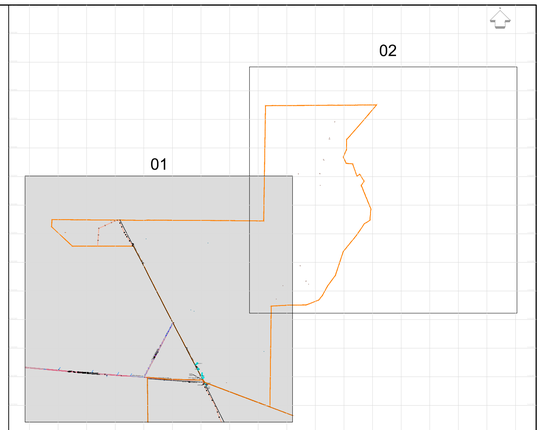

PLANTA CHAVE

LEGENDA:

- LIMITE - JAÍBA III
- LIMITE - JAÍBA IV
- RODOVIA ESTADUAL E MUNICIPAL
- LINHA DE TRANSMISSÃO
- TORRE DE TRASMISSÃO
- CURVA DE NÍVEL
- CEMIG
- POVOADO
- ÁREAS AMBIENTAIS SENSÍVEIS
- TOMADA D'ÁGUA
- ÁREA IRRIGÁVEL

NOTAS:

1 - MEDIDAS, COORDENADAS E ELEVAÇÕES EM METRO.
2 - DATUM HORIZONTAL SIRGAS2000 - FUSO 23 - MC -45º.
3 - DATUM VERTICAL: MODELO GEOIDE HGEOHNOR2020 – MARÉGRAFO IMBITUBA - SC
4 - A ÁREA IRRIGADA CORRESPONDE A 95% DA ÁREA IRRIGÁVEL

Revisão	Data	Descrição	Elab.	Verif.	Aprov.	Aut.
2	10/10/2025	Revisão do parcelamento das áreas irrigáveis	AHL	HKZ	EDK	
1	26/08/2025	Revisão do parcelamento das áreas irrigáveis	AHL	HKZ	EDK	
0	31/07/2025	Emissão Inicial	JOP	AHL	EDK	XXX

FUNDO DE DESENVOLVIMENTO DA INFRAESTRUTURA REGIONAL SUSTENTÁVEL - FDIRS

ESTRUTURAÇÃO DE PROJETO DE CONCESSÃO DO PERÍMETRO IRRIGADO DO JAÍBA (ETAPAS 3 E 4)

ANTEPROJETO

LAYOUT DOS CANAIS
ETAPA 3
FOLHA 01

Finalidade de Emissão	1 Para Informação	2 Para Comentários	Para Aprovação	4 Para Execução	5 Como Construído	6 Para Utilização	7 Para Provisências

Moysés & Pires Consultoria de Projetos | ENGECORPS Group | Plena Consultoria e Projetos

Data: 26/08/25
Escala: 1:30.000
Referência:

Elaboração:
Aprovação
Revisão: 02

Verificação:
Autorização
Desenho nº J3-DS-HI-0001-02