
Nº PROPRIEDADE	ÁREA PROPRIEDADE (ha)	COR DA HACHURA	CLASSIFICAÇÃO DE PROPRIEDADES RURAIS
1	984.9005	VERMELHA	Imóvel Geo
2	3.666.8488	VERMELHA	Imóvel Geo
22	33.6596	AZUL	Imóvel CAR
23	148.7249	AMARELA	Imóvel sem classificação
24	146.2072	AZUL	Imóvel CAR
25	45.4360	AZUL	Imóvel CAR
26	662.6401	AMARELA	Imóvel sem classificação
27	81.9726	VERMELHA	Imóvel Geo
28	244.4560	AMARELA	Imóvel sem classificação
29	40.6151	AZUL	Imóvel CAR
30	40.6763	AZUL	Imóvel CAR
31	82.7130	AMARELA	Imóvel sem classificação
32	44.6305	AZUL	Imóvel CAR
33	80.6445	AZUL	Imóvel CAR
34	1.369.7791	AZUL	Imóvel CAR
45	27.4102	AZUL	Imóvel CAR
46	29.8654	AZUL	Imóvel CAR
47	153.3306	VERMELHA	Imóvel Geo
48	10.8401	VERMELHA	Imóvel Geo
49	20.4532	VERMELHA	Imóvel Geo
50	41.5791	AZUL	Imóvel CAR
51	31.4109	AZUL	Imóvel CAR
52	10.6937	AZUL	Imóvel CAR
53	80.8567	AZUL	Imóvel CAR
54	80.3360	VERMELHA	Imóvel Geo
55	72.7901	AZUL	Imóvel CAR
56	80.0643	AZUL	Imóvel CAR
57	95.4150	AMARELA	Imóvel sem classificação
58	391.1983	AZUL	Imóvel CAR
81	25.1691	AZUL	Imóvel CAR
82	89.2603	AZUL	Imóvel CAR
83	152.2230	AZUL	Imóvel CAR
84	31.1133	AZUL	Imóvel CAR
85	87.2090	VERMELHA	Imóvel Geo
86	90.6854	AZUL	Imóvel CAR
87	200.2822	AZUL	Imóvel CAR
88	120.5979	VERMELHA	Imóvel Geo
89	119.6151	VERMELHA	Imóvel Geo
90	161.8665	AMARELA	Imóvel sem classificação
98	27.7056	AZUL	Imóvel CAR
99	29.4889	AZUL	Imóvel CAR
100	14.7906	AZUL	Imóvel CAR
101	30.4985	AZUL	Imóvel CAR
102	121.0981	VERMELHA	Imóvel Geo
103	40.1218	AZUL	Imóvel CAR
104	38.2898	AZUL	Imóvel CAR
105	40.4561	AZUL	Imóvel CAR
106	40.7744	AZUL	Imóvel CAR
119	26.8767	AZUL	Imóvel CAR
120	4.9630	AZUL	Imóvel CAR
121	900.6554	AMARELA	Imóvel sem classificação
122	20.1635	AZUL	Imóvel CAR
123	39.8408	AZUL	Imóvel CAR
124	208.9901	AMARELA	Imóvel sem classificação
125	34.1842	AZUL	Imóvel CAR
126	41.3657	AZUL	Imóvel CAR
127	3.1506	VERMELHA	Imóvel Geo
128	3.0386	VERMELHA	Imóvel Geo
129	3.0335	VERMELHA	Imóvel Geo
130	3.0335	VERMELHA	Imóvel Geo
131	3.0359	VERMELHA	Imóvel Geo
132	3.0394	VERMELHA	Imóvel Geo
133	3.7630	VERMELHA	Imóvel Geo
134	4.0575	VERMELHA	Imóvel Geo
135	30.0085	AZUL	Imóvel CAR
136	15.1668	AZUL	Imóvel CAR
137	14.7833	AZUL	Imóvel CAR
138	6.4332	AZUL	Imóvel CAR
139	4.0387	AZUL	Imóvel CAR
140	7.5719	AZUL	Imóvel CAR
141	21.7517	AZUL	Imóvel CAR
142	23.2483	AZUL	Imóvel CAR
143	30.2674	AMARELA	Imóvel sem classificação
144	39.9854	AZUL	Imóvel CAR
145	41.6166	AZUL	Imóvel CAR
146	41.8107	AZUL	Imóvel CAR
147	14.2777	AZUL	Imóvel CAR
148	26.2764	AZUL	Imóvel CAR
149	29.6490	AZUL	Imóvel CAR
150	7.1738	AZUL	Imóvel CAR
151	1.7000	AZUL	Imóvel CAR
152	19.6450	AMARELA	Imóvel sem classificação
153	91.2524	AZUL	Imóvel CAR
154	52.5253	AZUL	Imóvel CAR
155	39.4552	AZUL	Imóvel CAR
156	13.8786	AZUL	Imóvel CAR
157	19.9522	AZUL	Imóvel CAR
158	5.9687	AZUL	Imóvel CAR
159	37.0947	AZUL	Imóvel CAR
160	26.7111	AZUL	Imóvel CAR
161	28.8392	AZUL	Imóvel CAR
162	29.6821	AZUL	Imóvel CAR
163	40.8582	AZUL	Imóvel CAR
164	41.4657	AZUL	Imóvel CAR
165	44.2996	AZUL	Imóvel CAR
166	35.0276	AZUL	Imóvel CAR
167	53.9939	AZUL	Imóvel CAR
168	29.8450	AZUL	Imóvel CAR
169	22.3395	AZUL	Imóvel CAR
170	28.1286	AZUL	Imóvel CAR
171	29.8854	AZUL	Imóvel CAR
172	30.3468	VERMELHA	Imóvel Geo
173	28.8707	AZUL	Imóvel CAR
174	14.4316	AZUL	Imóvel CAR
175	36.4555	AZUL	Imóvel CAR
176	5.4395	VERMELHA	Imóvel Geo
177	4.7189	VERMELHA	Imóvel Geo
178	4.5763	VERMELHA	Imóvel Geo
179	7.4999	VERMELHA	Imóvel Geo
180	7.5367	VERMELHA	Imóvel Geo
181	15.0862	AZUL	Imóvel CAR
182	14.4487	AMARELA	Imóvel sem classificação
183	14.6791	AZUL	Imóvel CAR
184	14.4039	AZUL	Imóvel CAR
185	15.1466	AZUL	Imóvel CAR
186	41.2850	AZUL	Imóvel CAR
187	120.8132	VERMELHA	Imóvel Geo
188	39.8208	AZUL	Imóvel CAR
189	39.7826	AZUL	Imóvel CAR
190	17.8158	AMARELA	Imóvel sem classificação
191	82.0793	AZUL	Imóvel CAR
192	15.2960	AZUL	Imóvel CAR
193	4.4968	AMARELA	Imóvel sem classificação
194	9.4027	AZUL	Imóvel CAR
195	3.4919	AMARELA	Imóvel sem classificação
196	5.4931	AZUL	Imóvel CAR
197	15.0239	AZUL	Imóvel CAR
198	15.2457	AZUL	Imóvel CAR
199	14.8980	AZUL	Imóvel CAR
200	18.0679	AZUL	Imóvel CAR
201	29.6840	AZUL	Imóvel CAR
202	7.1397	AZUL	Imóvel CAR
203	22.8614	AZUL	Imóvel CAR
204	3.3426	AZUL	Imóvel CAR
205	3.3312	AMARELA	Imóvel sem classificação
206	3.3353	AZUL	Imóvel CAR
207	3.3387	AZUL	Imóvel CAR
208	3.3435	AZUL	Imóvel CAR
209	3.3482	AZUL	Imóvel CAR
210	29.8271	AZUL	Imóvel CAR
211	23.1768	AZUL	Imóvel CAR
212	5.2077	AMARELA	Imóvel sem classificação
213	29.9025	AZUL	Imóvel CAR
214	9.6923	AZUL	Imóvel CAR
215	5.4421	AZUL	Imóvel CAR
216	14.8457	AZUL	Imóvel CAR
217	14.6365	AZUL	Imóvel CAR
218	15.2442	AZUL	Imóvel CAR
219	446.7896	VERMELHA	Imóvel Geo
220	26.3752	AZUL	Imóvel CAR
221	24.2413	AZUL	Imóvel CAR
222	30.0175	VERMELHA	Imóvel Geo
223	2.0059	AZUL	Imóvel CAR
224	28.2722	AMARELA	Imóvel sem classificação
225	79.2390	AZUL	Imóvel CAR
226	45.2706	AZUL	Imóvel CAR
227	29.8787	AZUL	Imóvel CAR
228	30.7579	AZUL	Imóvel CAR
229	19.9683	AZUL	Imóvel CAR
230	20.3157	AZUL	Imóvel CAR
231	13.8300	AZUL	Imóvel CAR
232	726.6007	AMARELA	Imóvel sem classificação
233	18.4633	AZUL	Imóvel CAR
234	495.4806	VERMELHA	Imóvel Geo
235	4.5377	VERMELHA	Imóvel Geo
236	127.1757	VERMELHA	Imóvel Geo
237	12.6308	AMARELA	Imóvel sem classificação
238	116.5786	VERMELHA	Imóvel Geo
239	111.2788	VERMELHA	Imóvel Geo
240	79.0966	AZUL	Imóvel CAR
241	503.0976	VERMELHA	Imóvel Geo
242	919.8851	AZUL	Imóvel CAR
243	90.1451	AZUL	Imóvel CAR
244	50.4584	AMARELA	Imóvel sem classificação
245	218.5561	VERMELHA	Imóvel Geo
246	34.8375	VERMELHA	Imóvel Geo
247	32.4039	AZUL	Imóvel CAR
248	31.7993	AMARELA	Imóvel sem classificação
249	30.8373	AZUL	Imóvel CAR
250	32.1537	AMARELA	Imóvel sem classificação
251	220.2688	VERMELHA	Imóvel Geo
252	560.0018	VERMELHA	Imóvel Geo
253	239.9770	VERMELHA	Imóvel Geo
254	153.4442	VERMELHA	Imóvel Geo
255	85.5712	VERMELHA	Imóvel Geo
256	82.7171	AZUL	Imóvel CAR
257	88.3471	AMARELA	Imóvel sem classificação
258	91.6730	AMARELA	Imóvel sem classificação
259	92.3735	AZUL	Imóvel CAR
260	9.4615	AMARELA	Imóvel sem classificação
261	21.1695	AZUL	Imóvel CAR
262	645.7153	VERMELHA	Imóvel Geo
263	225.8064	VERMELHA	Imóvel Geo
264	57.7377	VERMELHA	Imóvel Geo
265	30.4657	VERMELHA	Imóvel Geo
266	36.0299	AZUL	Imóvel CAR
267	75.0016	VERMELHA	Imóvel Geo
268	74.6117	VERMELHA	Imóvel Geo
269	62.0123	AZUL	Imóvel CAR
270	90.1858	AMARELA	Imóvel sem classificação
271	6.0180	AZUL	Imóvel CAR
272	19.4678	AZUL	Imóvel CAR
273	56.3922	AZUL	Imóvel CAR
274	16.1812	AMARELA	Imóvel sem classificação
275	9.9215	AZUL	Imóvel CAR
276	70.5961	AZUL	Imóvel CAR
277	21.5153	AMARELA	Imóvel sem classificação
278	80.3896	AMARELA	Imóvel sem classificação
279	25.9485	AZUL	Imóvel CAR
280	54.4940	AMARELA	Imóvel sem classificação
281	14.3022	AMARELA	Imóvel sem classificação
TOTAL	26.397,9571		

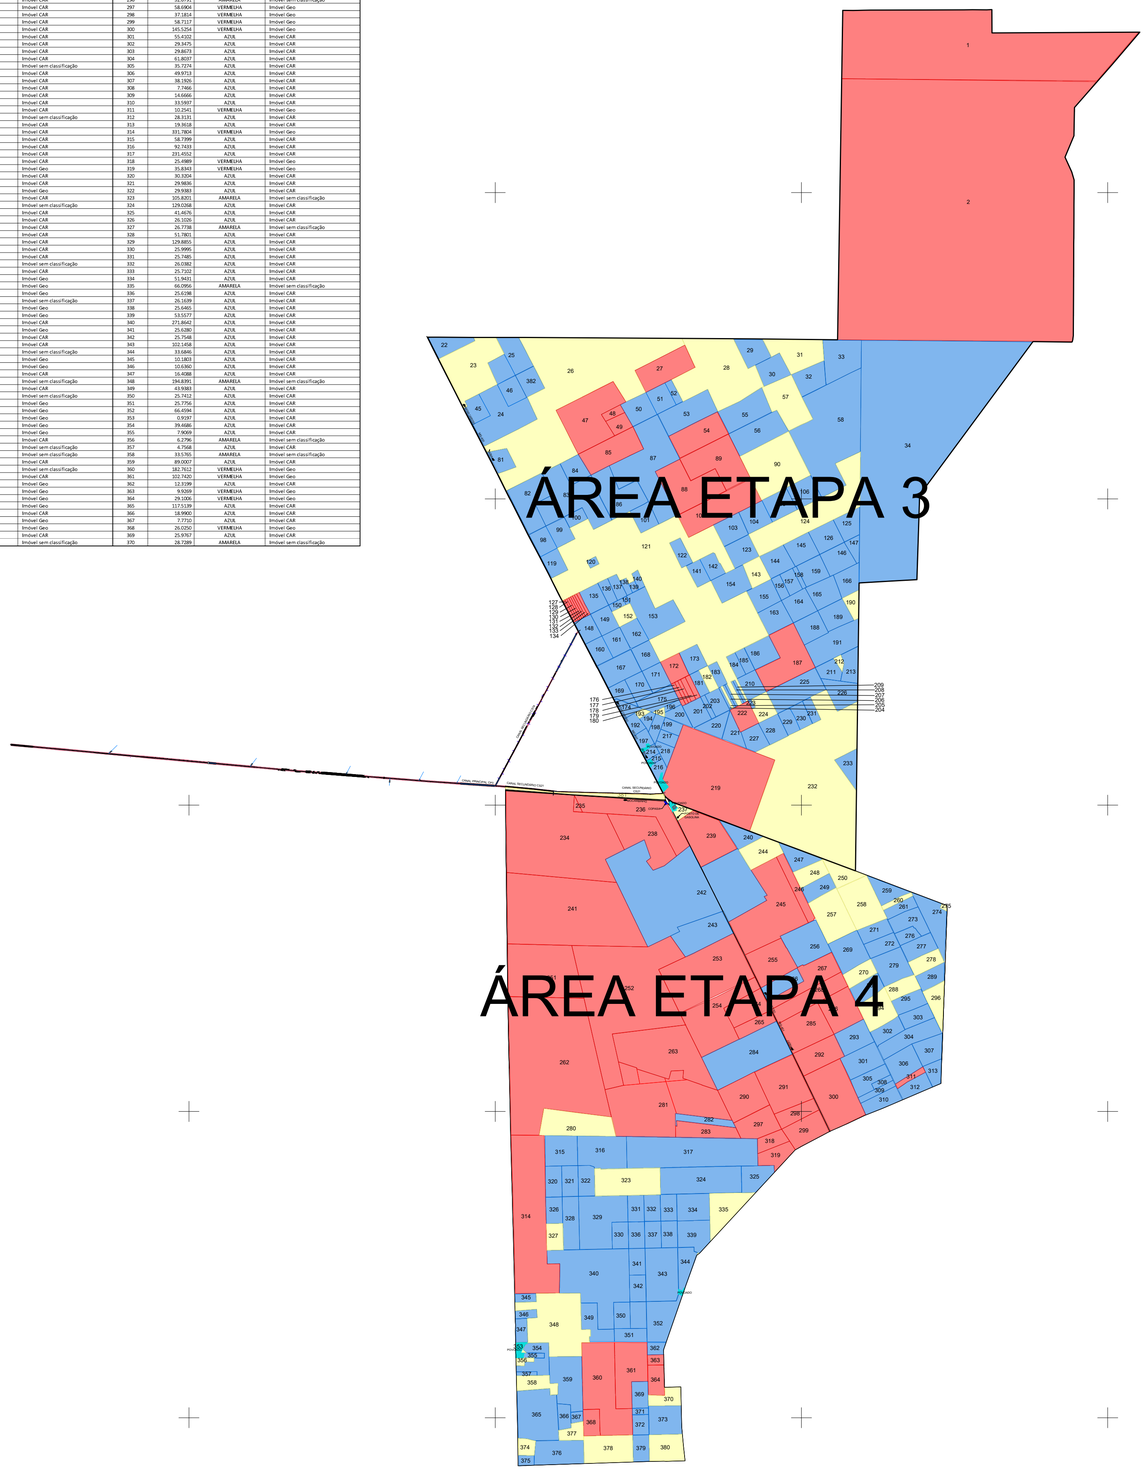

NOTAS:

1 - MEDIDAS, COORDENADAS E ELEVAÇÕES EM METRO.
2 - DATUM HORIZONTAL SIRGAS2000 - FUSO 23 - MC -45º.
3 - DATUM VERTICAL: MODELO GEOIDE HGEOHNOR2020 – MARÉGRAFO IMBITUBA - SC

LEGENDA:

- RODOVIA ESTADUAL E MUNICIPAL
- LIMITE POVOADO
- ÁREA COPASA
- CANAL — CANAL DE IRRIGAÇÃO (CP3 E CS21)
- IMÓVEL RURAL GEORREFERENCIADO SIGEF/INCRA: 11.982,9855 ha
- IMÓVEL RURAL COM CAR (SICAR) : 9.799,2777 ha
- IMÓVEL RURAL SEM REFERÊNCIA : 4.615,6939 ha

ÁREA TOTAL DOS IMÓVEIS RURAIS : 26.397,9571 ha

ÁREA TOTAL - ETAPA 3 e 4 : 26.652,0640 ha

OBS.:

1. Da área total das etapas 3 e 4 (26.652,0640 ha), 254,1069 ha não entraram na classificação de imóveis por se tratar de áreas pertencentes a:

   Infraestrutura de canais de irrigação = 9,4211 ha;
   Rodovia MG-401 = 54,2042 ha;
   Rodovia LMG-633 = 14,3306 ha;
   Estradas de acesso local = 176,1510 ha.

2. Fonte dos dados dos cadastros de imóveis rurais:

- CAR (Cadastro Ambiental Rural): Plataforma eletrônica SICAR (Sistema Nacional de Cadastro Ambiental Rural) endereço eletrônico https://consultapublica.car.gov.br/publico/estados/downloads - data: 26/08/2025.
- Georreferenciamento de Imóveis Rurais: Plataforma eletrônica SIGEF (Sistema de Gestão Fundiária) endereço eletrônico https://sigef.incra.gov.br/consultar/parcelas - data: 26/08/2025.

ÁREA TOTAL: 26.652,0640 ha

ÁREA ETAPA 3: 15.098,6408 ha

ÁREA ETAPA 4: 11.553,4232 ha

Revisão	Data	Descrição	Elab.	Verif.	Aprov.	Aut.
0	XX/XX	Emissão Inicial	XXX	XXX	XXX	XXX

FUNDO DE DESENVOLVIMENTO DA INFRAESTRUTURA REGIONAL SUSTENTÁVEL - FDIRS

ESTRUTURAÇÃO DE PROJETO DE CONCESSÃO DO PERÍMETRO IRRIGADO DO JAÍBA (ETAPAS 3 E 4)

ANTEPROJETO

TOPOGRAFIA - VETORIZAÇÃO DE PROPRIEDADES PELO GEORREFERENCIAMENTO E CADASTRO AMBIENTAL RURAL (CAR)

Finalidade de Emissão: [1] Para Informação | [2] Para Comentários | [3] Para Aprovação | [4] Para Execução | [5] Como Construído | [6] Para Utilização | [7] Para Providências

Data: 07/2026	Elaboração:	Verificação:	
Escala: H= 1:75.000	Aprovação XXX / XXX	Autorização XXX / XXX	
Referência:	Revisão: R2	Desenho nº JB-E3-4.04.TOP.DE.002	