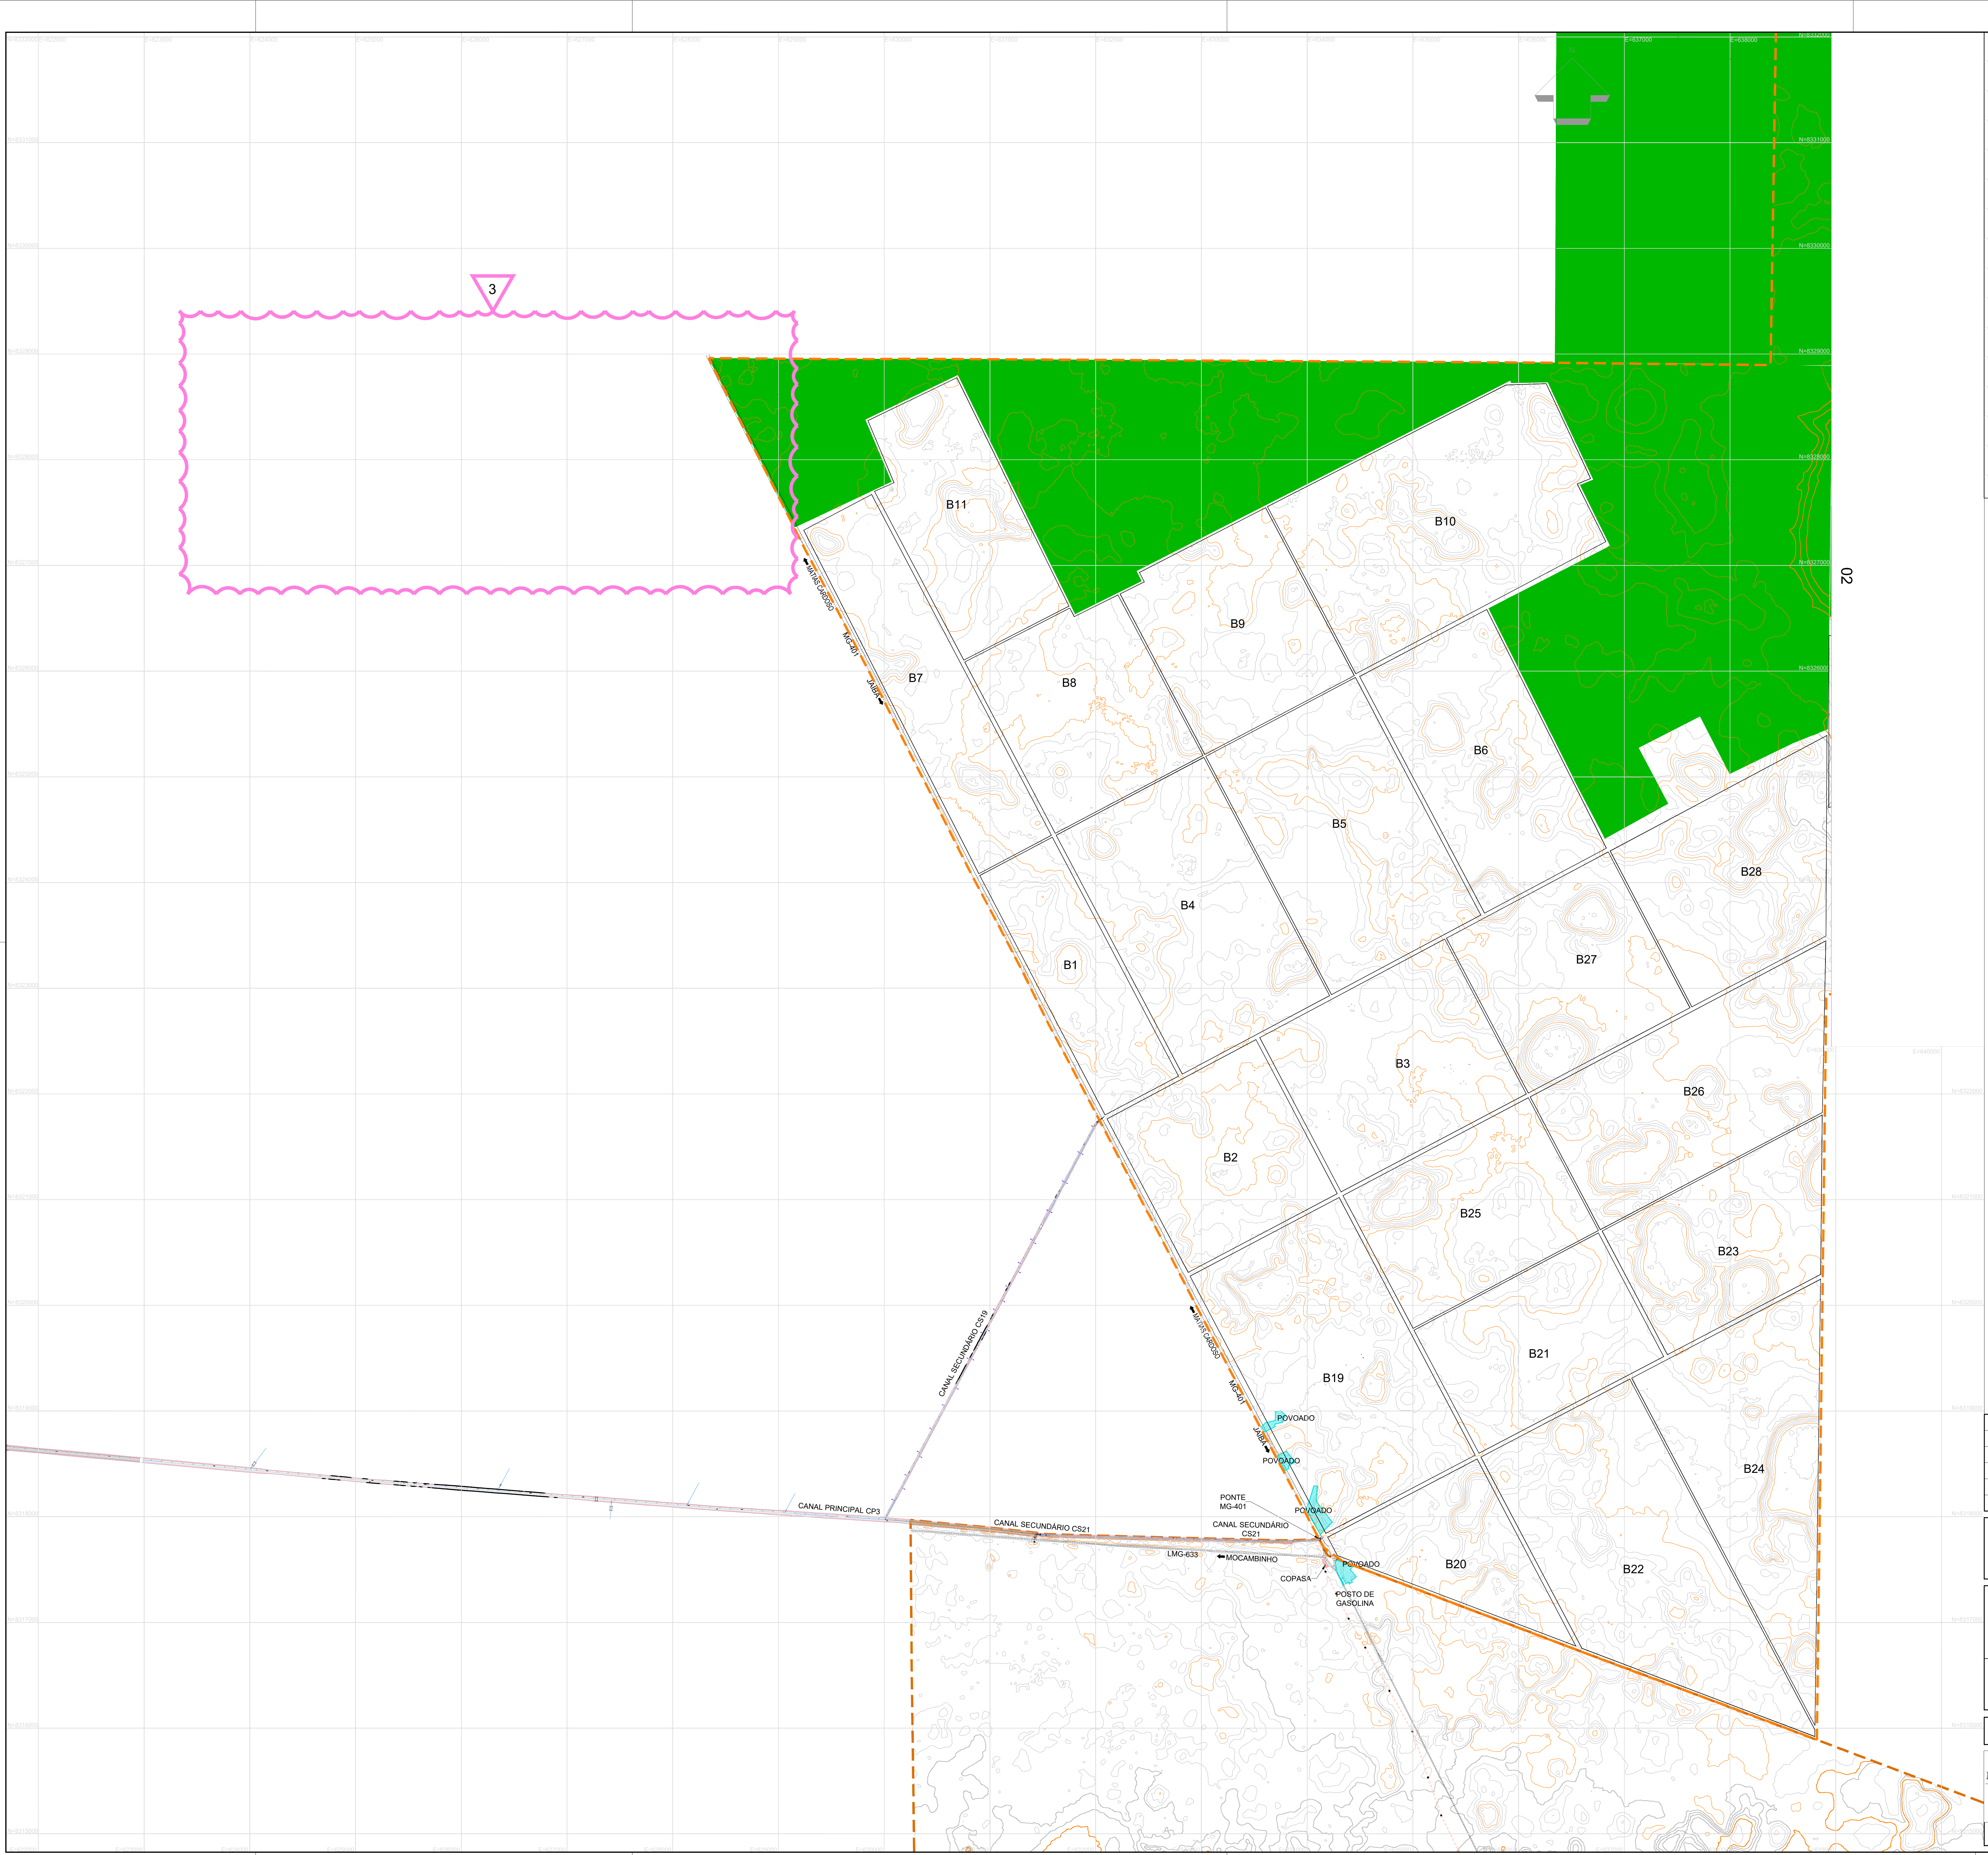
3
B11
B10
B9
B7
B8
B6
B5
B4
B28
B1
B27
B3
B26
B2
B25
B23
B21
B19
B24
B20
B22
02
MG-401
JAÍBA
CANAL SECUNDÁRIO CS19
CANAL PRINCIPAL CP3
CANAL SECUNDÁRIO CS21
PONTE MG-401
CANAL SECUNDÁRIO CS21
LMG-633
MOCAMBINHO
COPASA
POSTO DE GASOLINA
POVOADO
POVOADO
POVOADO
POVOADO

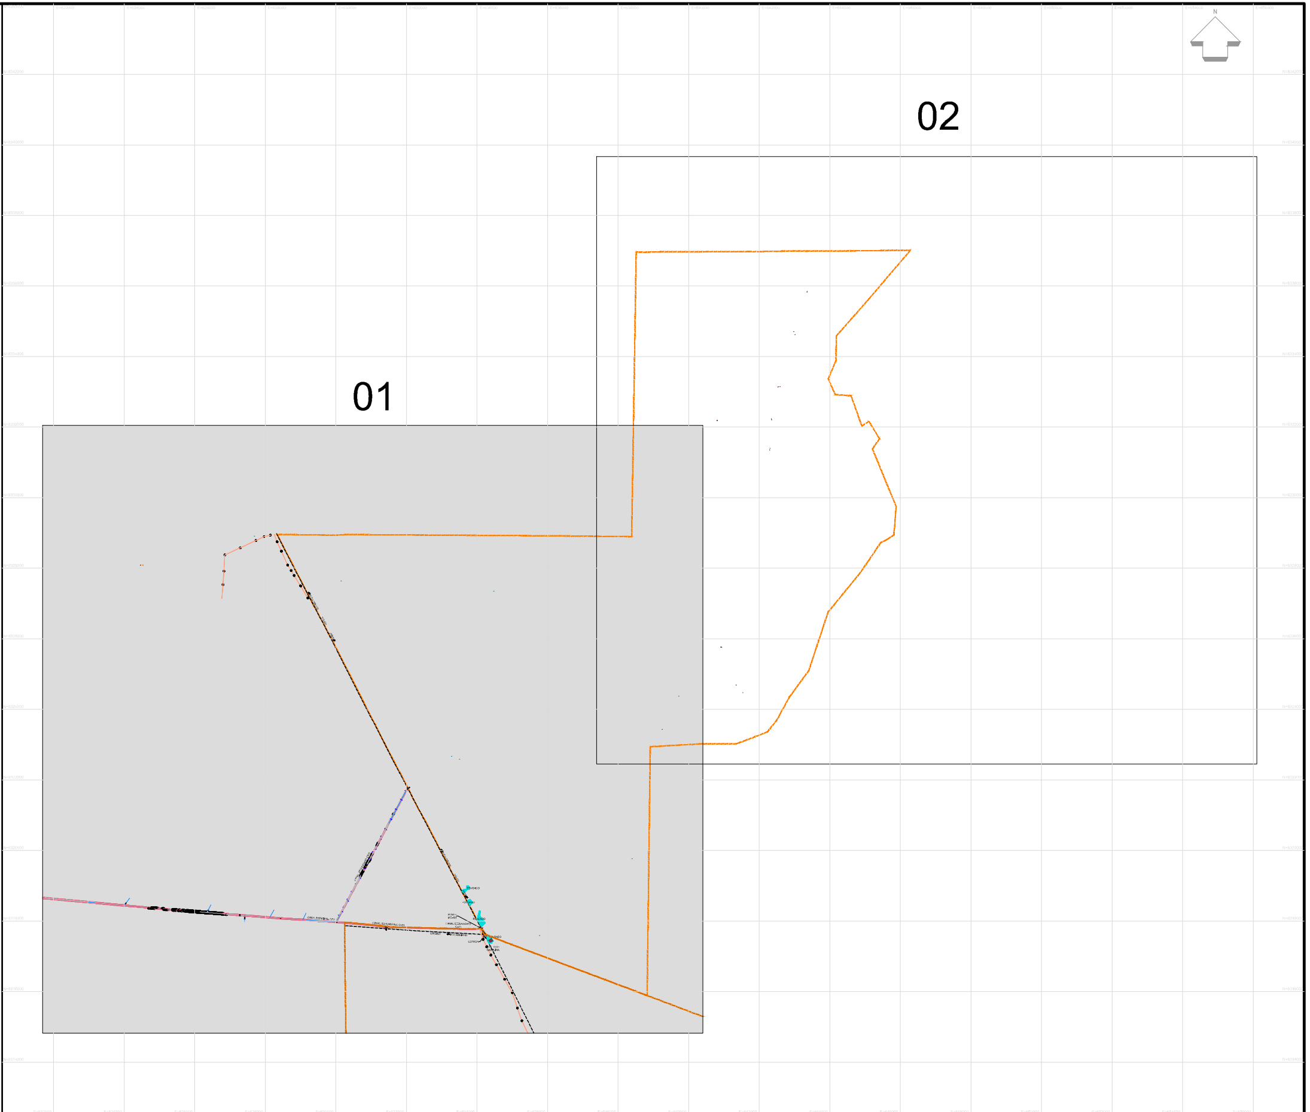

PLANTA CHAVE

LEGENDA:

- - -	LIMITE - JAÍBA III
- - -	LIMITE - JAÍBA IV
═	RODOVIA ESTADUAL E MUNICIPAL
┈	LINHA DE TRANSMISSÃO
⊠	TORRE DE TRASMISSÃO
☐	CURVA DE NÍVEL
▨	CEMIG
▨	POVOADO
🟩	ÁREAS AMBIENTAIS SENSÍVEIS
☐	ÁREA IRRIGÁVEL
▽ x	IDENTIFICAÇÃO DA REVISÃO

NOTAS:

1 - MEDIDAS, COORDENADAS E ELEVAÇÕES EM METRO.
2 - DATUM HORIZONTAL SIRGAS2000 - FUSO 23 - MC -45º.
3 - DATUM VERTICAL: MODELO GEOIDE HGEOHNOR2020 – MARÉGRAFO IMBITUBA - SC

REVISÕES:

REVISÃO 3 - REVISÃO DO PERÍMETRO IRRIGÁVEL DA ETAPA 3, CONFORME SOLICITAÇÕES FEITAS APÓS CONSULTA PÚBLICA

Revisão	Data	Descrição	Elab.	Verif.	Aprov.	Aut.
3	01/07/2026	Revisão do perímetro de irrigação da Etapa 3	AHL	HKZ	EDK	
2	10/10/2025	Revisão do parcelamento das áreas irrigáveis	AHL	HKZ	EDK	
1	26/08/2025	Revisão do parcelamento das áreas irrigáveis	AHL	HKZ	EDK	
0	31/07/2025	Emissão Inicial	JOP	AHL	EDK	

FUNDO DE DESENVOLVIMENTO DA INFRAESTRUTURA
REGIONAL SUSTENTÁVEL - FDIRS

ESTRUTURAÇÃO DE PROJETO DE CONCESSÃO DO
PERÍMETRO IRRIGADO DO JAÍBA (ETAPAS 3 E 4)

ANTEPROJETO

IDENTIFICAÇÃO DAS ÁREAS IRRIGÁVEIS
ETAPA 3
FOLHA 01

Finalidade de Emissão	☐ 1 Para Informação	☐ 2 Para Comentários	☒ 3 Para Aprovação	☐ 4 Para Execução	☐ 5 Como Construído	☐ 6 Para Utilização	☐ 7 Para Providências

Moysés & Pires – Sociedade de advogados; ENGECORPS GrupoTYPSA; A&M; Plena Consultoria e Projetos	Data: 01/07/26	Elaboração:	Verificação:
	Escala: 1:30.000	Aprovação	Autorização
Referência:		Revisão: 03	Desenho nº J3-DS-GR-0001-03