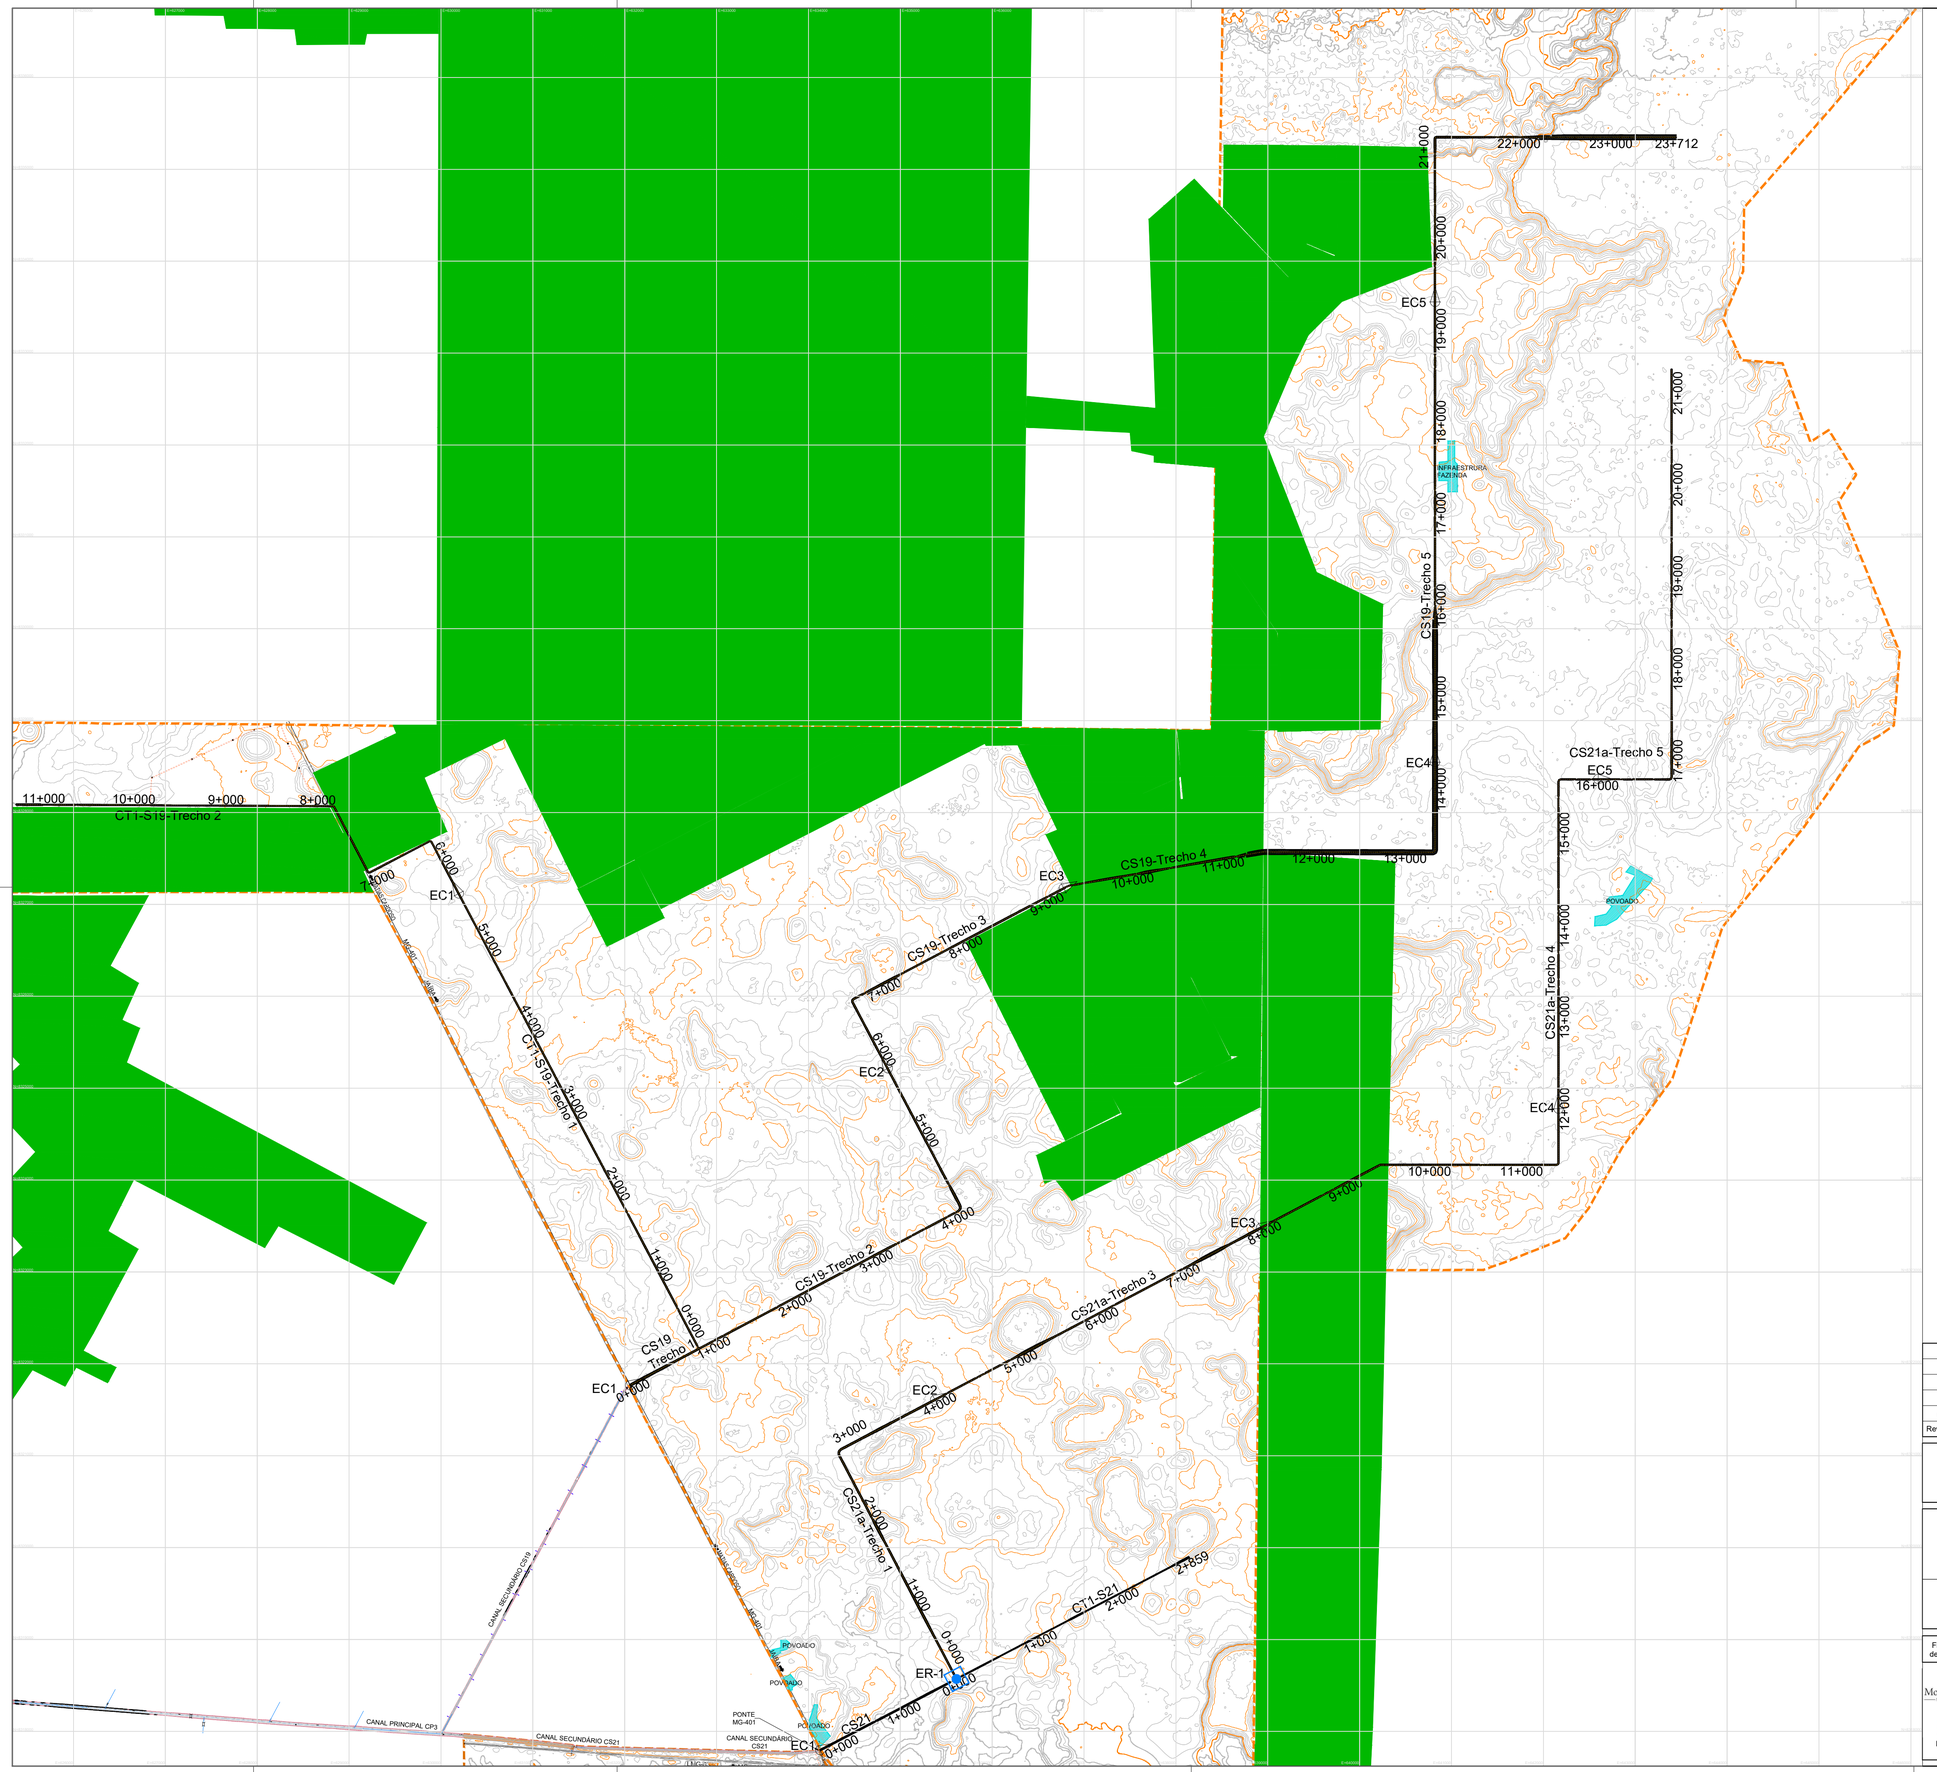


LEGENDA:

- LIMITE - JAÍBA III
- CANAL ADUTOR
- ÁREAS AMBIENTAIS SENSÍVEIS
- ELEVATÓRIA DE RECALQUE (ER-1)
- ESTAÇÃO DE CONTROLE (EC)

NOTAS:

1 - ÁREA IRRIGADA DOS LOTES EM HECTARES (93% ÁREA BRUTA IRRIGÁVEL);
2 - MEDIDAS EM METRO, EXCETO INDICAÇÃO CONTRÁRIA;
3 - ESTAQUEMANTO INDICADO EM km.

Revisão	Data	Descrição	Elab.	Verif.	Aprov.	Aut.
0	19/09/2025	Emissão Inicial	AHL	HKO	EDK	

FUNDO DE DESENVOLVIMENTO DA INFRAESTRUTURA REGIONAL SUSTENTÁVEL - FDIRS

ESTRUTURAÇÃO DE PROJETO DE CONCESSÃO DO PERÍMETRO IRRIGADO DO JAÍBA (ETAPAS 3 E 4)

ANTEPROJETO

ALTERNATIVA 1 - SISTEMA ADUTOR POR CANAIS

ETAPA 3

Finalidade de Emissão	1 Para Informação	2 Para Comentários	Para Aprovação	4 Para Execução	5 Como Construído	6 Para Utilização	7 Para Providências

Moyses & Pires Consultoria | ENGECORPS Group | Plena Consultoria e Projetos

Data: 29/08/25 | Elaboração: | Verificação:

Escala: sem escala | Aprovação | Autorização

Referência:

Revisão: 00 | Desenho nº J3-DS-HI-0004-00