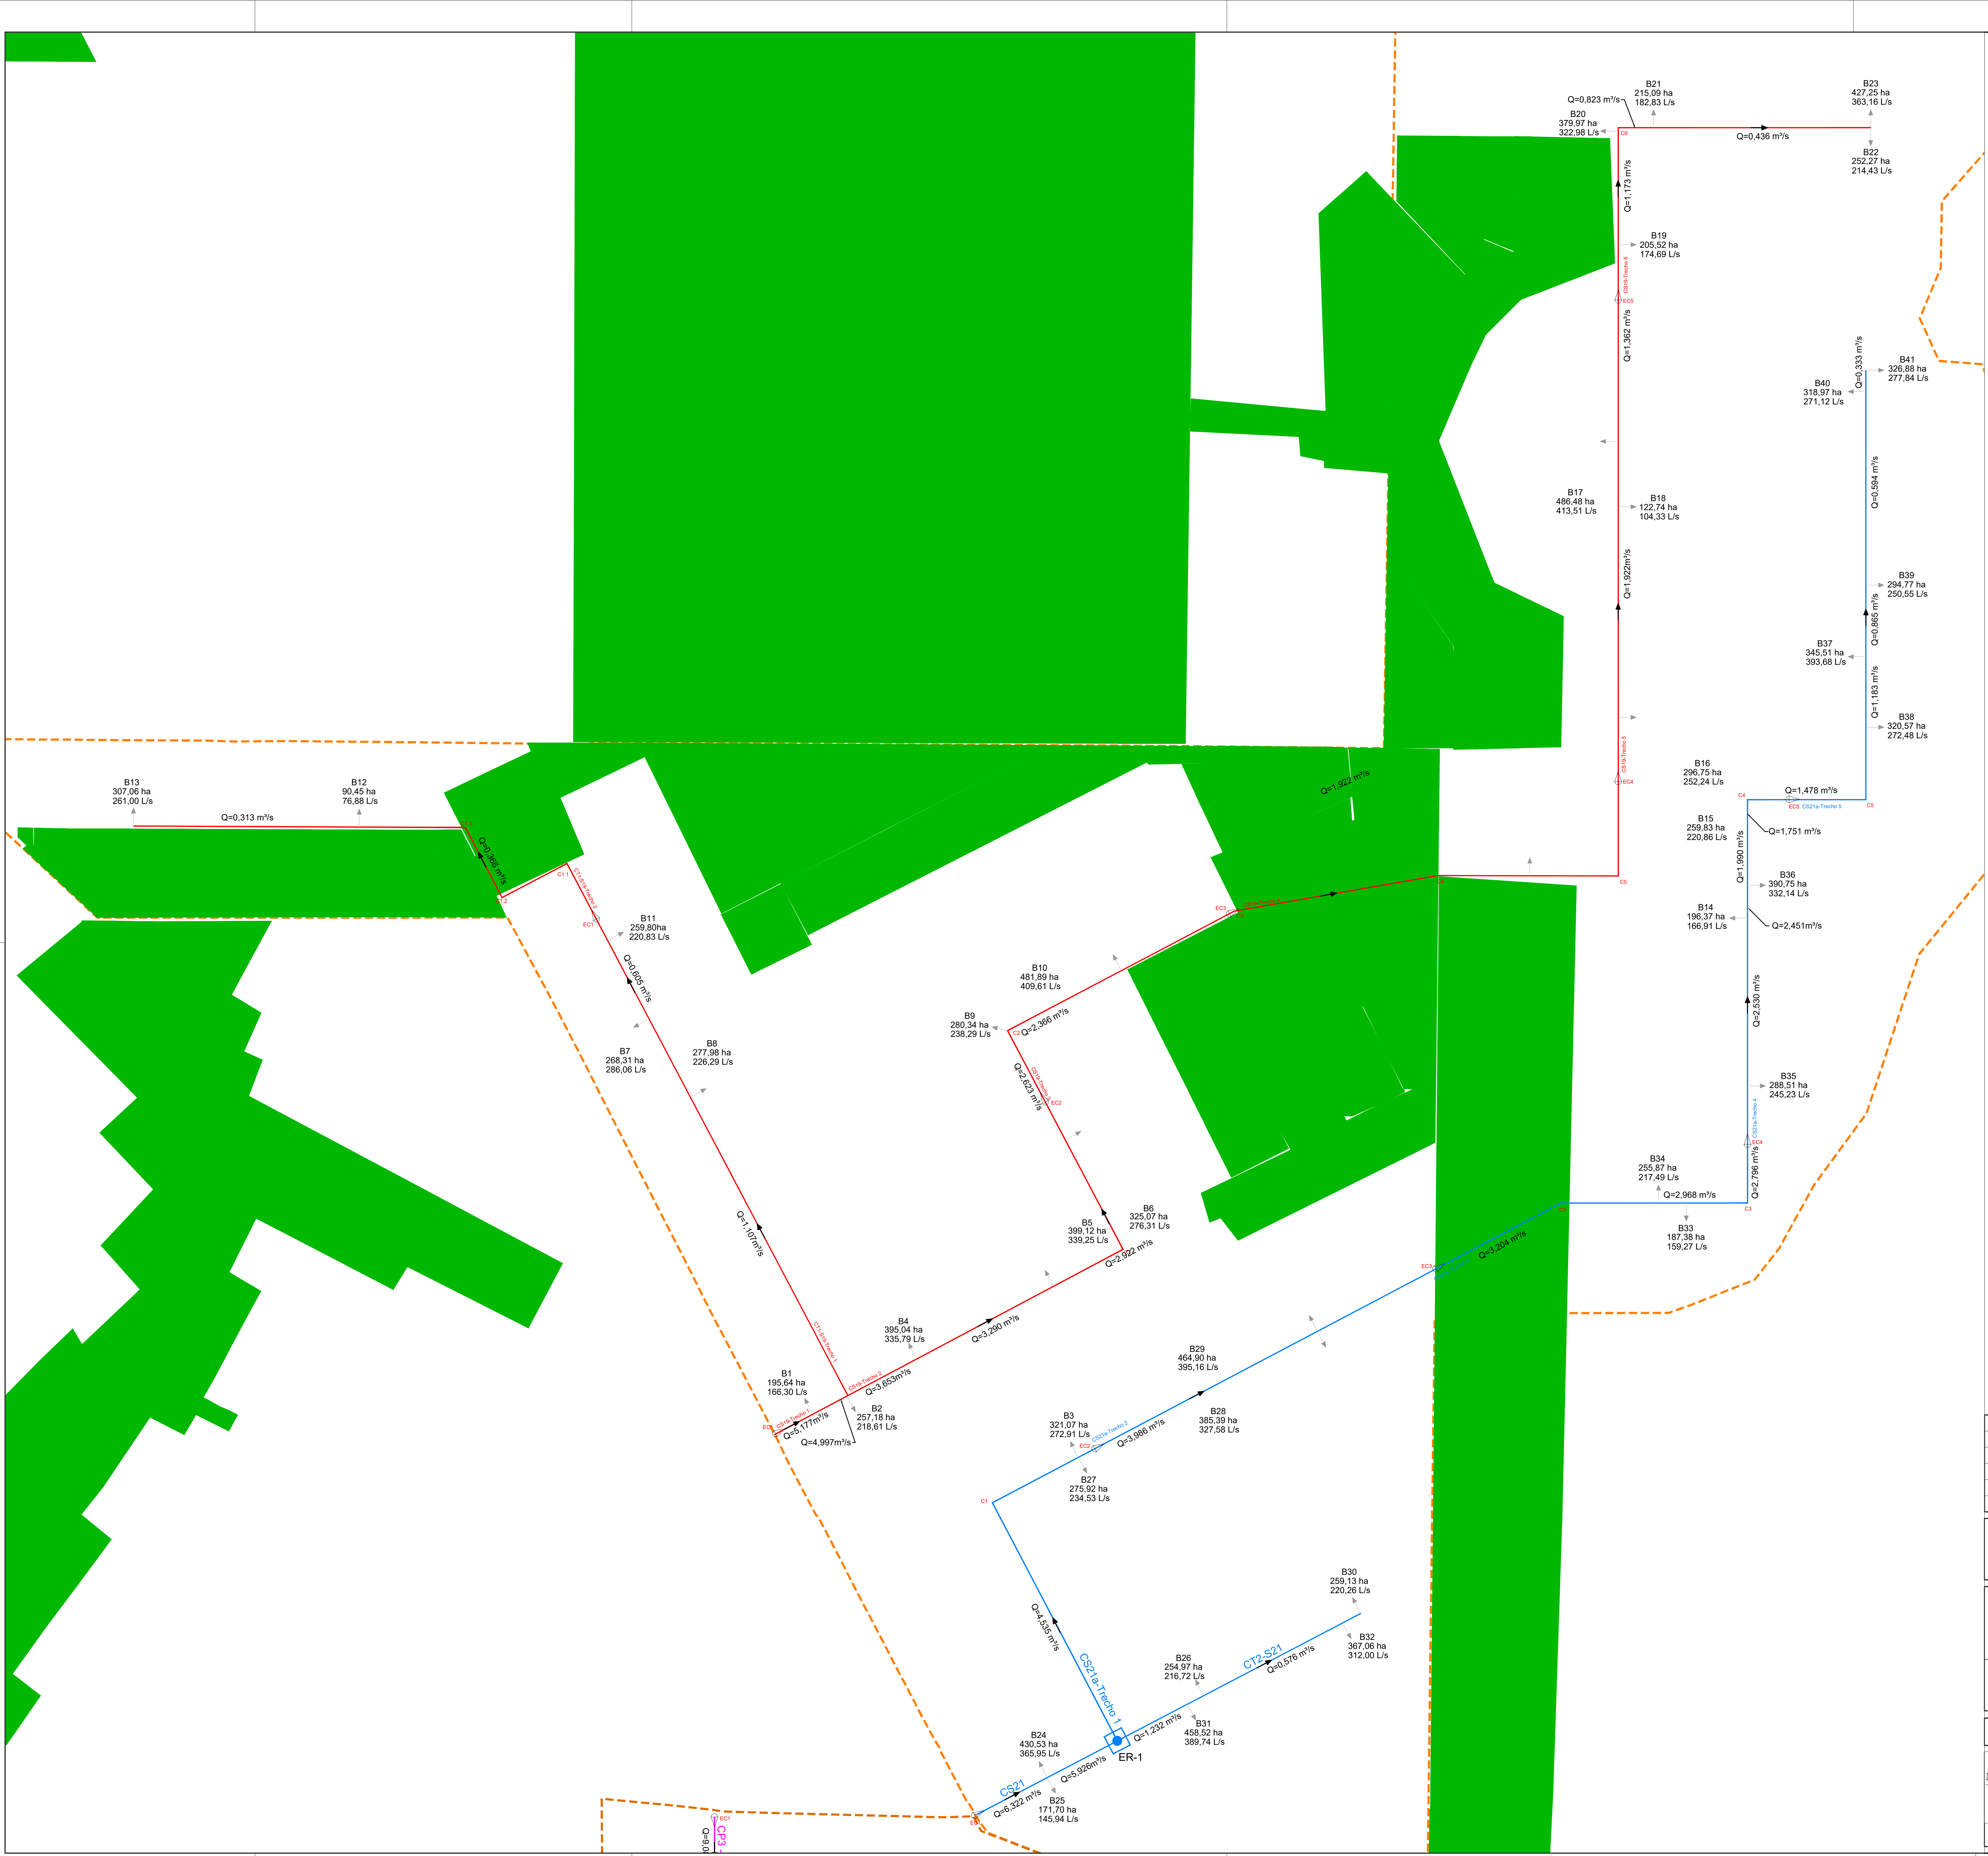

LEGENDA:

- ▬ ▬ LIMITE - JAÍBA III
- ── CANAL ADUTOR - CS-19
- ── CANAL ADUTOR - CS-21
- 🟩 ÁREAS AMBIENTAIS SENSÍVEIS
- ▶ TOMADA D'ÁGUA
- ● ELEVATÓRIA DE RECALQUE
- → SENTIDO DE ESCOAMENTO

NOTAS:

1 - VAZÃO NA PARCELA EM L/S

2 - VAZÃO NO CANAL EM M³/S

| Revisão | Data | Descrição | Elab. | Verif. | Aprov. | Aut. |
|---|---|---|---|---|---|---|
| 3 | 10/02/2026 | Revisão do trecho 6 | AHL | HKZ | EDK | |
| 2 | 25/11/2025 | Revisão da vazão unitária parcelar | AHL | HKZ | EDK | |
| 1 | 13/10/2025 | Revisão do parcelamento das áreas irrigáveis | AHL | HKZ | EDK | |
| 0 | 29/08/2025 | Emissão Inicial | AHL | HKO | EDK | |

FUNDO DE DESENVOLVIMENTO DA INFRAESTRUTURA
REGIONAL SUSTENTÁVEL - FDIRS

# ESTRUTURAÇÃO DE PROJETO DE CONCESSÃO DO PERÍMETRO IRRIGADO DO JAÍBA (ETAPAS 3 E 4)

ANTEPROJETO

## DIAGRAMA DE VAZÕES

ETAPA 3

| Finalidade de Emissão | | | | | | | |
|---|---|---|---|---|---|---|---|
| | 1 Para Informação | 2 Para Comentários | ▨ 3 Para Aprovação | 4 Para Execução | 5 Como Construído | 6 Para Utilização | 7 Para Providências |

Moysés & Pires Sociedade de advogados
ENGECORPS GrupoTYPSA
A&M
Plena Consultoria e Projetos

Data: 29/08/25
Escala: sem escala
Elaboração:
Verificação:
Aprovação
Autorização
Referência:
Revisão: 02
Desenho nº J3-DS-HI-0003