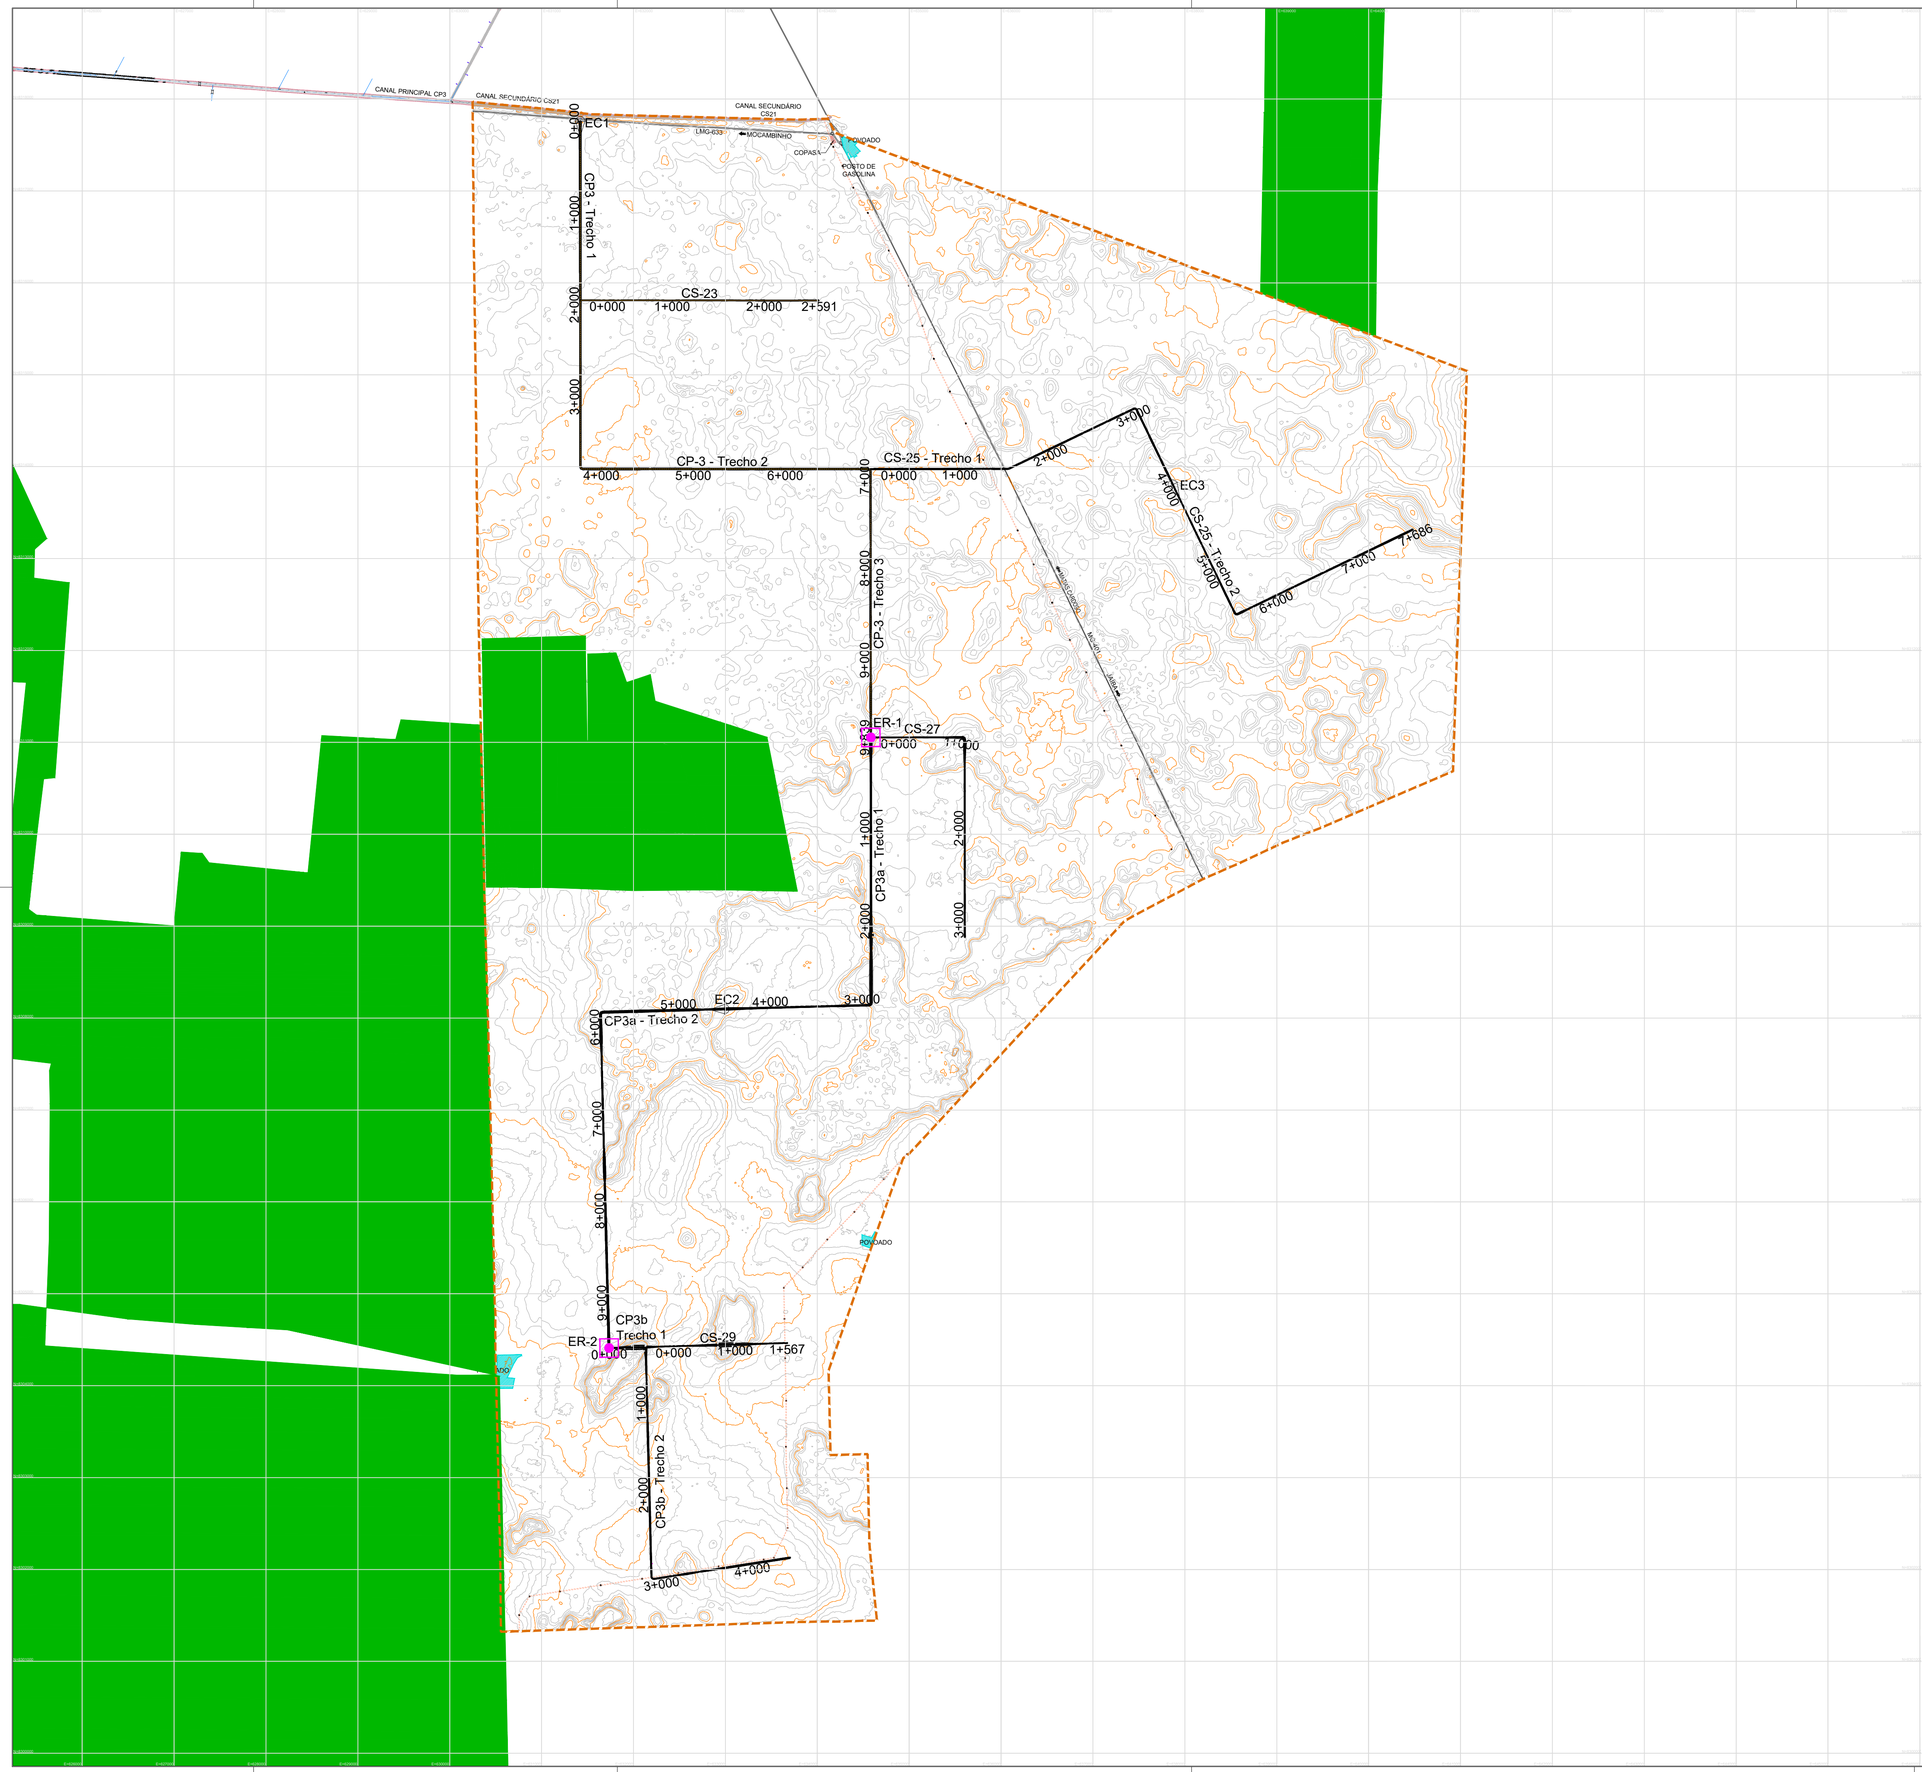


LEGENDA:

- LIMITE - JAÍBA IV
- CANAL ADUTOR
- ÁREAS AMBIENTAIS SENSÍVEIS
- ELEVATÓRIA DE RECALQUE (ER-1 E ER-2)
- ESTAÇÃO DE CONTROLE (EC)

NOTAS:

1 - ÁREA IRRIGADA DOS LOTES EM HECTARES (93% ÁREA BRUTA IRRIGÁVEL)
2 - MEDIDAS EM METRO, EXCETO INDICAÇÃO CONTRÁRIA;
3 - ESTAQUEMANTO INDICADO EM km.

Revisão	Data	Descrição	Elab.	Verif.	Aprov.	Aut.
0	19/09/2025	Emissão Inicial	AHL	HKO	EDK	

FUNDO DE DESENVOLVIMENTO DA INFRAESTRUTURA REGIONAL SUSTENTÁVEL - FDIRS

ESTRUTURAÇÃO DE PROJETO DE CONCESSÃO DO PERÍMETRO IRRIGADO DO JAÍBA (ETAPAS 3 E 4)

ANTEPROJETO

ALTERNATIVA 1 - SISTEMA ADUTOR POR CANAIS

ETAPA 4

Finalidade de Emissão	1 Para Informação	2 Para Comentários	Para Aprovação	4 Para Execução	5 Como Construído	6 Para Utilização	7 Para Providências

Moysés & Pires Sociedade de Engenheiros | ENGECORPS Group | Plena Consultoria e Projetos

Data: 29/08/25	Elaboração:		Verificação:
Escala: sem escala	Aprovação		Autorização
Referência:	Revisão: 00	Desenho nº	J4-DS-HI-0003-00