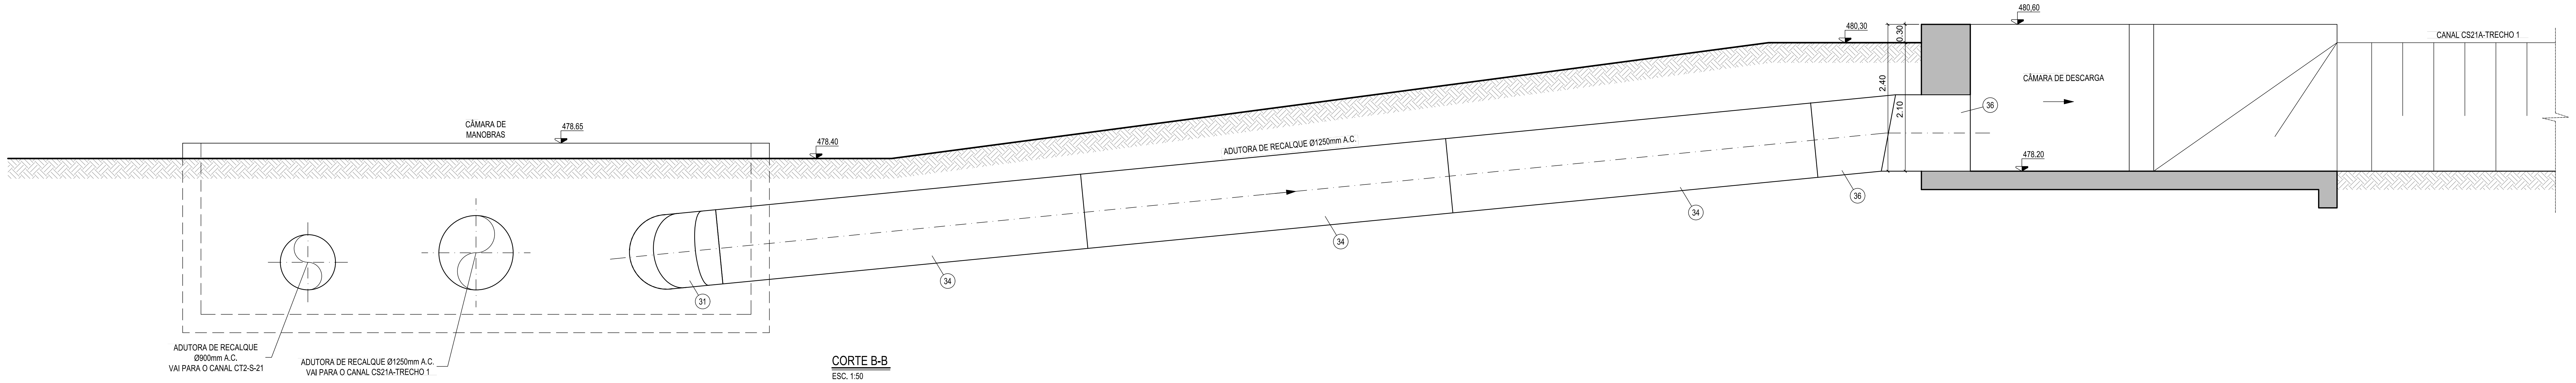

CORTE B-B
ESC. 1:50

QUADRO DE EQUIPAMENTOS DA ELEVATÓRIA

N°	DISCRIMINAÇÃO	MATERIAL	CAP.	ER M1 Ø/L/H(mm)	UNID.	QUANTIDADE
100	BOMBA VERTICAL – CANAL CT2–S–21	--	--	--	CJ	01
101	MOTOR DE INDUÇÃO P/ BOMBA VERTICAL – CANAL CT2–S–21	--	--	--	CJ	01
102	GRADE METÁLICA FIXA	AÇO	--	2.10x2.80	PÇ	01
103	COMPORTA ENSECADEIRA	AÇO	--	2.10x2.80	PÇ	01
104	MONOVIA COM TROLHE E TALHA, PERFIL "I" #4"x15"	AÇO	3ton.	6.500	CJ	01
105	MONOVIA COM TROLHE E TALHA ELÉTRICA, PERFIL "I" #4"x15"	AÇO	5ton.	6.500	CJ	01
106	MONOVIA COM TROLHE E TALHA, PERFIL "I" #4"x15"	AÇO	5ton.	6.500	CJ	01
107	ESCADA MARINHEIRO	AÇO	--	5.000	PÇ	03
108	ESCADA MARINHEIRO	AÇO	--	2.750	PÇ	03
109	ESCADA MARINHEIRO	AÇO	--	2.800	PÇ	03
110	GRADE METÁLICA FIXA	AÇO	--	2.80x2.80	PÇ	02
111	COMPORTA ENSECADEIRA	AÇO	--	2.80x2.80	PÇ	02
112	TAMPA	PRFV	--	0.80x0.80	PÇ	01
113	BOMBA VERTICAL – CANAL CS21A–TRECHO 1	--	--	--	CJ	02
114	MOTOR DE INDUÇÃO P/ BOMBA VERTICAL – CANAL CS21A–TRECHO 1	--	--	--	CJ	02

QUADRO DE TUBULAÇÕES E CONEXÕES DA ELEVATÓRIA – PARTE 1

N°	DISCRIMINAÇÃO	MATERIAL	CHAPA	ER M1		UNID.	QUANTIDADE
				DN(mm)	L(mm)		
01	TUBO COM DERIVAÇÃO, FLANGES E ABA DE VEDAÇÃO	AÇO	#7,1mm	650 x 150	1.500	PÇ	01
02	TOCO COM FLANGE E PONTA	AÇO	#7,1mm	650	450	PÇ	02
03	JUNTA DE DESMONTAGEM TRAVADA AXIALMENTE	AÇO	#7,1mm	650	--	PÇ	01
04	VÁLVULA DE RETENÇÃO COM FLANGES (CLASAR)	F°F°	--	650	--	PÇ	01
05	REGISTRO DE GAVETA COM FLANGES, SÉRIE CHATA	F°F°	--	300	--	PÇ	03
06	VÁLVULA BORBOLETA, ACIONAMENTO ELÉTRICO	F°F°	--	650	--	PÇ	01
07	TUBO COM FLANGE, PONTA E ABA DE VEDAÇÃO	AÇO	#7,1mm	650	1.350	PÇ	01
08	REGISTRO DE GAVETA, SÉRIE CHATA	F°F°	--	150	--	PÇ	01
09	VENTOSA DE TRÍPLICE FUNÇÃO	F°F°	--	150	--	PÇ	01
10	TUBO COM DERIVAÇÃO, FLANGES E PONTA	AÇO	#7,1mm	900 x 300	1.250	PÇ	01
11	REDUÇÃO CONCÊNTRICA COM PONTAS	AÇO	#7,1mm	900 x 650	800	PÇ	01
12	TUBO COM FLANGE E PONTA	AÇO	#7,1mm	900	1.500	PÇ	01
13	TOCO COM FLANGE E PONTA	AÇO	#7,1mm	900	350	PÇ	02
14	JUNTA DE DESMONTAGEM TRAVADA AXIALMENTE	AÇO	#7,1mm	900	--	PÇ	01
15	VÁLVULA BORBOLETA, ACIONAMENTO MANUAL	F°F°	--	900	--	PÇ	01
16	TUBO COM DERIVAÇÃO, FLANGES E ABA DE VEDAÇÃO	AÇO	#7,1mm	950 x 150	1.500	PÇ	02
17	TOCO COM FLANGE E PONTA	AÇO	#7,1mm	950	350	PÇ	04
18	JUNTA DE DESMONTAGEM TRAVADA AXIALMENTE	AÇO	#7,1mm	950	--	PÇ	02
19	VÁLVULA DE RETENÇÃO COM FLANGES (CLASAR)	F°F°	--	950	--	PÇ	02
20	VÁLVULA BORBOLETA, ACIONAMENTO ELÉTRICO	F°F°	--	950	--	PÇ	02

QUADRO DE TUBULAÇÕES E CONEXÕES DA ELEVATÓRIA – PARTE 2

N°	DISCRIMINAÇÃO	MATERIAL	CHAPA	ER M1		UNID.	QUANTIDADE
				DN(mm)	L(mm)		
21	TUBO COM FLANGE E PONTA/ABA DE VEDAÇÃO	AÇO	#7,1mm	950	1.350	PÇ	02
22	TUBO COM DERIVAÇÃO, FLANGES E PONTA	AÇO	#7,1mm	1.250 x 300	1.250	PÇ	02
23	REDUÇÃO CONCÊNTRICA COM PONTAS	AÇO	#7,1mm	1.250 x 950	800	PÇ	02
24	TUBO COM FLANGE E PONTA	AÇO	#7,1mm	1.250	1.500	PÇ	02
25	TOCO COM FLANGE E PONTA	AÇO	#7,1mm	1.250	350	PÇ	04
26	JUNTA DE DESMONTAGEM TRAVADA AXIALMENTE	AÇO	#7,1mm	1.250	--	PÇ	02
27	VÁLVULA BORBOLETA, ACIONAMENTO MANUAL	F°F°	--	1.250	--	PÇ	02
28	TUBO COM PONTAS PARA SOLDA	AÇO	#7,1mm	1.250	1.100	PÇ	01
29	TUBO COM PONTAS PARA SOLDA	AÇO	#7,1mm	1.250	4.200	PÇ	01
30	TUBO COM PONTAS PARA SOLDA	AÇO	#7,1mm	900	6.700	PÇ	01
31	CURVA 90° COM PONTAS PARA SOLDA	AÇO	--	1.250	--	PÇ	02
32	CURVA 90° COM PONTAS PARA SOLDA	AÇO	--	900	--	PÇ	02
33	TUBO COM PONTA PARA SOLDA	AÇO	#7,1mm	900	1.800	PÇ	01
34	TUBO COM PONTA PARA SOLDA	AÇO	#7,1mm	1.250	6.000	PÇ	03
35	TUBO COM PONTA PARA SOLDA	AÇO	#7,1mm	1.250	4.500	PÇ	01
36	TUBO COM PONTA PARA SOLDA	AÇO	#7,1mm	1.250	1.450	PÇ	04
37	TUBO COM FLANGES	AÇO	#7,1mm	950	1.000	PÇ	02
38	TUBO COM PONTA PARA SOLDA	AÇO	#7,1mm	900	1.850	PÇ	01
39	TOCO COM FLANGES	AÇO	#7,1mm	650	300	PÇ	01

NOTAS :

1. MEDIDAS E COTAS EM METROS E DIÂMETROS EM MILÍMETROS, EXCETO COM INDICAÇÃO CONTRÁRIA.
2. TODAS AS MEDIDAS DEVERÃO SER VERIFICADAS NO LOCAL.
3. PARA ESPECIFICAÇÕES DE EQUIPAMENTOS E INSTRUMENTOS VER DOCUMENTO ESPECÍFICO. PARA LISTAS DE MATERIAIS VER ISOMÉTRICO ESPECÍFICO.
4. O FORNECEDOR DOS EQUIPAMENTOS DEVERÃO ANALISAR OS DESENHOS DE HIDROMECÂNICA E ESTRUTURAS E APONTAR EVENTUAIS AJUSTES QUE SE FIZEREM NECESSÁRIOS, PARA O PERFEITO FUNCIONAMENTO DE TODOS OS COM PONENTES DI SISTEMA.
5. DETALHES CONSTRUTIVOS ESPECÍFICOS DE CALDERARIA E MECÂNICA PARA PEÇAS ESPECIAIS E SUPORTES DEVERÃO SER DEFINIDOS NA OCASIÃO DAS OBRAS PELO FORNECEDOR.

Revisão	Data	Descrição	Elab.	Verif.	Aprov.	Aut.
0	11/2025	Emissão Inicial	DGC	AHL	EDK	-

FUNDO DE DESENVOLVIMENTO DA INFRAESTRUTURA
REGIONAL SUSTENTÁVEL - FDIRS

ESTRUTURAÇÃO DE PROJETO DE CONCESSÃO DO
PERÍMETRO IRRIGADO DO JAÍBA (ETAPAS 3 E 4)

ANTEPROJETO

ESTAÇÃO DE RECALQUE
ER1 - ETAPA 3
CORTE E LISTAS DE MATERIAIS

Finalidade de Emissão	1 Para Informação	2 Para COM entários	3 Para Aprovação	4 Para Execução	5 COM o Construído	6 Para Utilização	7 Para Providências

Moysés & Pires Sociedade de advogados
ENGECORPS GrupoTYPSA
A&M
Plena Consultoria e Projetos

Data: 11/2025	Elaboração:		Verificação:
Escala: INDICADAS	Aprovação		Autorização
Referência:	Revisão:	Desenho nº	J3-DS-HI-0007-00