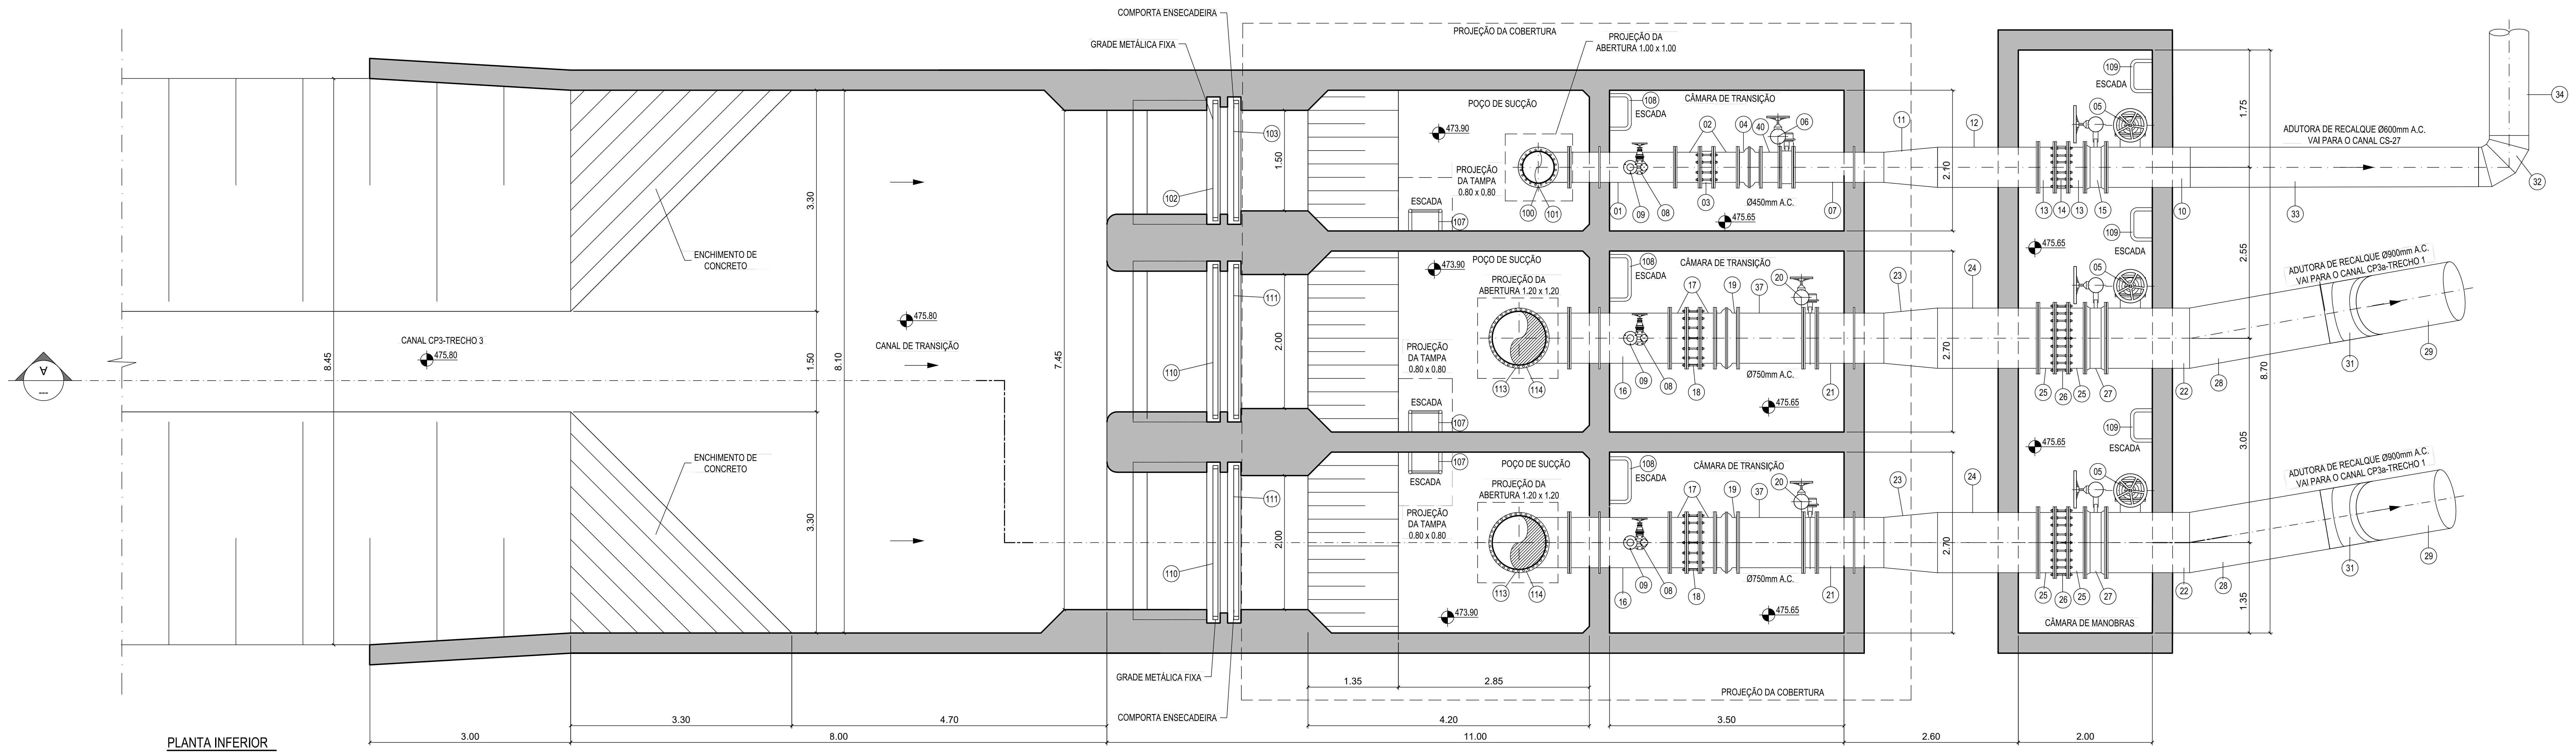

PLANTA INFERIOR
ESC. 1:50

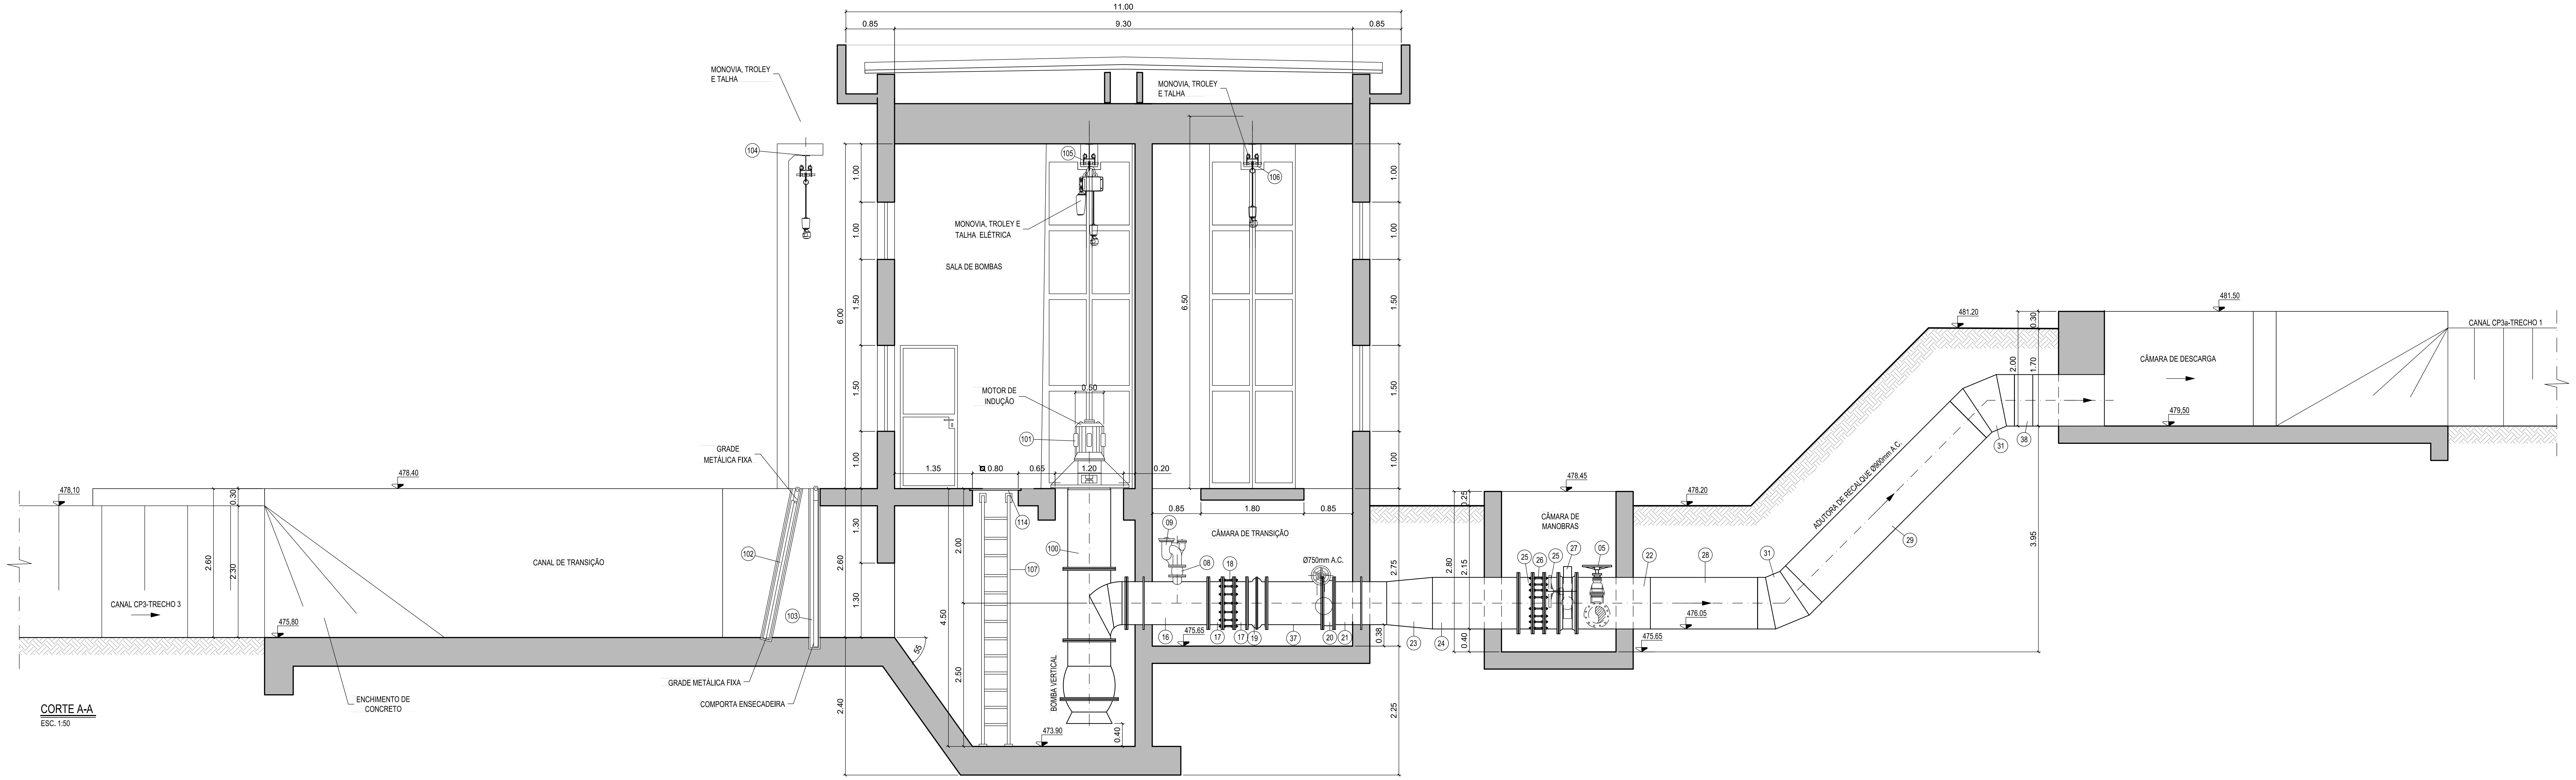

CORTE A-A
ESC. 1:50

NOTAS :

1. MEDIDAS E COTAS EM METROS E DIÂMETROS EM MILÍMETROS, EXCETO COM INDICAÇÃO CONTRÁRIA.
2. TODAS AS MEDIDAS DEVERÃO SER VERIFICADAS NO LOCAL.
3. PARA ESPECIFICAÇÕES DE EQUIPAMENTOS E INSTRUMENTOS VER DOCUMENTO ESPECÍFICO. PARA LISTAS DE MATERIAIS VER ISOMÉTRICO ESPECÍFICO.
4. O FORNECEDOR DOS EQUIPAMENTOS DEVERÃO ANALISAR OS DESENHOS DE HIDROMECÂNICA E ESTRUTURAS E APONTAR EVENTUAIS AJUSTES QUE SE FIZEREM NECESSÁRIOS, PARA O PERFEITO FUNCIONAMENTO DE TODOS OS COM PONENTES DI SISTEMA.
5. DETALHES CONSTRUTIVOS ESPECÍFICOS DE CALDERARIA E MECÂNICA PARA PEÇAS ESPECIAIS E SUPORTES DEVERÃO SER DEFINIDOS NA OCASIÃO DAS OBRAS PELO FORNECEDOR.

0	11/2025	Emissão Inicial	DGC	AHL	EDK	-
Revisão	Data	Descrição	Elab.	Verif.	Aprov.	Aut.

FUNDO DE DESENVOLVIMENTO DA INFRAESTRUTURA
REGIONAL SUSTENTÁVEL - FDIRS

ESTRUTURAÇÃO DE PROJETO DE CONCESSÃO DO
PERÍMETRO IRRIGADO DO JAÍBA (ETAPAS 3 E 4)

ANTEPROJETO

ESTAÇÃO DE RECALQUE
ER1 - ETAPA 4
PLANTA E CORTE

Finalidade de Emissão	1 Para Informação	2 Para Comentários	3 Para Aprovação	4 Para Execução	5 Como Construído	6 Para Utilização	7 Para Providências

Data: 11/2025
Escala: INDICADAS
Elaboração:
Verificação:
Aprovação
Autorização
Referência:
Revisão:
Desenho nº J4-DS-HI-0006-00