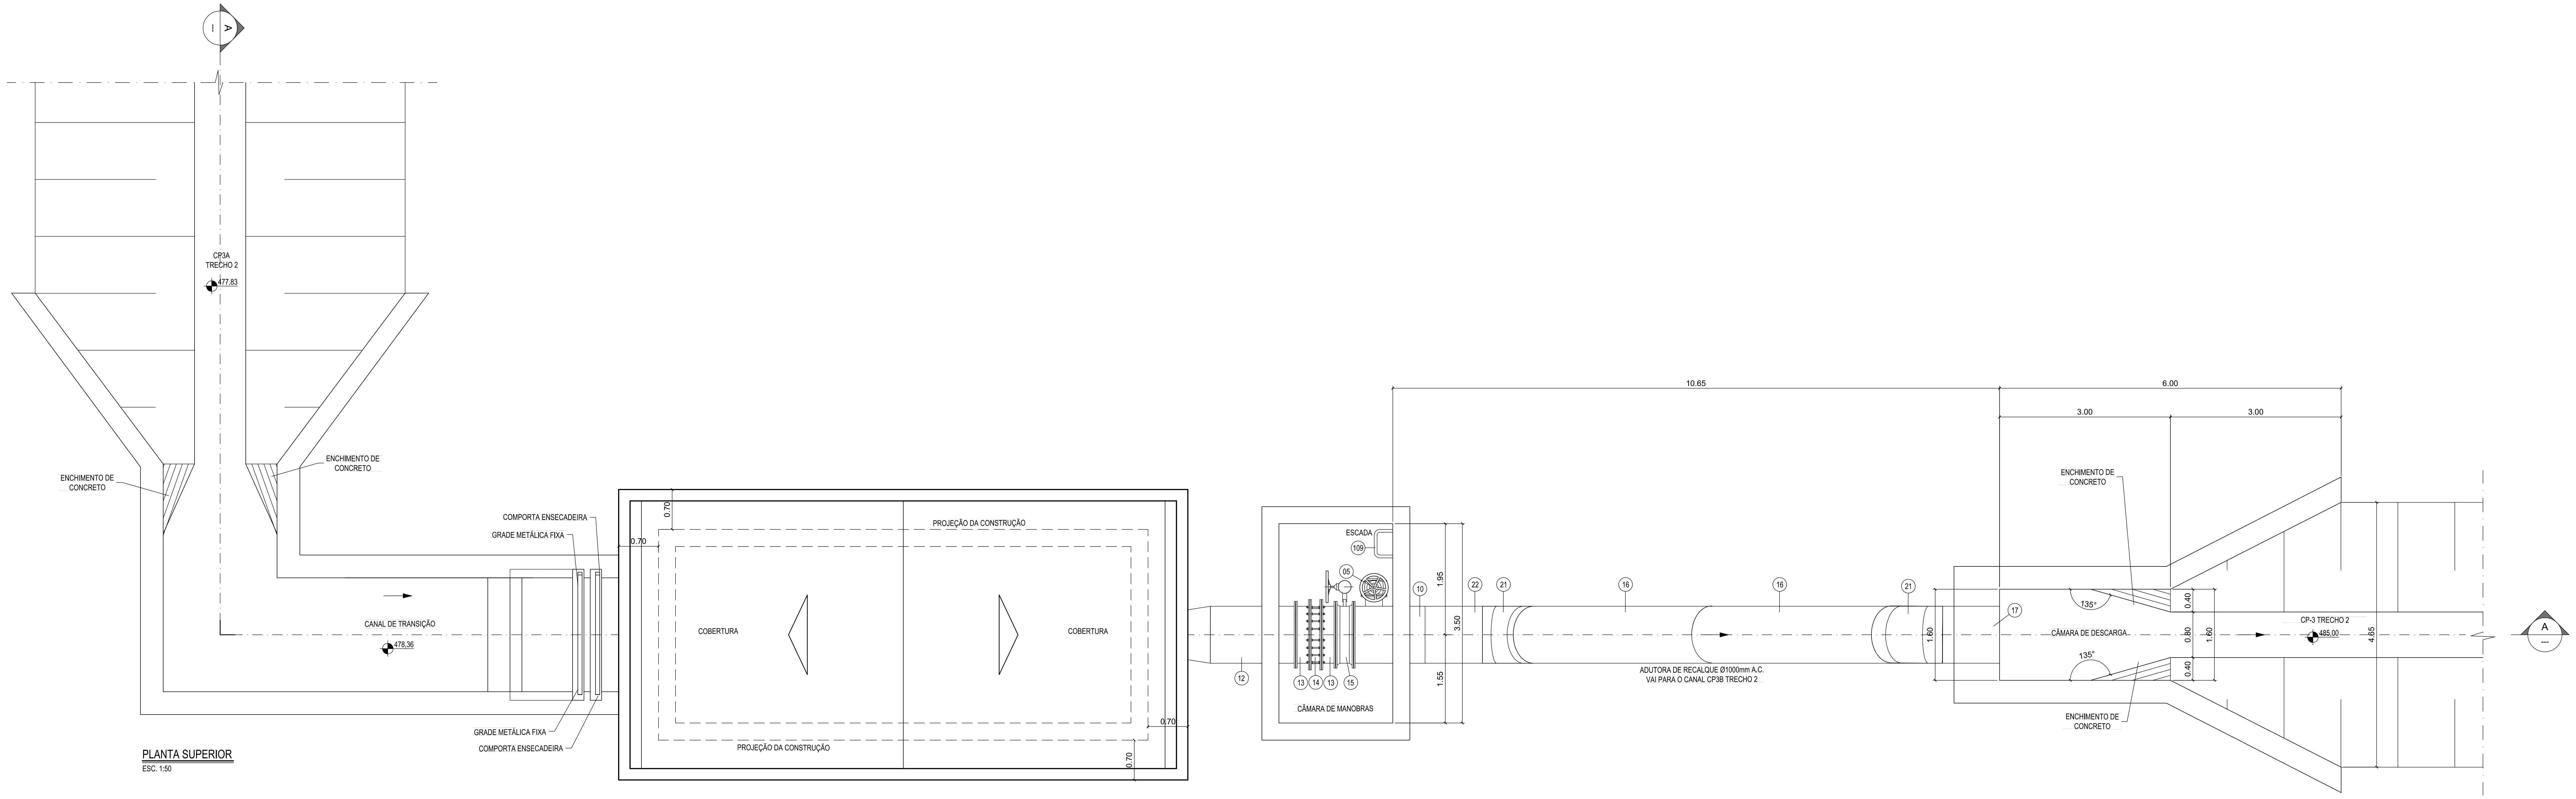
A
CP3A
TRECHO 2
477.83
ENCHIMENTO DE CONCRETO
ENCHIMENTO DE CONCRETO
COMPORTA ENSECADEIRA
GRADE METÁLICA FIXA
CANAL DE TRANSIÇÃO
478,36
GRADE METÁLICA FIXA
COMPORTA ENSECADEIRA
0.70
0.70
PROJEÇÃO DA CONSTRUÇÃO
COBERTURA
COBERTURA
PROJEÇÃO DA CONSTRUÇÃO
0.70
0.70
ESCADA
109
05
10
12
13
14
13
15
CÂMARA DE MANOBRAS
1.95
3.50
1.55
22
21
16
16
21
10.65
ADUTORA DE RECALQUE Ø1000mm A.C.
VAI PARA O CANAL CP3B TRECHO 2
1.60
17
6.00
3.00
3.00
ENCHIMENTO DE CONCRETO
135°
CÂMARA DE DESCARGA
135°
ENCHIMENTO DE CONCRETO
0.40
0.80
0.40
1.60
CP-3 TRECHO 2
485,00
4.65
A

PLANTA SUPERIOR
ESC. 1:50


A
CP3A
TRECHO 2
478,36
6.50
3.00
7.00
1.25
4.00
2.00
0.90
ENCHIMENTO DE CONCRETO
ENCHIMENTO DE CONCRETO
19.60
15.00
4.60
3.70
3.30
1.35
3.15
3.50
2.60
2.00
PROJEÇÃO DA COBERTURA
COMPORTA ENSECADEIRA
GRADE METÁLICA FIXA
CANAL DE TRANSIÇÃO
478,36
2.00
102
103
2.00
107
PROJEÇÃO DA TAMPA 0.80 x 0.80
POÇO DE SUCÇÃO
100
101
PROJEÇÃO DA ABERTURA 1.00 x 1.00
108
ESCADA
PROJEÇÃO DA PISO DA CASA
02
04
20
06
01
09
08
03
Ø750mm A.C.
478,21
07
PROJEÇÃO DA PISO DA CASA
1.55
1.55
11
12
GRADE METÁLICA FIXA
COMPORTA ENSECADEIRA
PROJEÇÃO DA COBERTURA
ESCADA
109
05
10
13
14
13
15
CÂMARA DE MANOBRAS
2.15
3.50
1.55
16
ADUTORA DE RECALQUE Ø1000mm A.C.
VAI PARA O CANAL CP3B TRECHO 1
A

PLANTA INFERIOR
ESC. 1:50

NOTAS :

1. MEDIDAS E COTAS EM METROS E DIÂMETROS EM MILÍMETROS, EXCETO COM INDICAÇÃO CONTRÁRIA.
2. TODAS AS MEDIDAS DEVERÃO SER VERIFICADAS NO LOCAL.
3. PARA ESPECIFICAÇÕES DE EQUIPAMENTOS E INSTRUMENTOS VER DOCUMENTO ESPECÍFICO. PARA LISTAS DE MATERIAIS VER ISOMÉTRICO ESPECÍFICO.
4. O FORNECEDOR DOS EQUIPAMENTOS DEVERÃO ANALISAR OS DESENHOS DE HIDROMECÂNICA E ESTRUTURAS E APONTAR EVENTUAIS AJUSTES QUE SE FIZEREM NECESSÁRIOS, PARA O PERFEITO FUNCIONAMENTO DE TODOS OS COM PONENTES DI SISTEMA.
5. DETALHES CONSTRUTIVOS ESPECÍFICOS DE CALDERARIA E MECÂNICA PARA PEÇAS ESPECIAIS E SUPORTES DEVERÃO SER DEFINIDOS NA OCASIÃO DAS OBRAS PELO FORNECEDOR.

0	11/2025	Emissão Inicial	DGC	AHL	EDK	-
Revisão	Data	Descrição	Elab.	Verif.	Aprov.	Aut.

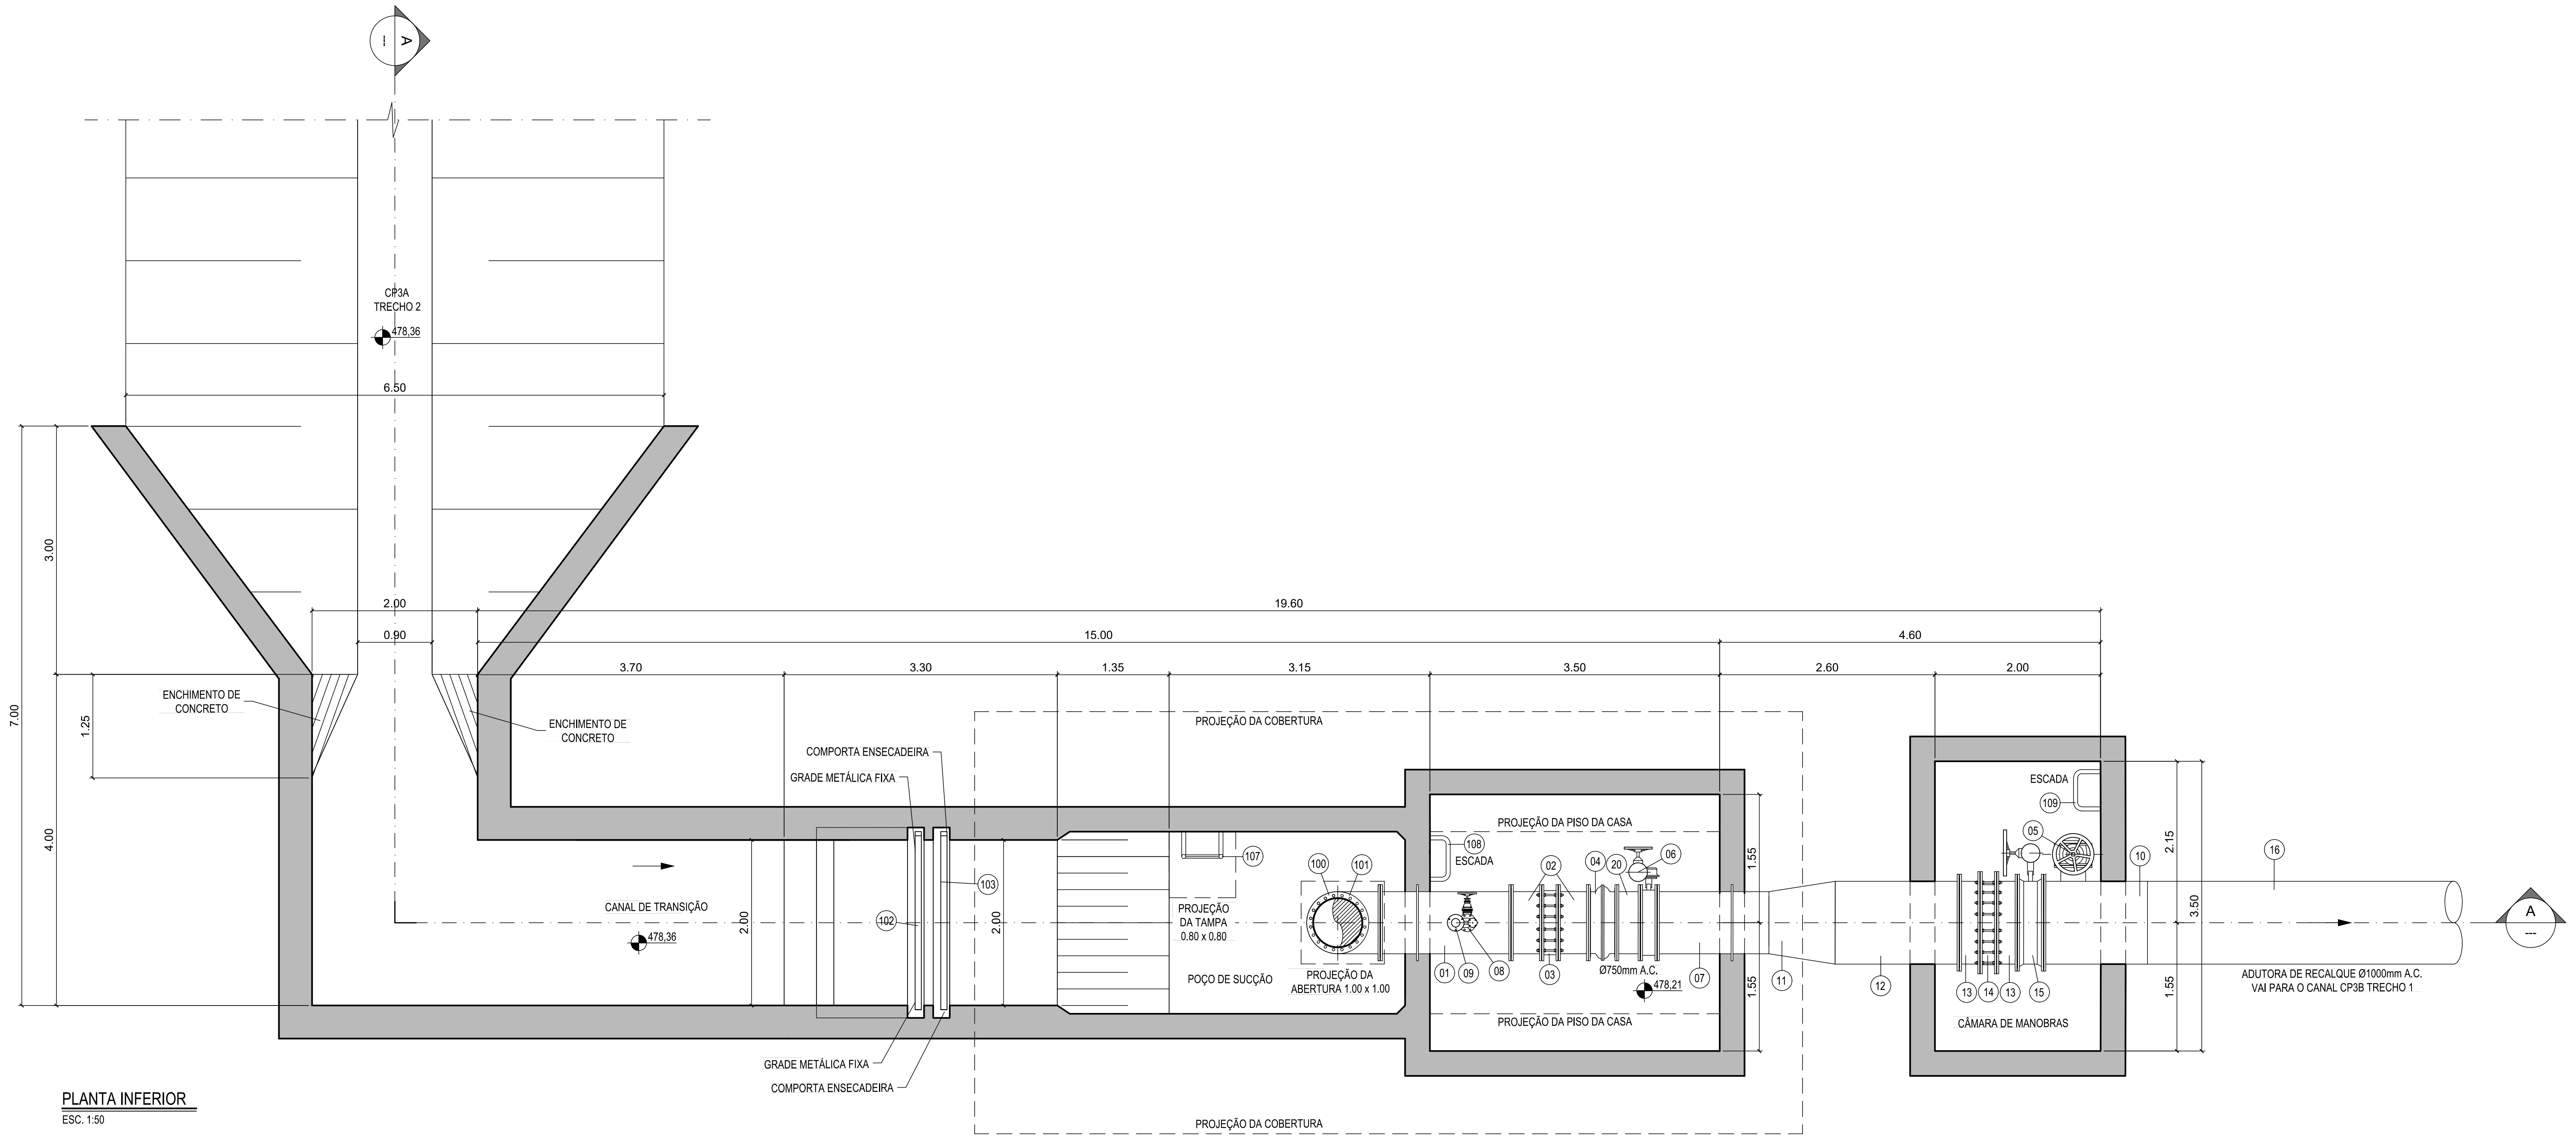FUNDO DE DESENVOLVIMENTO DA INFRAESTRUTURA
REGIONAL SUSTENTÁVEL - FDIRS

ESTRUTURAÇÃO DE PROJETO DE CONCESSÃO DO
PERÍMETRO IRRIGADO DO JAÍBA (ETAPAS 3 E 4)

ANTEPROJETO

ESTAÇÃO DE RECALQUE
ER2 - ETAPA 4
PLANTA E CORTE

Finalidade de Emissão ☐ 1 Para Informação ☐ 2 Para Comentários ☒ 3 Para Aprovação ☐ 4 Para Execução ☐ 5 Como Construído ☐ 6 Para Utilização ☐ 7 Para Providências

Data: 11/2025	Elaboração:	Verificação:	
Escala: INDICADAS	Aprovação	Autorização	
Referência:	Revisão:	Desenho nº	J4-DS-HI-0007-00