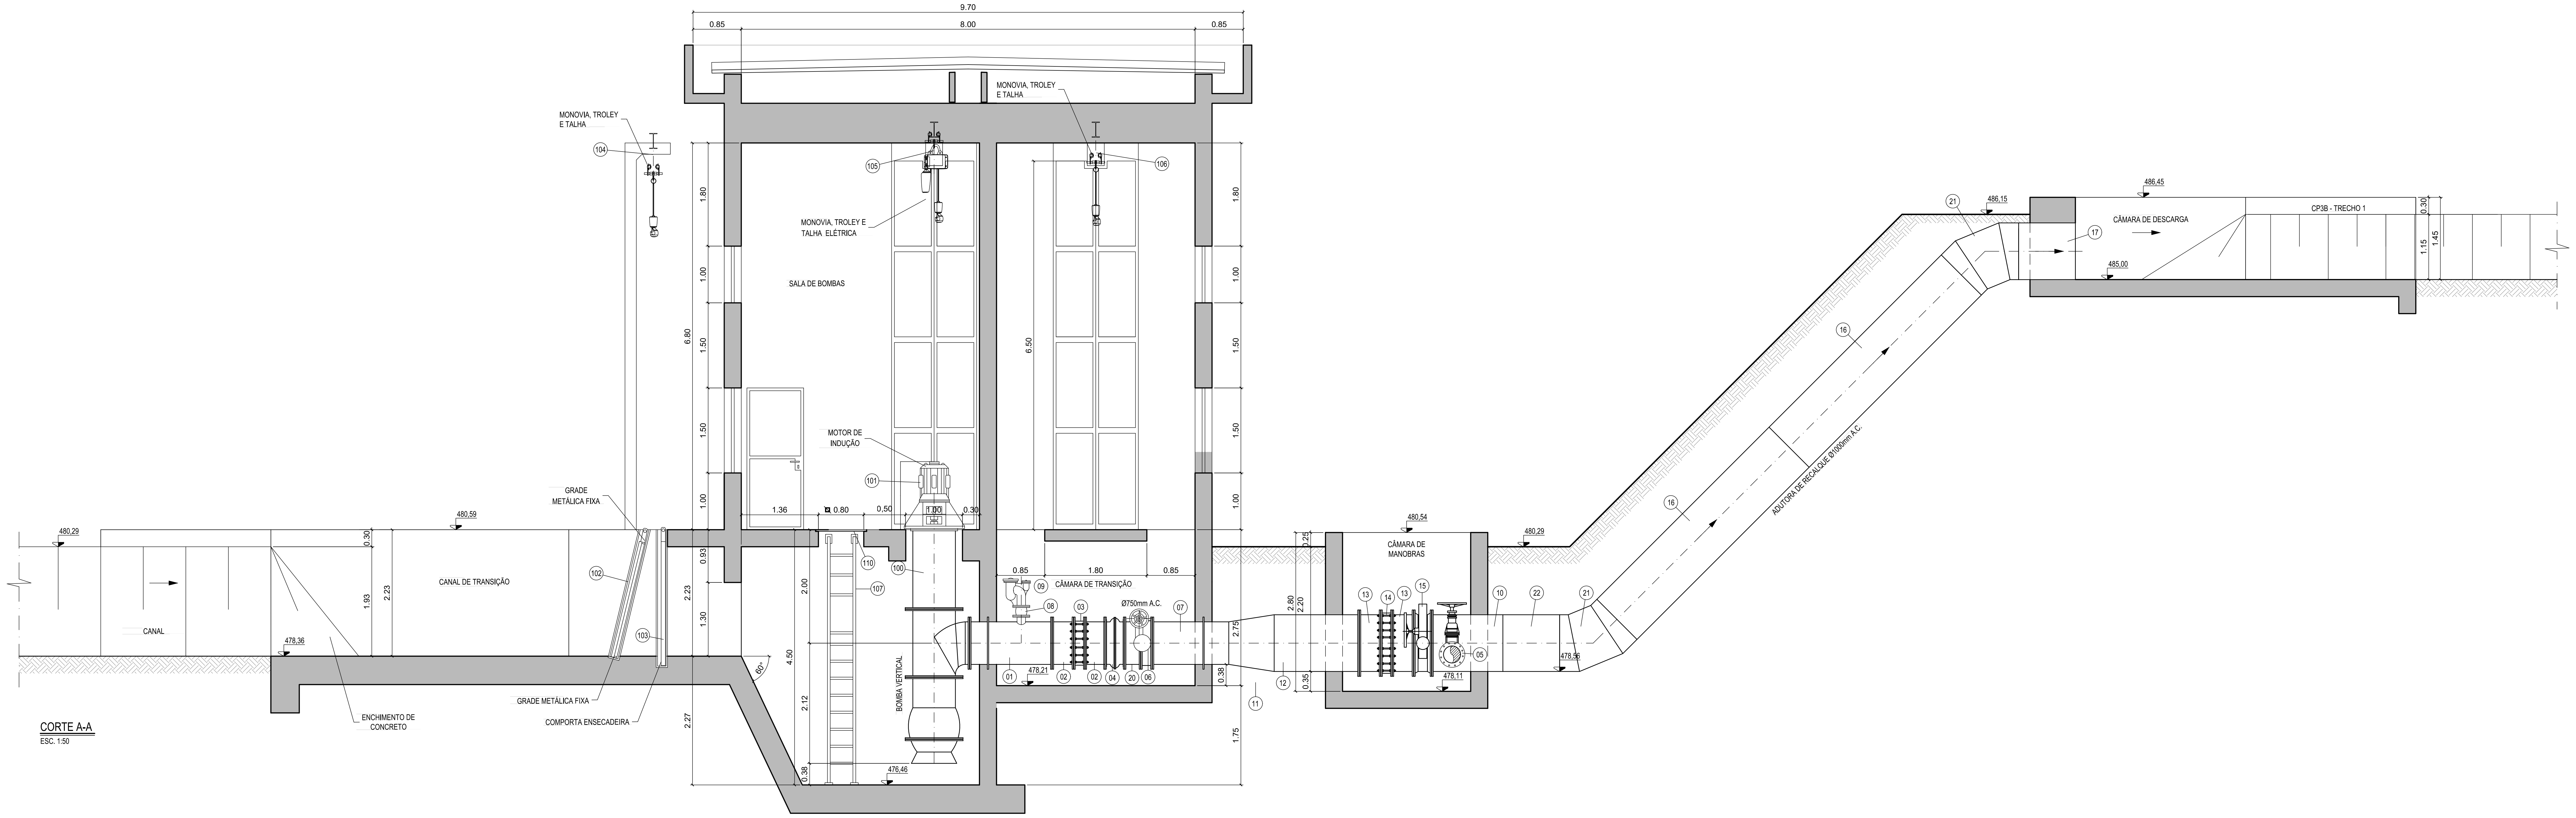
9.70
0.85
8.00
0.85
MONOVIA, TROLEY E TALHA
104
MONOVIA, TROLEY E TALHA
105
106
MONOVIA, TROLEY E TALHA ELÉTRICA
SALA DE BOMBAS
1.80
1.00
1.50
1.50
1.00
6.80
6.50
MOTOR DE INDUÇÃO
101
1.36
0.80
0,50
1.00
0.30
GRADE METÁLICA FIXA
480,29
480,59
0.30
1.93
2.23
CANAL DE TRANSIÇÃO
CANAL
478,36
102
103
0.93
2.23
1.30
2.27
110
100
107
2.00
4.50
2.12
0.38
60°
476,46
BOMBA VERTICAL
ENCHIMENTO DE CONCRETO
GRADE METÁLICA FIXA
COMPORTA ENSECADEIRA
0.85
1.80
0.85
09
CÂMARA DE TRANSIÇÃO
08
03
Ø750mm A.C.
07
01
478,21
02
02
04
20
06
2.75
0.38
1.75
11
12
0.25
2.80
2.20
0.35
480,54
CÂMARA DE MANOBRAS
13
14
13
15
05
478,11
10
22
21
478,56
480,29
16
16
ADUTORA DE RECALQUE Ø1000mm A.C.
21
486,15
486,45
CÂMARA DE DESCARGA
17
485,00
CP3B - TRECHO 1
0.30
1.15
1.45

CORTE A-A
ESC. 1:50

NOTAS :

1. MEDIDAS E COTAS EM METROS E DIÂMETROS EM MILÍMETROS, EXCETO COM INDICAÇÃO CONTRÁRIA.
2. TODAS AS MEDIDAS DEVERÃO SER VERIFICADAS NO LOCAL.
3. PARA ESPECIFICAÇÕES DE EQUIPAMENTOS E INSTRUMENTOS VER DOCUMENTO ESPECÍFICO. PARA LISTAS DE MATERIAIS VER ISOMÉTRICO ESPECÍFICO.
4. O FORNECEDOR DOS EQUIPAMENTOS DEVERÃO ANALISAR OS DESENHOS DE HIDROMECÂNICA E ESTRUTURAS E APONTAR EVENTUAIS AJUSTES QUE SE FIZEREM NECESSÁRIOS, PARA O PERFEITO FUNCIONAMENTO DE TODOS OS COM PONENTES DI SISTEMA.
5. DETALHES CONSTRUTIVOS ESPECÍFICOS DE CALDERARIA E MECÂNICA PARA PEÇAS ESPECIAIS E SUPORTES DEVERÃO SER DEFINIDOS NA OCASIÃO DAS OBRAS PELO FORNECEDOR.

QUADRO DE EQUIPAMENTOS DA ELEVATÓRIA

N°	DISCRIMINAÇÃO	MATERIAL	CAP.	ER M1 Ø/L/H(mm)	UNID.	QUANTIDADE
100	BOMBA VERTICAL	--	--	--	CJ	01
101	MOTOR DE INDUÇÃO P/ BOMBA VERTICAL	--	--	--	CJ	01
102	GRADE METÁLICA FIXA	AÇO	--	2.20x2.60	PÇ	01
103	COMPORTA ENSECADEIRA	AÇO	--	2.20x2.60	PÇ	01
104	MONOVIA COM TROLHE E TALHA, PERFIL "I" #4"x15"	AÇO	3ton.	6.500	CJ	01
105	MONOVIA COM TROLHE E TALHA ELÉTRICA, PERFIL "I" #4"x15"	AÇO	5ton.	6.500	CJ	01
106	MONOVIA COM TROLHE E TALHA, PERFIL "I" #4"x15"	AÇO	5ton.	6.500	CJ	01
107	ESCADA MARINHEIRO	AÇO	--	4.500	PÇ	01
108	ESCADA MARINHEIRO	AÇO	--	2.750	PÇ	01
109	ESCADA MARINHEIRO	AÇO	--	2.800	PÇ	01
110	TAMPA	PRFV	--	0.80x0.80	PÇ	01

QUADRO DE TUBULAÇÕES E CONEXÕES DA ELEVATÓRIA – PARTE 1

N°	DISCRIMINAÇÃO	MATERIAL	CHAPA	ER M1		UNID.	QUANTIDADE
				DN(mm)	L(mm)		
01	TUBO COM DERIVAÇÃO, FLANGES E ABA DE VEDAÇÃO	AÇO	#7,1mm	x 750/150	1.500	PÇ	01
02	TOCO COM FLANGE E PONTA	AÇO	#7,1mm	750	450	PÇ	02
03	JUNTA DE DESMONTAGEM TRAVADA AXIALMENTE	AÇO	#7,1mm	750	--	PÇ	01
04	VÁLVULA DE RETENÇÃO COM FLANGES (CLASAR)	F°F°	--	750	--	PÇ	01
05	REGISTRO DE GAVETA COM FLANGES, SÉRIE CHATA	F°F°	--	300	--	PÇ	01
06	VÁLVULA BORBOLETA, ACIONAMENTO ELÉTRICO	F°F°	--	750	--	PÇ	01
07	TUBO COM FLANGE, PONTA E ABA DE VEDAÇÃO	AÇO	#7,1mm	750	1.350	PÇ	01
08	REGISTRO DE GAVETA, SÉRIE CHATA	F°F°	--	150	--	PÇ	01
09	VENTOSA DE TRÍPLICE FUNÇÃO	F°F°	--	150	--	PÇ	01
10	TUBO COM DERIVAÇÃO, FLANGES E PONTA	AÇO	#7,1mm	x 1000/300	1.250	PÇ	01
11	REDUÇÃO CONCÊNTRICA COM PONTAS	AÇO	#7,1mm	x 1000/750	800	PÇ	01
12	TUBO COM FLANGE E PONTA	AÇO	#7,1mm	1000	1.500	PÇ	01
13	TOCO COM FLANGE E PONTA	AÇO	#7,1mm	1000	350	PÇ	02
14	JUNTA DE DESMONTAGEM TRAVADA AXIALMENTE	AÇO	#7,1mm	1000	--	PÇ	01
15	VÁLVULA BORBOLETA, ACIONAMENTO MANUAL	F°F°	--	1000	--	PÇ	01
16	TUBO COM PONTAS PARA SOLDA	AÇO	#7,1mm	1000	4.290	PÇ	02
17	TUBO COM PONTA PARA SOLDA	AÇO	#7,1mm	1000	1.000	PÇ	01
20	TOCO COM FLANGES	AÇO	#7,1mm	750	300	PÇ	01
21	CURVA 45° COM PONTAS PARA SOLDA	AÇO	#7,1mm	1000	--	PÇ	02
22	TUBO COM PONTA PARA SOLDA	AÇO	#7,1mm	1000	1.000	PÇ	01

Revisão	Data	Descrição	Elab.	Verif.	Aprov.	Aut.
0	11/2025	Emissão Inicial	DGC	AHL	EDK	-

FUNDO DE DESENVOLVIMENTO DA INFRAESTRUTURA
REGIONAL SUSTENTÁVEL - FDIRS

ESTRUTURAÇÃO DE PROJETO DE CONCESSÃO DO
PERÍMETRO IRRIGADO DO JAÍBA (ETAPAS 3 E 4)

ANTEPROJETO

ESTAÇÃO DE RECALQUE
ER2 - ETAPA 4
PLANTA E LISTAS DE MATERIAIS

Finalidade de Emissão: ☐ 1 Para Informação ☐ 2 Para Comentários ■ 3 Para Aprovação ☐ 4 Para Execução ☐ 5 Como Construído ☐ 6 Para Utilização ☐ 7 Para Providências

Data: 11/2025
Escala: INDICADAS
Elaboração:
Verificação:
Aprovação
Autorização
Referência:
Revisão:
Desenho nº J4-DS-HI-0007-00