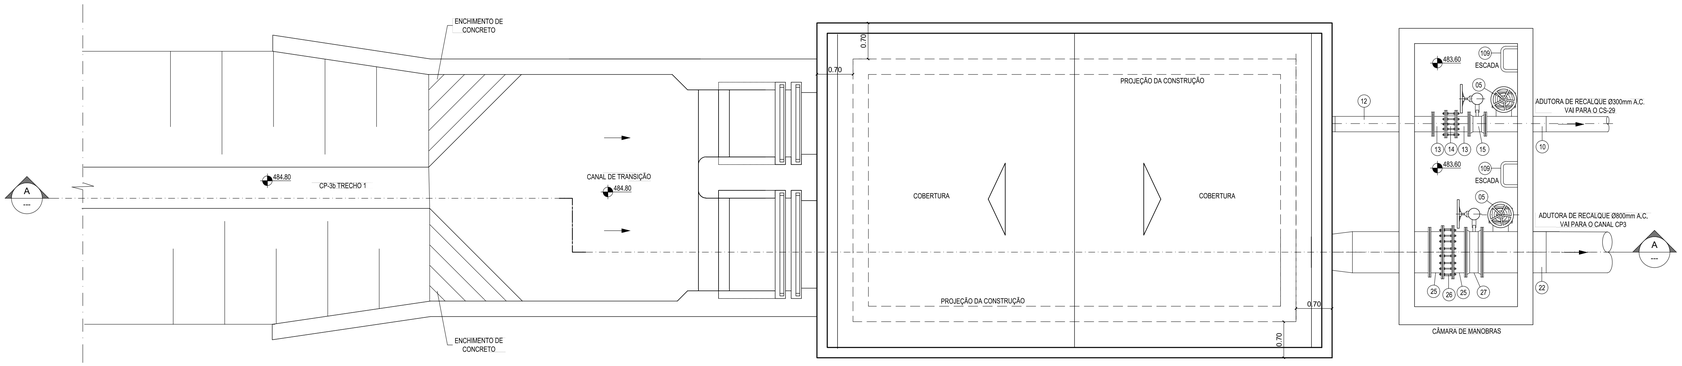


PLANTA SUPERIOR

ESC. 1:50

NOTAS :

1. MEDIDAS E COTAS EM METROS E DIÂMETROS EM MILÍMETROS, EXCETO COM INDICAÇÃO CONTRÁRIA.
2. TODAS AS MEDIDAS DEVERÃO SER VERIFICADAS NO LOCAL.
3. PARA ESPECIFICAÇÕES DE EQUIPAMENTOS E INSTRUMENTOS VER DOCUMENTO ESPECÍFICO. PARA LISTAS DE MATERIAIS VER ISOMÉTRICO ESPECÍFICO.
4. O FORNECEDOR DOS EQUIPAMENTOS DEVERÃO ANALISAR OS DESENHOS DE HIDROMECÂNICA E ESTRUTURAS E APONTAR EVENTUAIS AJUSTES QUE SE FIZEREM NECESSÁRIOS, PARA O PERFEITO FUNCIONAMENTO DE TODOS OS COM PONENTES DI SISTEMA.
5. DETALHES CONSTRUTIVOS ESPECÍFICOS DE CALDERARIA E MECÂNICA PARA PEÇAS ESPECIAIS E SUPORTES DEVERÃO SER DEFINIDOS NA OCASIÃO DAS OBRAS PELO FORNECEDOR.

QUADRO DE EQUIPAMENTOS DA ELEVATÓRIA

Nº	DISCRIMINAÇÃO	MATERIAL	CAP.	ER M1 Ø/L/H(mm)	UNID.	QUANTIDADE
100	BOMBA VERTICAL – CANAL CT2-S-21	--	--	--	CJ	02
101	MOTOR DE INDUÇÃO P/ BOMBA VERTICAL – CANAL CT2-S-21	--	--	--	CJ	02
102	GRADE METÁLICA FIXA	AÇO	--	1.70x1.65	PÇ	01
103	COMPORTA ENSECADEIRA	AÇO	--	1.70x1.65	PÇ	01
104	MONOVIA COM TROLHE E TALHA, PERFIL "I" Ø4"x15"	AÇO	3ton.	6.500	CJ	01
105	MONOVIA COM TROLHE E TALHA ELÉTRICA, PERFIL "I" Ø4"x15"	AÇO	5ton.	6.500	CJ	01
106	MONOVIA COM TROLHE E TALHA, PERFIL "I" Ø4"x15"	AÇO	5ton.	6.500	CJ	01
107	ESCADA MARINHEIRO	AÇO	--	5.000	PÇ	02
108	ESCADA MARINHEIRO	AÇO	--	2.750	PÇ	02
109	ESCADA MARINHEIRO	AÇO	--	2.800	PÇ	02
110	TAMPA	PRFV	--	0.80x0.80	PÇ	02
111	GRADE METÁLICA FIXA	AÇO	--	1.20x1.65	PÇ	01
112	COMPORTA ENSECADEIRA	AÇO	--	1.20x1.65	PÇ	01

QUADRO DE TUBULAÇÕES E CONEXÕES DA ELEVATÓRIA – PARTE 1

Nº	DISCRIMINAÇÃO	MATERIAL	CHAPA	ER M1 DN(mm)	ER M1 L(mm)	UNID.	QUANTIDADE
01	TUBO COM DERIVAÇÃO, FLANGES E ABA DE VEDAÇÃO	AÇO	∯7,1mm	250 x 150	1.500	PÇ	02
02	TOCO COM FLANGE E PONTA	AÇO	∯7,1mm	200	350	PÇ	04
03	JUNTA DE DESMONTAGEM TRAVADA AXIALMENTE	AÇO	∯7,1mm	200	--	PÇ	02
04	VÁLVULA DE RETENÇÃO COM FLANGES (CLASAR)	F"F"	--	200	--	PÇ	02
05	REGISTRO DE GAVETA COM FLANGES, SÉRIE CHATA	F"F"	--	300	--	PÇ	02
06	VÁLVULA BORBOLETA, ACIONAMENTO ELÉTRICO	F"F"	--	200	--	PÇ	02
07	TUBO COM FLANGE, PONTA E ABA DE VEDAÇÃO	AÇO	∯7,1mm	600	1.350	PÇ	02
08	REGISTRO DE GAVETA, SÉRIE CHATA	F"F"	--	100	--	PÇ	02
09	VENTOSA DE TRIPLICE FUNÇÃO	F"F"	--	100	--	PÇ	02
10	TUBO COM DERIVAÇÃO, FLANGES E PONTA	AÇO	∯7,1mm	300 x 300	1.250	PÇ	02
11	REDUÇÃO CONCÊNTRICA COM PONTAS	AÇO	∯7,1mm	300 x 250	400	PÇ	02
12	TUBO COM FLANGE E PONTA	AÇO	∯7,1mm	300	1.900	PÇ	02
13	TOCO COM FLANGE E PONTA	AÇO	∯7,1mm	300	350	PÇ	04
14	JUNTA DE DESMONTAGEM TRAVADA AXIALMENTE	AÇO	∯7,1mm	300	--	PÇ	02
15	VÁLVULA BORBOLETA, ACIONAMENTO MANUAL	F"F"	--	300	--	PÇ	02
16	TUBO COM PONTAS PARA SOLDA	AÇO	∯7,1mm	600	6.700	PÇ	02
17	TOCO COM FLANGE E PONTA	AÇO	∯7,1mm	600	250	PÇ	02
18	TUBO COM PONTA PARA SOLDA	AÇO	∯7,1mm	600	1.800	PÇ	01
19	TUBO COM PONTA PARA SOLDA	AÇO	∯7,1mm	600	1.850	PÇ	01
20	TOCO COM FLANGE E PONTA	AÇO	∯7,1mm	600	300	PÇ	02

QUADRO DE TUBULAÇÕES E CONEXÕES DA ELEVATÓRIA – PARTE 2

Nº	DISCRIMINAÇÃO	MATERIAL	CHAPA	ER M1 DN(mm)	ER M1 L(mm)	UNID.	QUANTIDADE
21	TUBO COM FLANGE E PONTA/ABA DE VEDAÇÃO	AÇO	∯7,1mm	600	0.980	PÇ	02
22	TUBO COM DERIVAÇÃO, FLANGES E PONTA	AÇO	∯7,1mm	800 x 300	1.250	PÇ	02
23	REDUÇÃO CONCÊNTRICA COM PONTAS	AÇO	∯7,1mm	800 x 600	800	PÇ	02
24	TUBO COM FLANGE E PONTA	AÇO	∯7,1mm	800	1.500	PÇ	02
25	TOCO COM FLANGE E PONTA	AÇO	∯7,1mm	800	250	PÇ	04
26	JUNTA DE DESMONTAGEM TRAVADA AXIALMENTE	AÇO	∯7,1mm	800	--	PÇ	02
27	VÁLVULA BORBOLETA, ACIONAMENTO MANUAL	F"F"	--	800	--	PÇ	02
28	TUBO COM PONTA PARA SOLDA	F"F"	∯7,1mm	600	950	PÇ	02
29	TOCO COM PONTA PARA SOLDA	F"F"	∯7,1mm	250	300	PÇ	02

Revisão	Data	Descrição	Elab.	Verif.	Aprov.	Aut.
0	11/2025	Emissão Inicial	DGC	AHL	EDK	-

FUNDO DE DESENVOLVIMENTO DA INFRAESTRUTURA REGIONAL SUSTENTÁVEL - FDIRS

ESTRUTURAÇÃO DE PROJETO DE CONCESSÃO DO PERÍMETRO IRRIGADO DO JAÍBA (ETAPAS 3 E 4)

ANTEPROJETO

ESTAÇÃO DE RECALQUE
ER3 - ETAPA 4
PLANTA E LISTAS DE MATERIAIS

Finalidade de Emissão	1 Para Informação	2 Para Comentários	3 Para Aprovação	4 Para Execução	5 Como Construído	6 Para Utilização	7 Para Providências

Moyses & Pires Engenharia | ENGECORPS | Plena Consultoria e Projetos

Data: 11/2025 | Elaboração: | Verificação:

Escala: INDICADAS | Aprovação | Autorização

Referência: | Revisão: | Desenho nº J4-DS-HI-0008-00