ENCHIMENTO DE CONCRETO
COMPORTA ENSECADEIRA
GRADE METÁLICA FIXA
0.70
PROJEÇÃO DA CONSTRUÇÃO
CANAL
476.08
CANAL DE TRANSIÇÃO
476.08
1.55
1.20
4.30
1.55
COBERTURA
COBERTURA
PROJEÇÃO DA CONSTRUÇÃO
0.70
0.70
GRADE METÁLICA FIXA
COMPORTA ENSECADEIRA
ENCHIMENTO DE CONCRETO
ESCADA
109
475.13
05
13 14 13 15
12
CÂMARA DE MANOBRAS
10
16
7.45
ADUTORA DE RECALQUE Ø900mm A.C.
VAI PARA O CANAL CS-25 - TRECHO 1
ADUTORA DE RECALQUE Ø900mm A.C.
VAI PARA O CANAL CS-25 - TRECHO 1
ESCADA
7.55
4.55
3.00
1.60
4.00
1.60
2.00
17
135°
ENCHIMENTO DE CONCRETO
CÂMARA DE DESCARGA
477.38
1.40
1.20
4.00
1.40
CS-25 - TRECHO 1
477.38
5.90
A

PLANTA DAS INTERLIGAÇÕES COM OS CANAIS

ESC. 1:50

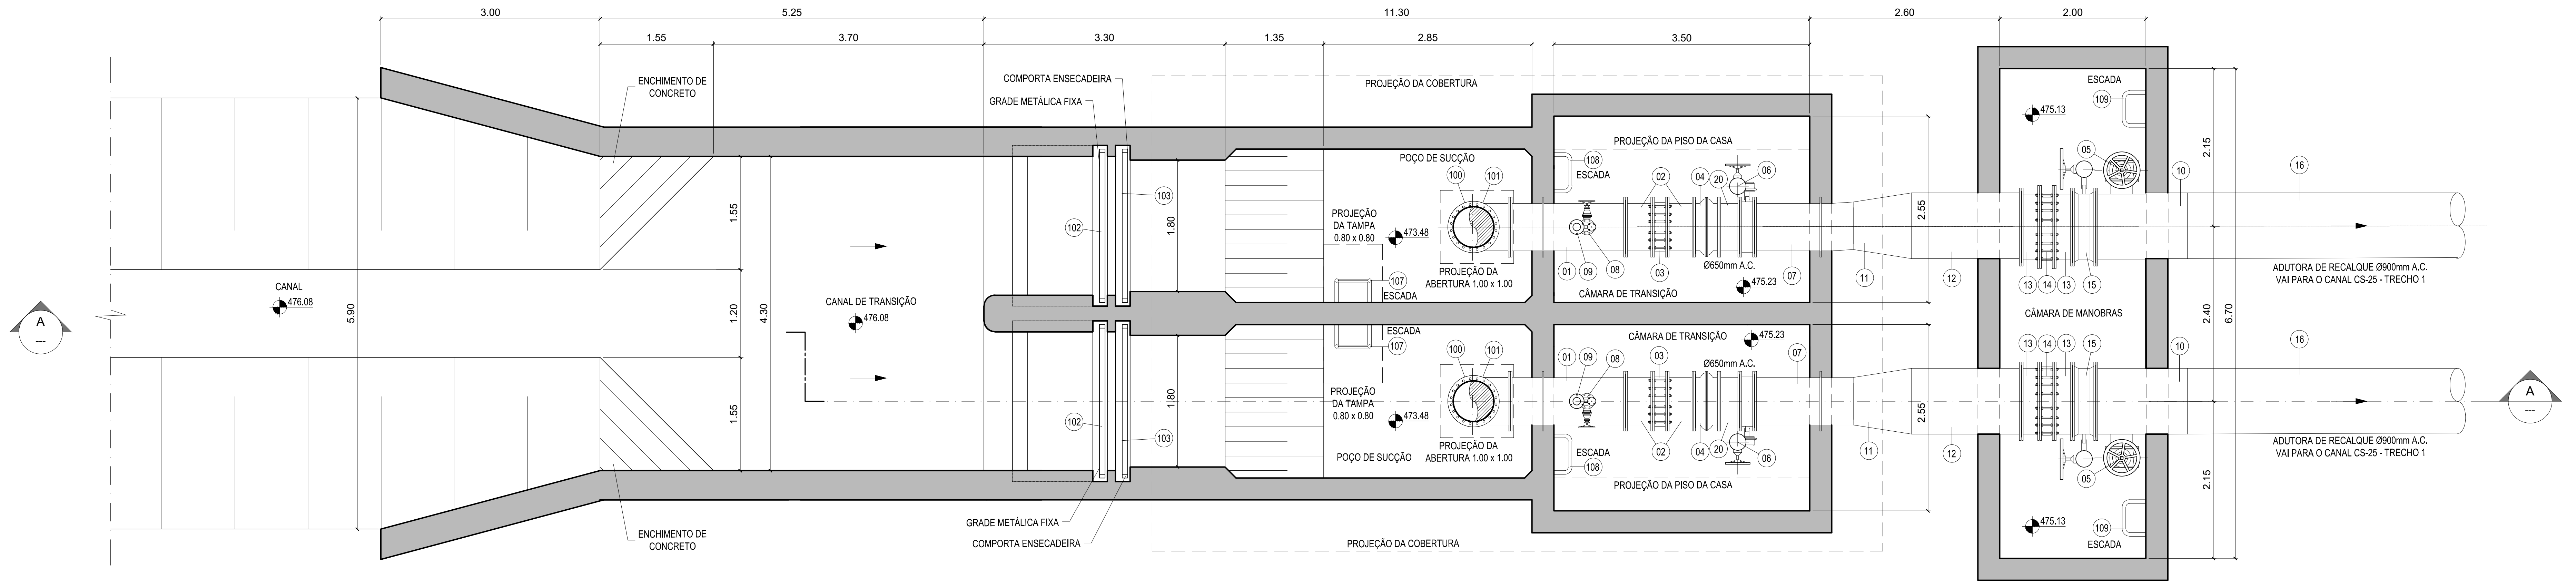
3.00
5.25
11.30
2.60
2.00
1.55
3.70
3.30
1.35
2.85
3.50
ENCHIMENTO DE CONCRETO
COMPORTA ENSECADEIRA
GRADE METÁLICA FIXA
PROJEÇÃO DA COBERTURA
PROJEÇÃO DA PISO DA CASA
POÇO DE SUCÇÃO
100
101
102
103
108
ESCADA
107
PROJEÇÃO DA TAMPA 0.80 x 0.80
473.48
PROJEÇÃO DA ABERTURA 1.00 x 1.00
01 09 08 03 02 04 20 06 07
Ø650mm A.C.
475.23
CÂMARA DE TRANSIÇÃO
11
12
1.80
2.55
CANAL
476.08
5.90
CANAL DE TRANSIÇÃO
476.08
1.55
1.20
4.30
1.55
ESCADA
109
475.13
05
13 14 13 15
10
16
CÂMARA DE MANOBRAS
2.15
2.40
6.70
2.15
ADUTORA DE RECALQUE Ø900mm A.C.
VAI PARA O CANAL CS-25 - TRECHO 1
ADUTORA DE RECALQUE Ø900mm A.C.
VAI PARA O CANAL CS-25 - TRECHO 1
POÇO DE SUCÇÃO
GRADE METÁLICA FIXA
COMPORTA ENSECADEIRA
ENCHIMENTO DE CONCRETO
PROJEÇÃO DA COBERTURA
A

PLANTA INFERIOR

ESC. 1:50

NOTAS :

1. MEDIDAS E COTAS EM METROS E DIÂMETROS EM MILÍMETROS, EXCETO COM INDICAÇÃO CONTRÁRIA.
2. TODAS AS MEDIDAS DEVERÃO SER VERIFICADAS NO LOCAL.
3. PARA ESPECIFICAÇÕES DE EQUIPAMENTOS E INSTRUMENTOS VER DOCUMENTO ESPECÍFICO. PARA LISTAS DE MATERIAIS VER ISOMÉTRICO ESPECÍFICO.
4. O FORNECEDOR DOS EQUIPAMENTOS DEVERÃO ANALISAR OS DESENHOS DE HIDROMECÂNICA E ESTRUTURAS E APONTAR EVENTUAIS AJUSTES QUE SE FIZEREM NECESSÁRIOS, PARA O PERFEITO FUNCIONAMENTO DE TODOS OS COM PONENTES DI SISTEMA.
5. DETALHES CONSTRUTIVOS ESPECÍFICOS DE CALDERARIA E MECÂNICA PARA PEÇAS ESPECIAIS E SUPORTES DEVERÃO SER DEFINIDOS NA OCASIÃO DAS OBRAS PELO FORNECEDOR.

Revisão	Data	Descrição	Elab.	Verif.	Aprov.	Aut.
0	11/2025	Emissão Inicial	DGC	AHL	EDK	-

FUNDO DE DESENVOLVIMENTO DA INFRAESTRUTURA
REGIONAL SUSTENTÁVEL - FDIRS

ESTRUTURAÇÃO DE PROJETO DE CONCESSÃO DO
PERÍMETRO IRRIGADO DO JAÍBA (ETAPAS 3 E 4)

ANTEPROJETO

ESTAÇÃO DE RECALQUE ER4
ETAPA 4
PLANTAS

Finalidade de Emissão	1 Para Informação	2 Para Comentários	▨ Para Aprovação	4 Para Execução	5 Como Construído	6 Para Utilização	7 Para Providências

Moysés & Pires
ENGECORPS
Plena Consultoria e Projetos

Data: 11/2025
Elaboração:
Verificação:
Escala: INDICADAS
Aprovação
Autorização
Referência:
Revisão:
Desenho nº J4-DS-HI-0009-00