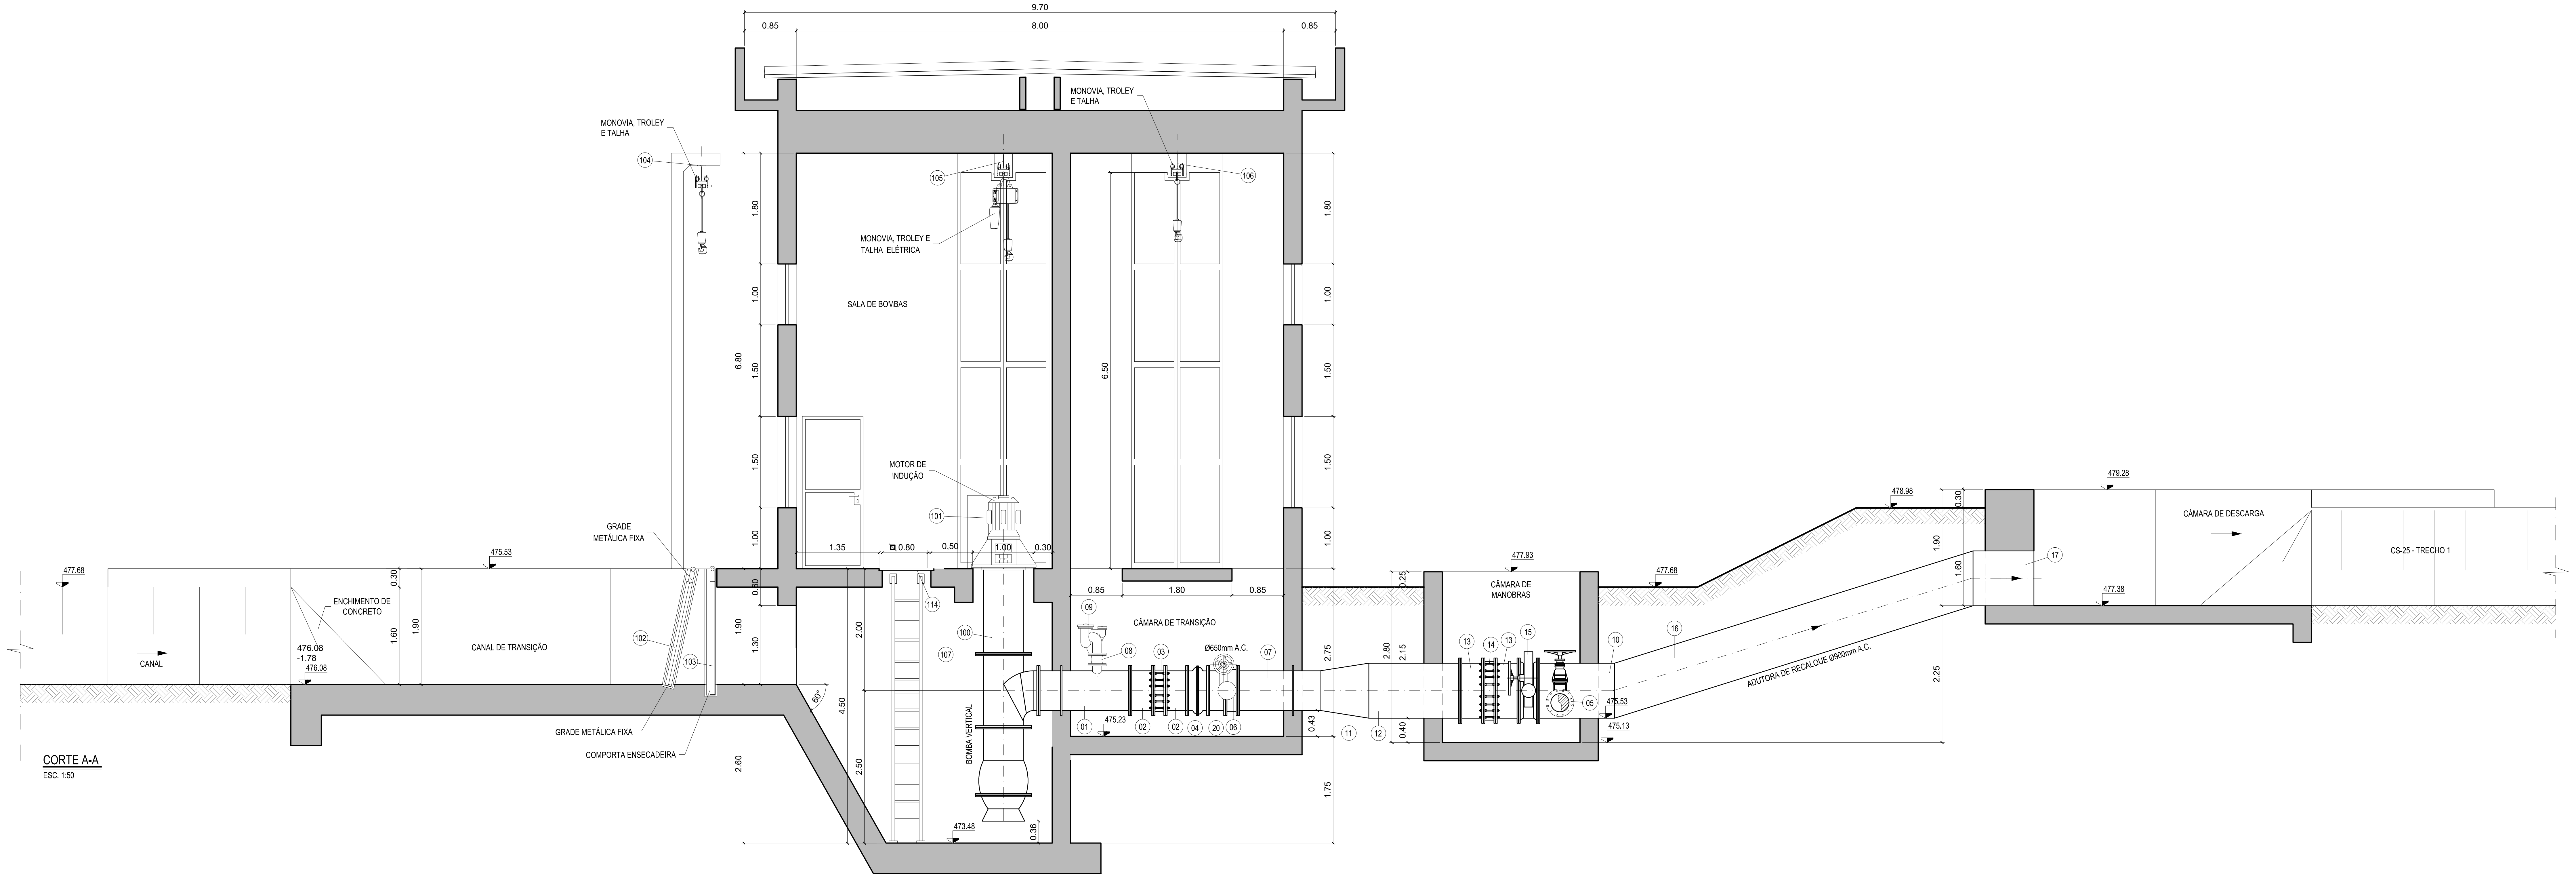
9.70
0.85
8.00
0.85
MONOVIA, TROLEY E TALHA
104
MONOVIA, TROLEY E TALHA
105
106
MONOVIA, TROLEY E TALHA ELÉTRICA
SALA DE BOMBAS
MOTOR DE INDUÇÃO
101
6.80
6.50
1.80
1.00
1.50
1.50
1.00
0.60
1.90
1.30
2.60
1.35
0.80
0,50
1.00
0.30
114
GRADE METÁLICA FIXA
477.68
475.53
ENCHIMENTO DE CONCRETO
476.08
-1.78
476.08
CANAL
CANAL DE TRANSIÇÃO
0.30
1.60
1.90
102
103
GRADE METÁLICA FIXA
COMPORTA ENSECADEIRA
60°
2.00
4.50
2.50
100
107
BOMBA VERTICAL
473.48
0.36
0.85
1.80
0.85
CÂMARA DE TRANSIÇÃO
09
08
03
Ø650mm A.C.
07
01
475.23
02
02
04
20
06
2.75
0.43
1.75
11
12
0.25
2.80
2.15
0.40
477.93
CÂMARA DE MANOBRAS
13
14
13
15
10
05
475.53
475.13
477.68
16
ADUTORA DE RECALQUE Ø900mm A.C.
478.98
0.30
1.90
1.60
2.25
17
479.28
CÂMARA DE DESCARGA
477.38
CS-25 - TRECHO 1

CORTE A-A
ESC. 1:50

NOTAS :

1. MEDIDAS E COTAS EM METROS E DIÂMETROS EM MILÍMETROS, EXCETO COM INDICAÇÃO CONTRÁRIA.
2. TODAS AS MEDIDAS DEVERÃO SER VERIFICADAS NO LOCAL.
3. PARA ESPECIFICAÇÕES DE EQUIPAMENTOS E INSTRUMENTOS VER DOCUMENTO ESPECÍFICO. PARA LISTAS DE MATERIAIS VER ISOMÉTRICO ESPECÍFICO.
4. O FORNECEDOR DOS EQUIPAMENTOS DEVERÃO ANALISAR OS DESENHOS DE HIDROMECÂNICA E ESTRUTURAS E APONTAR EVENTUAIS AJUSTES QUE SE FIZEREM NECESSÁRIOS, PARA O PERFEITO FUNCIONAMENTO DE TODOS OS COM PONENTES DI SISTEMA.
5. DETALHES CONSTRUTIVOS ESPECÍFICOS DE CALDERARIA E MECÂNICA PARA PEÇAS ESPECIAIS E SUPORTES DEVERÃO SER DEFINIDOS NA OCASIÃO DAS OBRAS PELO FORNECEDOR.

QUADRO DE EQUIPAMENTOS DA ELEVATÓRIA

N°	DISCRIMINAÇÃO	MATERIAL	CAP.	ER M1 Ø/L/H(mm)	UNID.	QUANTIDADE
100	BOMBA VERTICAL	--	--	--	CJ	02
101	MOTOR DE INDUÇÃO P/ BOMBA VERTICAL	--	--	--	CJ	02
102	GRADE METÁLICA FIXA	AÇO	--	2.15x1.90	PÇ	02
103	COMPORTA ENSECADEIRA	AÇO	--	2.15x1.90	PÇ	02
104	MONOVIA COM TROLHE E TALHA, PERFIL "I" #4"x15"	AÇO	3ton.	6.500	CJ	01
105	MONOVIA COM TROLHE E TALHA ELÉTRICA, PERFIL "I" #4"x15"	AÇO	5ton.	6.500	CJ	01
106	MONOVIA COM TROLHE E TALHA, PERFIL "I" #4"x15"	AÇO	5ton.	6.500	CJ	01
107	ESCADA MARINHEIRO	AÇO	--	4.500	PÇ	02
108	ESCADA MARINHEIRO	AÇO	--	2.750	PÇ	02
109	ESCADA MARINHEIRO	AÇO	--	2.800	PÇ	02
110	TAMPA	PRFV	--	0.80x0.80	PÇ	02

QUADRO DE TUBULAÇÕES E CONEXÕES DA ELEVATÓRIA – PARTE 1

N°	DISCRIMINAÇÃO	MATERIAL	CHAPA	ER M1		UNID.	QUANTIDADE
				DN(mm)	L(mm)		
01	TUBO COM DERIVAÇÃO, FLANGES E ABA DE VEDAÇÃO	AÇO	#7,1mm	650 x 150	1.500	PÇ	02
02	TOCO COM FLANGE E PONTA	AÇO	#7,1mm	650	450	PÇ	04
03	JUNTA DE DESMONTAGEM TRAVADA AXIALMENTE	AÇO	#7,1mm	650	--	PÇ	02
04	VÁLVULA DE RETENÇÃO COM FLANGES (CLASAR)	F°F°	--	650	--	PÇ	02
05	REGISTRO DE GAVETA COM FLANGES, SÉRIE CHATA	F°F°	--	300	--	PÇ	02
06	VÁLVULA BORBOLETA, ACIONAMENTO ELÉTRICO	F°F°	--	650	--	PÇ	02
07	TUBO COM FLANGE, PONTA E ABA DE VEDAÇÃO	AÇO	#7,1mm	650	1.350	PÇ	02
08	REGISTRO DE GAVETA, SÉRIE CHATA	F°F°	--	150	--	PÇ	02
09	VENTOSA DE TRÍPLICE FUNÇÃO	F°F°	--	150	--	PÇ	02
10	TUBO COM DERIVAÇÃO, FLANGES E PONTA	AÇO	#7,1mm	900 x 300	1.250	PÇ	02
11	REDUÇÃO CONCÊNTRICA COM PONTAS	AÇO	#7,1mm	900 x 650	800	PÇ	02
12	TUBO COM FLANGE E PONTA	AÇO	#7,1mm	900	1.500	PÇ	02
13	TOCO COM FLANGE E PONTA	AÇO	#7,1mm	900	350	PÇ	04
14	JUNTA DE DESMONTAGEM TRAVADA AXIALMENTE	AÇO	#7,1mm	900	--	PÇ	02
15	VÁLVULA BORBOLETA, ACIONAMENTO MANUAL	F°F°	--	900	--	PÇ	02
16	TUBO COM PONTAS PARA SOLDA	AÇO	#7,1mm	900	6.000	PÇ	02
17	TUBO COM PONTA PARA SOLDA	AÇO	#7,1mm	900	1.000	PÇ	02
20	TOCO COM FLANGES	AÇO	#7,1mm	650	300	PÇ	02

Revisão	Data	Descrição	Elab.	Verif.	Aprov.	Aut.
0	11/2025	Emissão Inicial	DGC	AHL	EDK	-

FUNDO DE DESENVOLVIMENTO DA INFRAESTRUTURA
REGIONAL SUSTENTÁVEL - FDIRS

ESTRUTURAÇÃO DE PROJETO DE CONCESSÃO DO
PERÍMETRO IRRIGADO DO JAÍBA (ETAPAS 3 E 4)

ANTEPROJETO

ESTAÇÃO DE RECALQUE ER4
ETAPA 4
CORTE E LISTAS DE MATERIAIS

Finalidade de Emissão	1 Para Informação	2 Para COM entários	☒ 3 Para Aprovação	4 Para Execução	5 COM o Construído	6 Para Utilização	7 Para Providências

Data: 11/2025
Escala: INDICADAS
Elaboração:
Verificação:
Aprovação
Autorização
Referência:
Revisão:
Desenho nº J4-DS-HI-0009-00