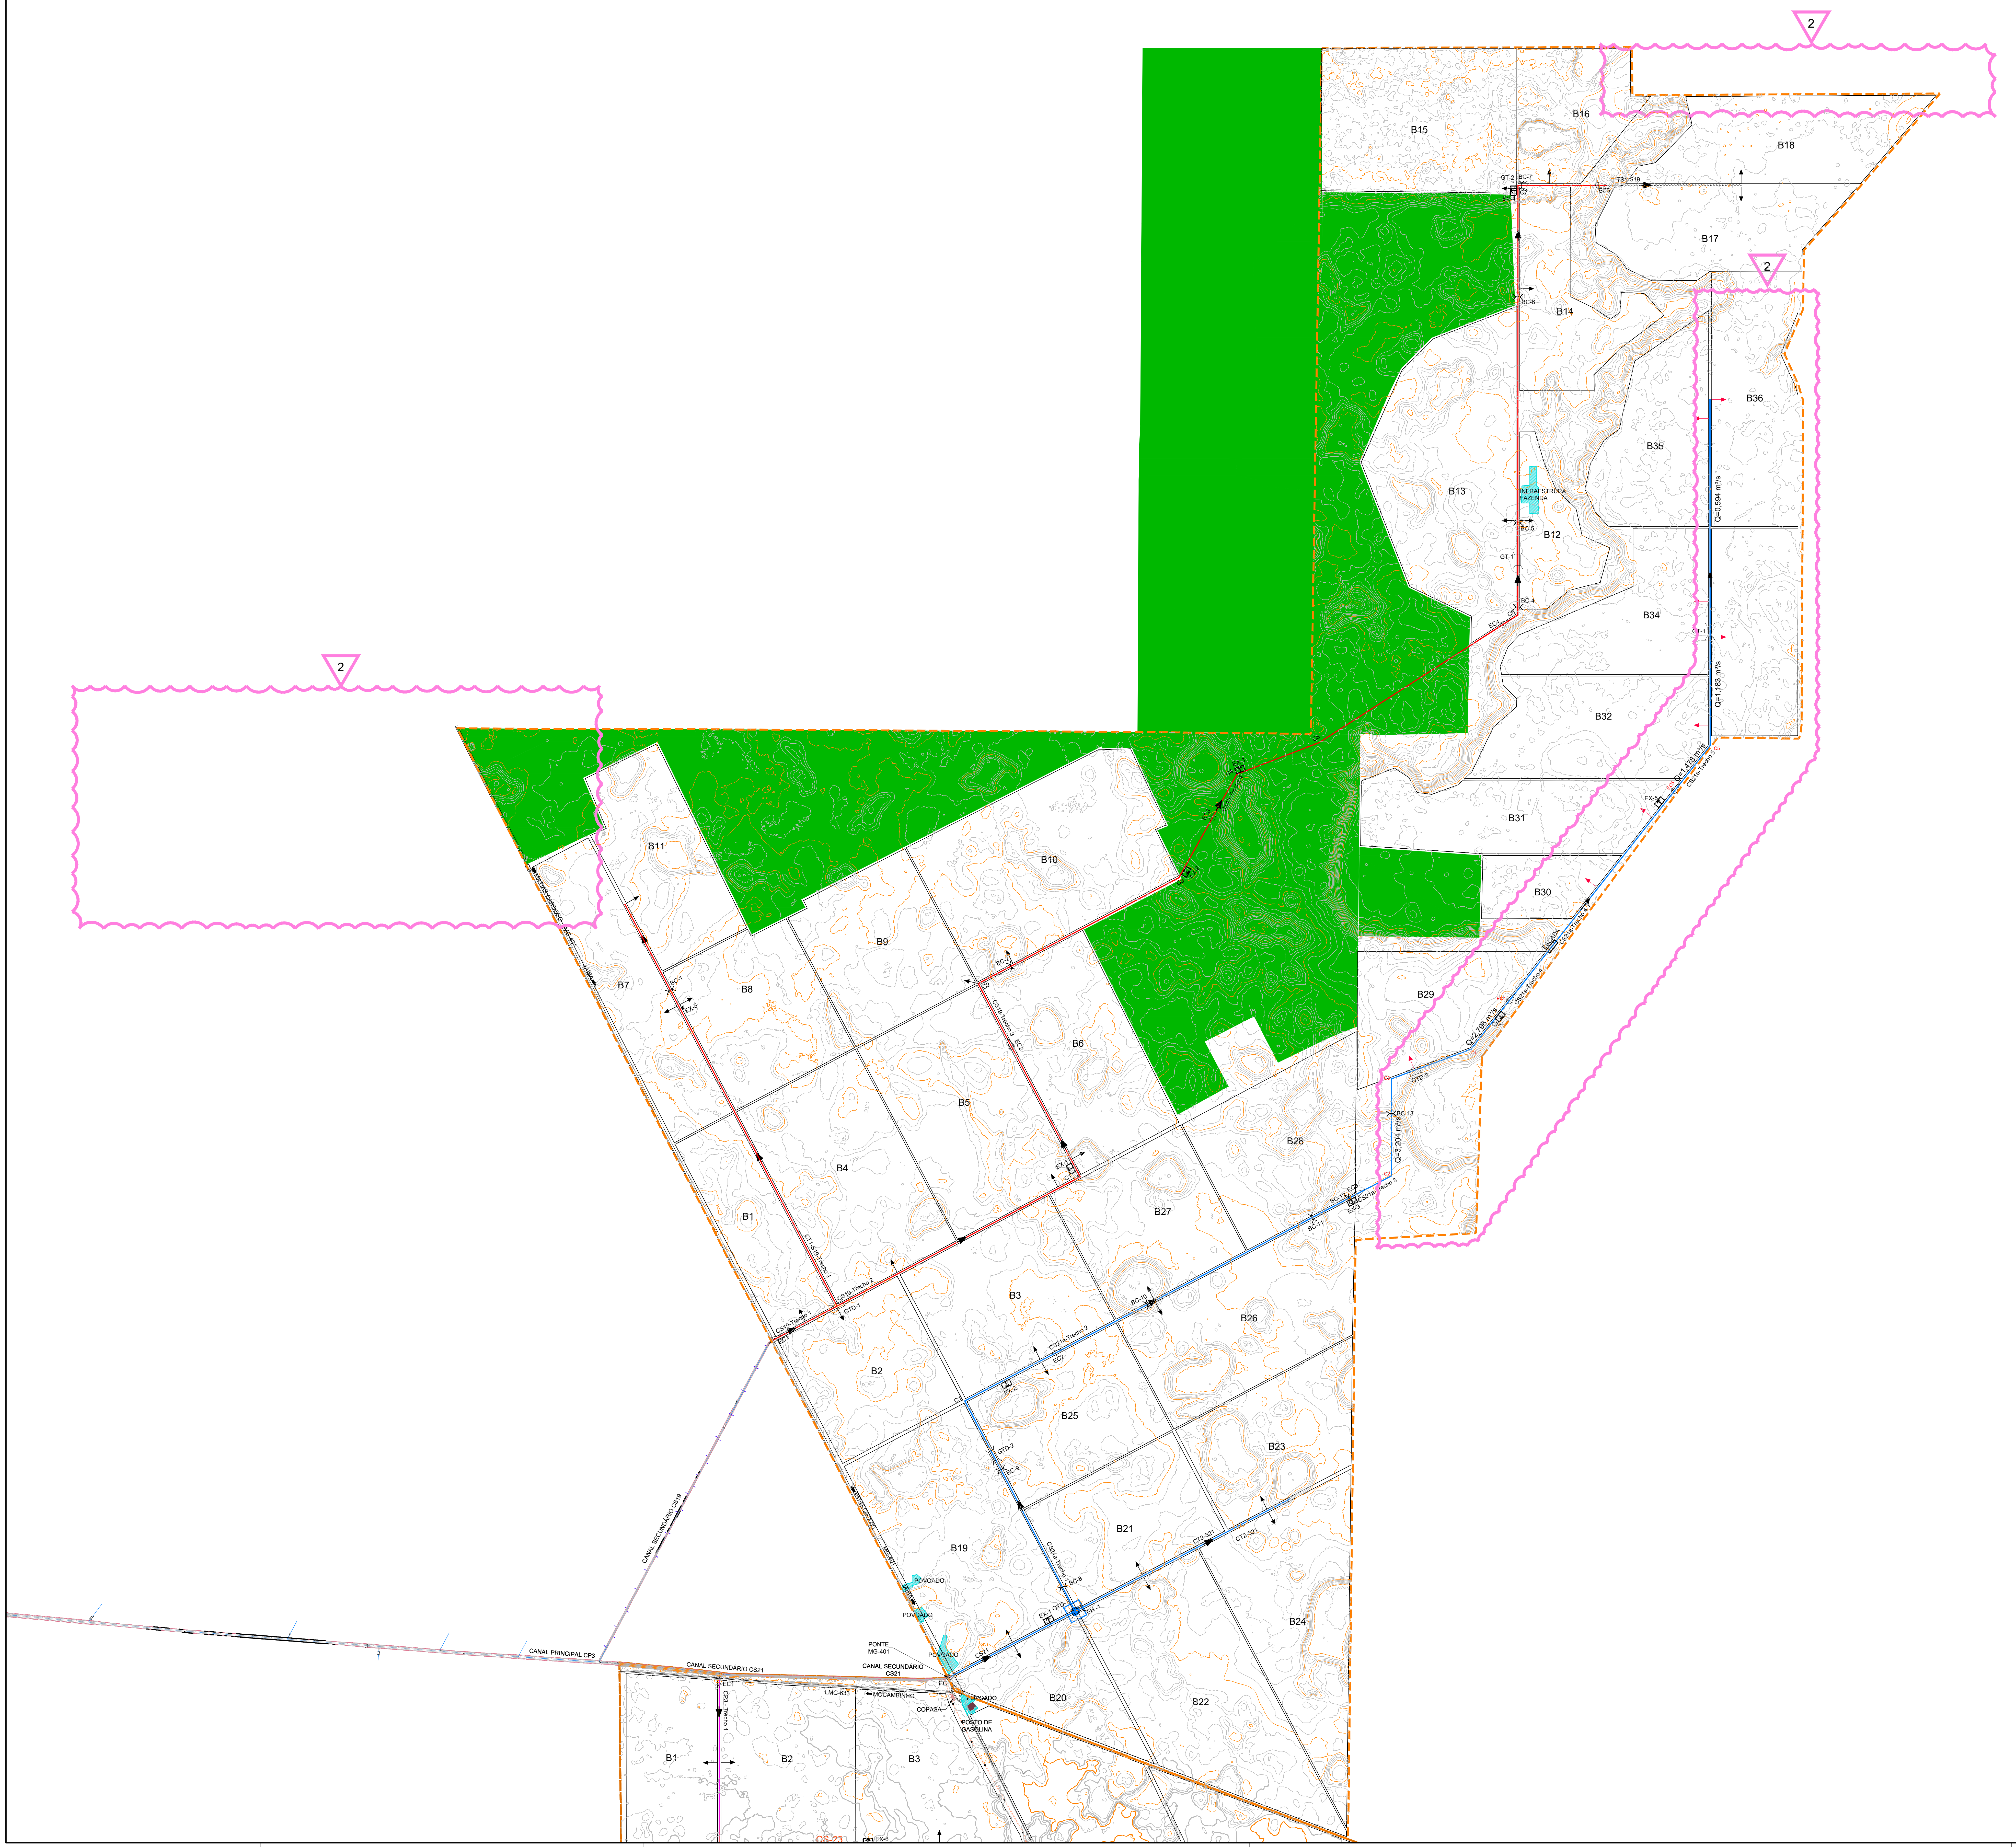
2
2
2
B1
B2
B3
B4
B5
B6
B7
B8
B9
B10
B11
B12
B13
B14
B15
B16
B17
B18
B19
B20
B21
B22
B23
B24
B25
B26
B27
B28
B29
B30
B31
B32
B34
B35
B36
INFRAESTRUTURA FAZENDA
Q=0,594 m³/s
Q=1,183 m³/s
Q=3,204 m³/s
CANAL PRINCIPAL CP3
CANAL SECUNDÁRIO CS21
CANAL SECUNDÁRIO CS19
PONTE MG-401
POVOADO
POSTO DE GASOLINA
COPASA
MOCAMBINHO
LMG-633
CS-23

LEGENDA:

‐ ‐ ‐	LIMITE - JAÍBA III
—	CANAL ADUTOR - CS-19
—	CANAL ADUTOR - CS-21
🟩	ÁREAS AMBIENTAIS SENSÍVEIS
●	ELEVATÓRIA DE RECALQUE
➤	SENTIDO DE ESCOAMENTO
∼	CURVAS DE NÍVEL A CADA METRO
	ESTRURA DE CONTROLE
	GALERIA
●	ESTAÇÃO DE RECALQUE
	EXTRAVASOR LATERAL
	TRANSIÇÃO CANAL X TUBULAÇÃO
	TUBULAÇÃO
	SIFÃO INVERTIDO
↑	TOMADA D'ÁGUA PARCELAR
	CANAL TIPO ESCADA
	BUEIRO
▽	IDENTIFICAÇÃO DA REVISÃO

NOTAS:

1 - MEDIDAS, COORDENADAS E ELEVAÇÕES EM METRO.

REVISÕES:

REVISÃO 2 - REVISÃO DO PERÍMETRO IRRIGÁVEL DA ETAPA 3, CONFORME SOLICITAÇÕES FEITAS APÓS CONSULTA PÚBLICA

Revisão	Data	Descrição	Elab.	Verif.	Aprov.	Aut.
2	06/07/26	REVISÃO DO PERÍMETRO DE IRRIGAÇÃO DA ETAPA 3	NP	AHL	EDK	
1	02/12/25	INSERÇÃO DAS GALERIAS DE TRANSPOSIÇÃO	NP	AHL	EDK	
0	19/11/25	EMISSÃO INICIAL	NP	AHL	EDK	

FUNDO DE DESENVOLVIMENTO DA INFRAESTRUTURA
REGIONAL SUSTENTÁVEL - FDIRS

ESTRUTURAÇÃO DE PROJETO DE CONCESSÃO DO PERÍMETRO IRRIGADO DO JAÍBA (ETAPAS 3 E 4)

ANTEPROJETO

ARRANJO GERAL

DA ETAPA 3

Finalidade de Emissão: ☐ 1 Para Informação ☐ 2 Para Comentários ☒ 3 Para Aprovação ☐ 4 Para Execução ☐ 5 Como Construído ☐ 6 Para Utilização ☐ 7 Para Providências

Data: 06/07/26	Elaboração:		Verificação:
Escala: sem escala	Aprovação	. .	Autorização . .
Referência:	Revisão: 2	Desenho nº	J3-DS-GR-0003