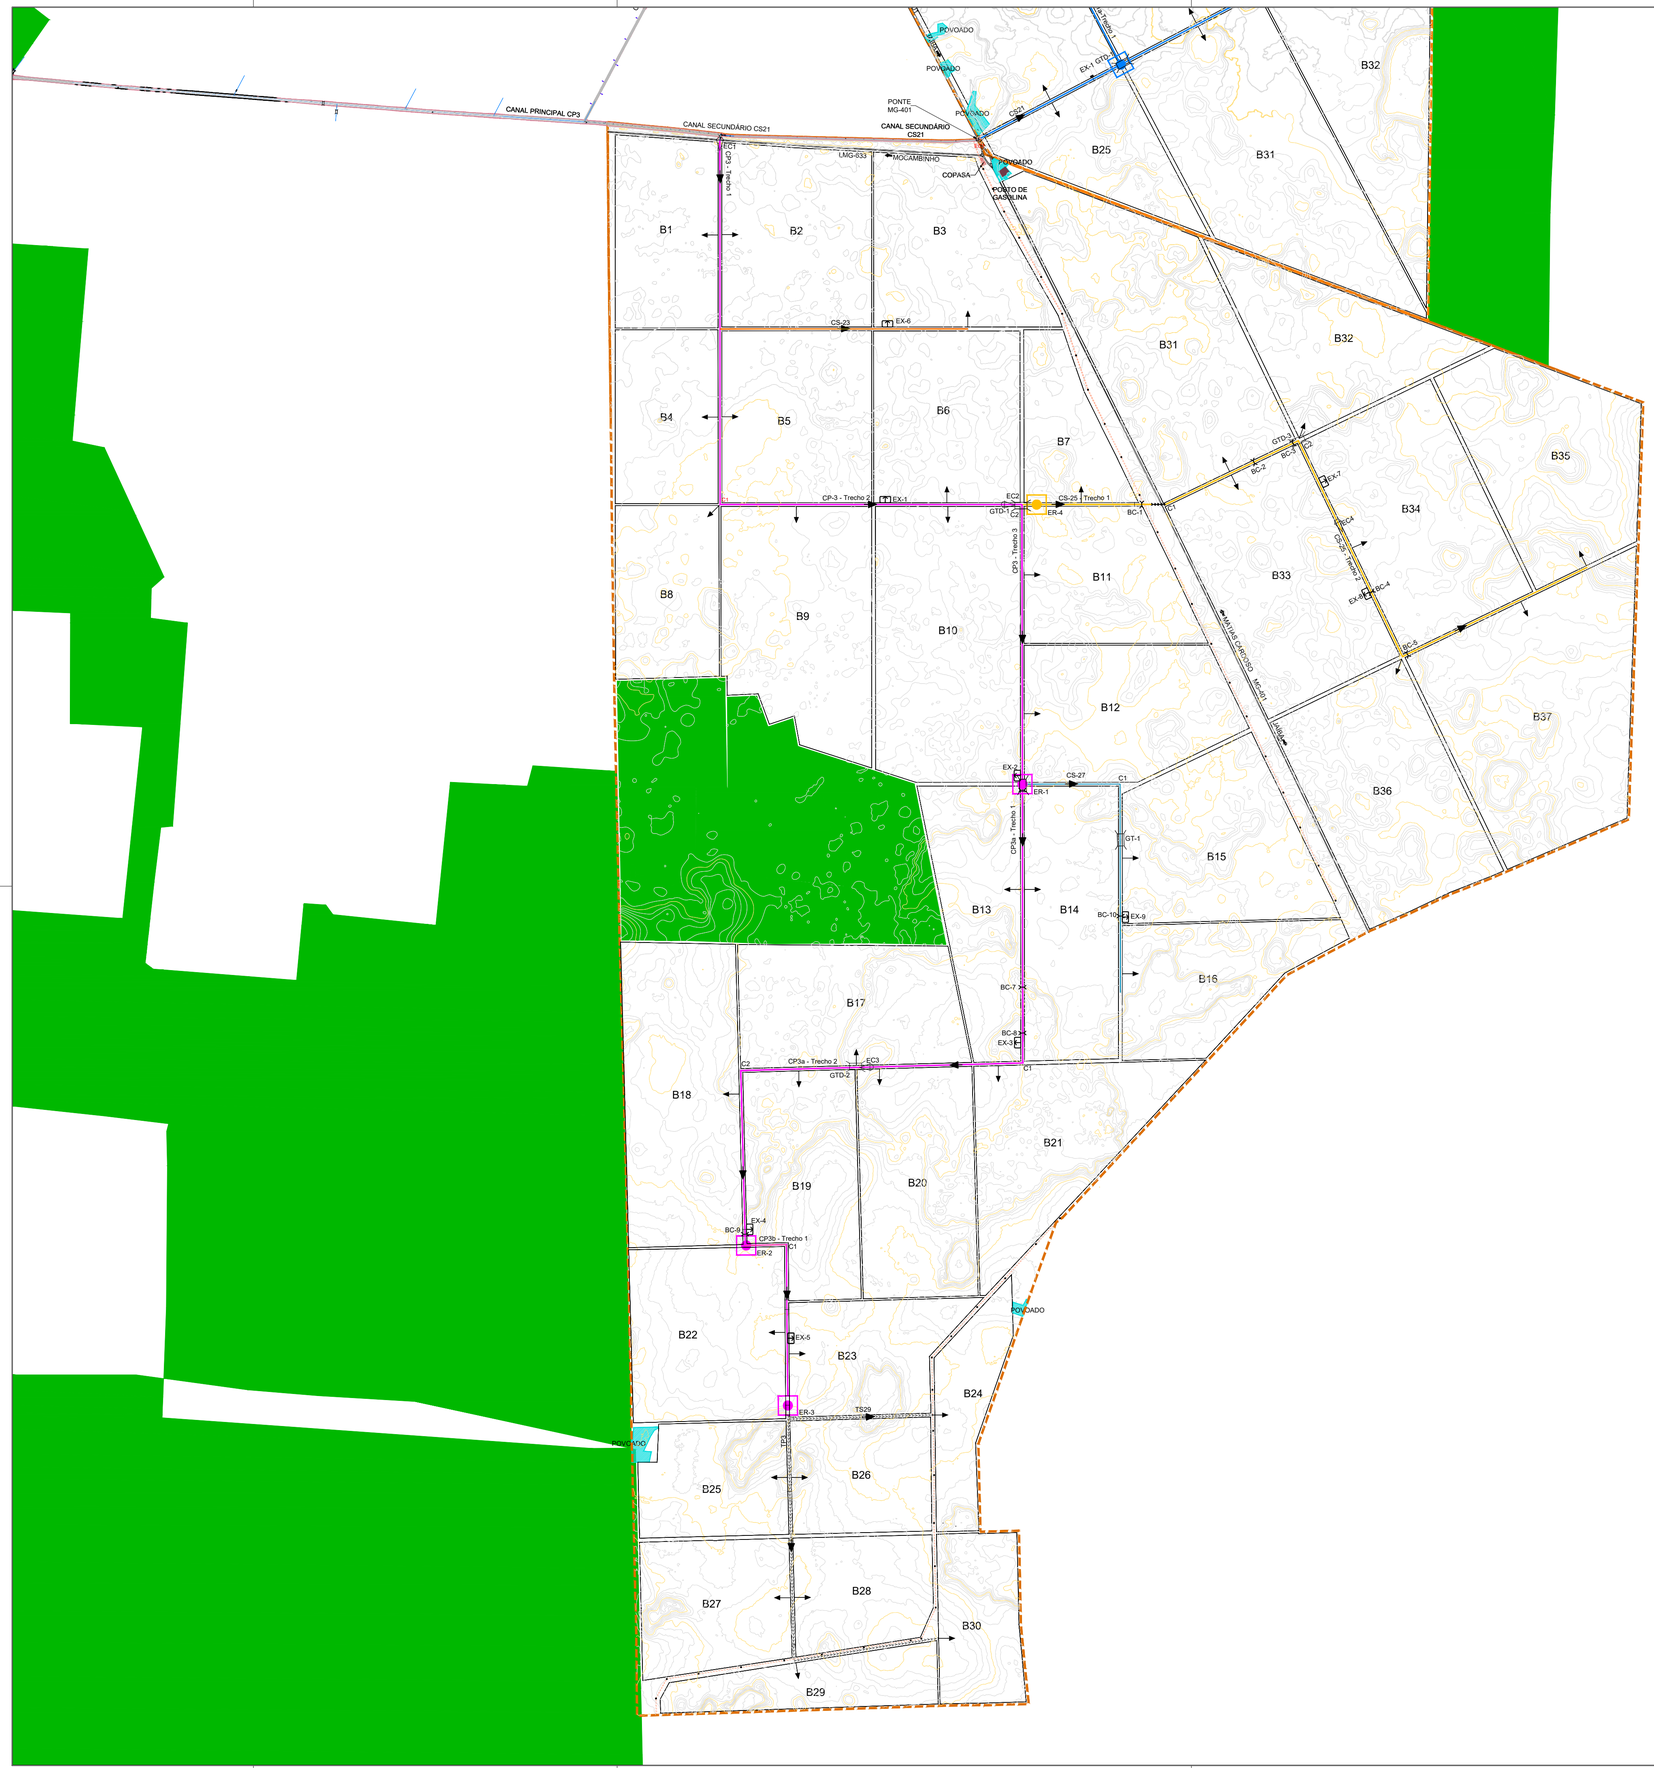


LEGENDA:

- LIMITE - JAÍBA IV
- CANAL ADUTOR - CP-3
- CANAL ADUTOR - CS-23
- CANAL ADUTOR - CS-25
- CANAL ADUTOR - CS-27
- CANAL ADUTOR - CS-29
- ÁREAS AMBIENTAIS SENSÍVEIS
- ELEVATÓRIA DE RECALQUE (ER)
- SENTIDO DE ESCOAMENTO
- CURVAS DE NÍVEL A CADA METRO
- COMPORTA
- GALERIA
- ESTAÇÃO DE RECALQUE
- EXTRAVASOR LATERAL
- TRANSIÇÃO CANAL X TUBULAÇÃO
- TUBULAÇÃO
- SIFÃO INVERTIDO
- TOMADA D'ÁGUA PARCELAR
- BUEIRO

NOTAS:

1 - VAZÃO NA PARCELA EM L/S

2 - VAZÃO NO CANAL EM M³/S

Revisão	Data	Descrição	Elab.	Verif.	Aprov.	Aut.
1	02/12/25	INSERÇÃO DAS GALERIAS DE TRANSPOSIÇÃO	NP	AHL	EDK	
0	19/11/25	EMISSÃO INICIAL	NP	AHL	EDK	

FUNDO DE DESENVOLVIMENTO DA INFRAESTRUTURA REGIONAL SUSTENTÁVEL - FDIRS

ESTRUTURAÇÃO DE PROJETO DE CONCESSÃO DO PERÍMETRO IRRIGADO DO JAÍBA (ETAPAS 3 E 4)

ANTEPROJETO

ARRANJO GERAL

DA ETAPA 4

Finalidade de Emissão	1 Para Informação	2 Para Comentários	Para Aprovação	4 Para Execução	5 Como Construído	6 Para Utilização	7 Para Providências

Moysés & Pires Consultoria Ltda. | ENGECORPS Group | Plena Consultoria e Projetos

Data: 29/08/25 | Elaboração: | Verificação:

Escala: sem escala | Aprovação | Autorização

Referência: | Revisão: 0 | Desenho nº J4-DS-GR-0002