


SEÇÃO EM ATERRO

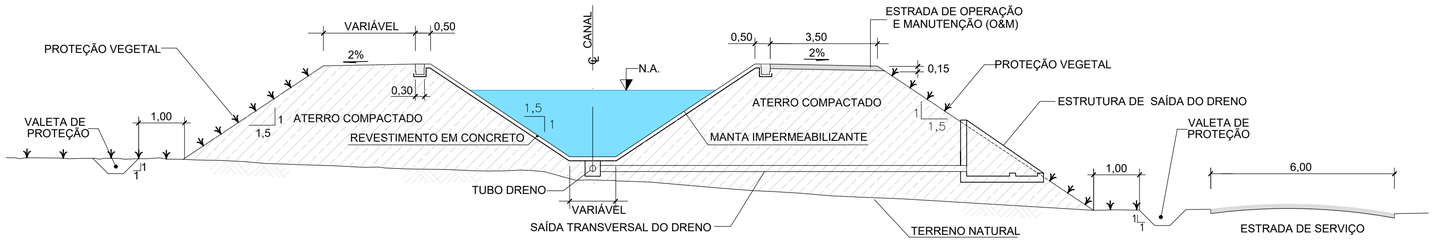


SEÇÃO EM CORTE

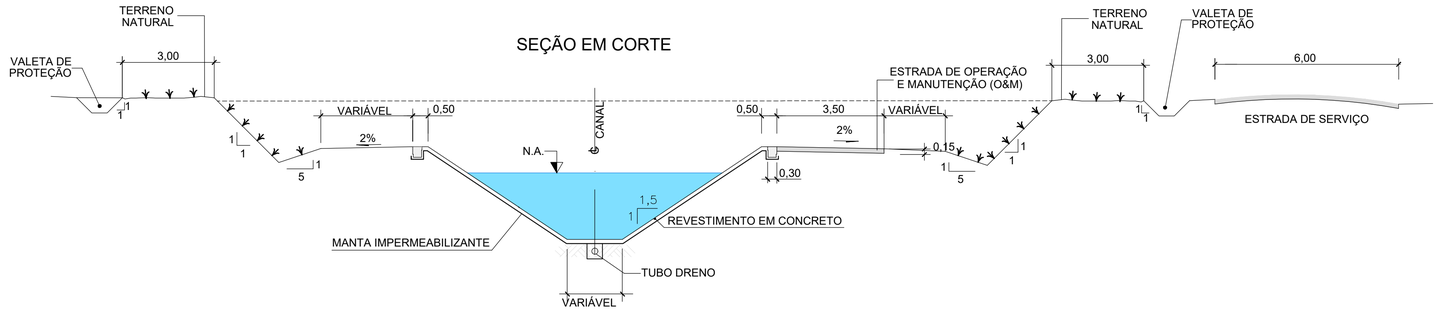


SEÇÃO MISTA

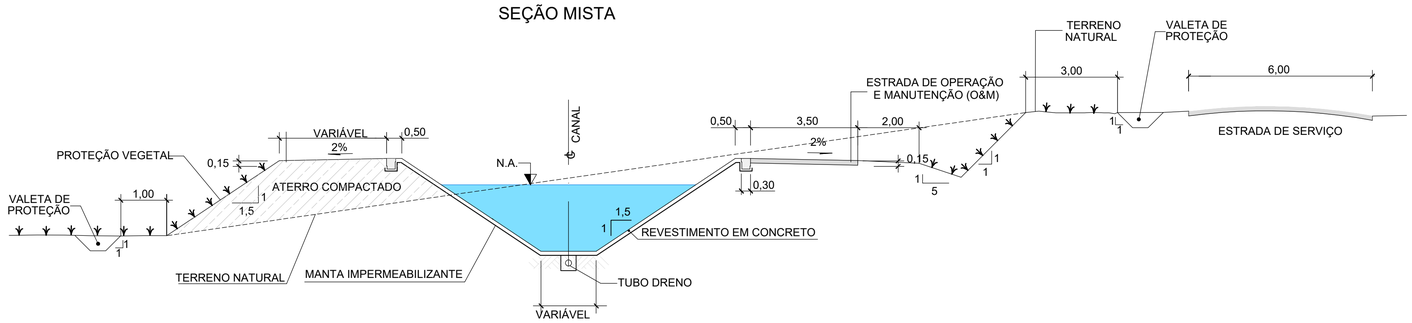

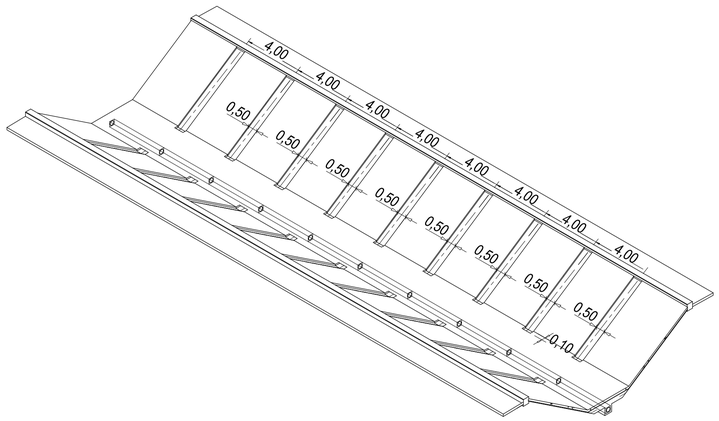

DRENOS TIPO "FINGER" - ISOMÉTRICO EM CORTE
SEM ESC.

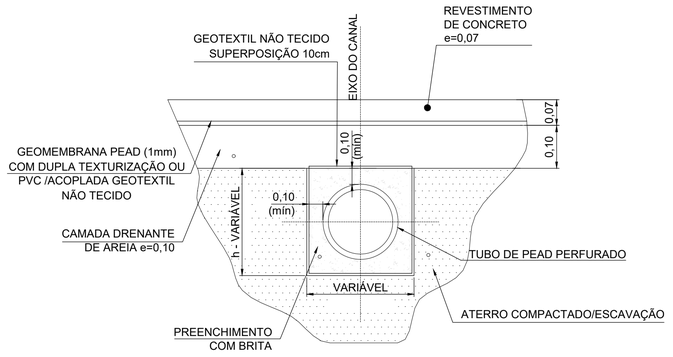

DETALHE DO DRENO LONGITUDINAL
SEM ESC.

DIÂMETRO NOMINAL TUBO DRENO (mm)	DIÂMETRO INTERNO TUBO DRENO (mm)	LARGURA DA VALA DE DRENAGEM INTERNA (M)	ALTURA DA VALA DE DRENAGEM INTERNA (M)
340	302	0,60	0,60

NOTAS:

1 - DIMENSÕES EM METROS.

2- PARA A FUNDAÇÃO DOS ATERROS DEVERÃO SER REMOVIDOS OS SOLOS ORGÂNICOS, COMPRESSÍVEIS E COLAPSÍVEIS.

3- CASO SEJAM EMPREGADOS MATERIAIS DE 3ª CATEGORIA NA EXECUÇÃO DO ATERRO COMPACTADO, DEVERÁ SER EXECUTADA UMA CAMADA DE TRANSIÇÃO NA INTERFACE ENTRE AS CAMADAS DE SOLO COMPACTADO E ENROCAMENTO COMPACTADO, EM ESPESSURA DE 0,30m.

4 - PARA O REVESTIMENTO DOS CANAIS DEVERÃO SER EMPREGADAS GEOMEMBRANAS DE PEAD TEXTURIZADA OU PVC ACOPLADA A GEOTÊXTIL.

5- AS GEOMEMBRANAS UTILIZADAS DEVERÃO ATENDER AOS CRITÉRIOS HIDRÁULICOS, MECÂNICOS E DE DESEMPENHO.

6- PREVIAMENTE À INSTALAÇÃO DA GEOMEMBRANA DEVERÁ SER PROMOVIDA A REGULARIZAÇÃO DA SUPERFÍCIE COM APLICAÇÃO DE SOLO-CIMENTO COMPACTADO MANUALMENTE.

7- PARA A ANCORAGEM DA GEOMEMBRANA DEVERÁ SER EXECUTADA UMA TRINCHEIRA NO TOPO DOS TALUDES E APÓS A ACOMADAÇÃO DA GEOMEMBRANA NO INTERIOR DA TRINCHEIRA, ESTA DEVERÁ SER PREENCHIDA COM SOLO COMPACTADO.

8- SOBRE A GEOMEMBRANA, PARA O REVESTIMENTO DOS CANAIS, DEVERÁ SER EXECUTADA UMA CAMADA DE CONCRETO QUE DEVERÁ APRESENTAR fck=15MPa AOS 28 DIAS.

9- EXECUTAR O DRENO NOS TALUDES APÓS REGULARIZAÇÃO COM SOLO COMPACTADO MANUALMENTE.

10 - O DESÁGUE DO DRENO LONGITUDINAL DEVERÁ FEITO COM TUBO NÃO PERFURADO COM O MESMO DIÂMETRO NOMINAL.

11 - A DRENAGEM DA ESTRUTURA DE SAÍDA NO PÉ DO ATERRO DEVERÁ SER ADAPTADA EM FUNÇÃO DAS CONDIÇÕES TOPOGRÁFICAS LOCAIS E DEVERÁ SER INTERLIGADA AO SISTEMA DE DRENAGEM EXTERNO DO CANAL.

12- NOS CASOS DE CORTE EM MATERIAL DE 2ª E 3ª CATEGORIA, A ESCAVAÇÃO DA VALA PARA DRENAGEM INTERNA DEVERÁ SER REGULARIZADA COM BRITA ANTES DA COLOCAÇÃO DO GEOTÊXTIL.

NOTAS:

1 - MEDIDAS EM METRO, EXCETO INDICAÇÃO CONTRÁRIA;

Revisão	Data	Descrição	Elab.	Verif.	Aprov.	Aut.
1	19/12/25	REVISÃO DO SISTEMA VIÁRIO	NP	AHL	EDK	
0	19/11/25	EMISSÃO INICIAL	NP	AHL	EDK	

FUNDO DE DESENVOLVIMENTO DA INFRAESTRUTURA REGIONAL SUSTENTÁVEL - FDIRS

ESTRUTURAÇÃO DE PROJETO DE CONCESSÃO DO PERÍMETRO IRRIGADO DO JAÍBA (ETAPAS 3 E 4)

ANTEPROJETO

SISTEMA ADUTOR

SEÇÕES TÍPICAS

Finalidade de Emissão	1 Para Informação	2 Para Comentários	Para Aprovação	4 Para Execução	5 Como Construído	6 Para Utilização	7 Para Providências

Data: -	Elaboração:	Verificação:	
Escala: sem escala	Aprovação -	Autorização -	-
Referência:	Revisão: 00	Desenho nº JA-DS-HI-0001	