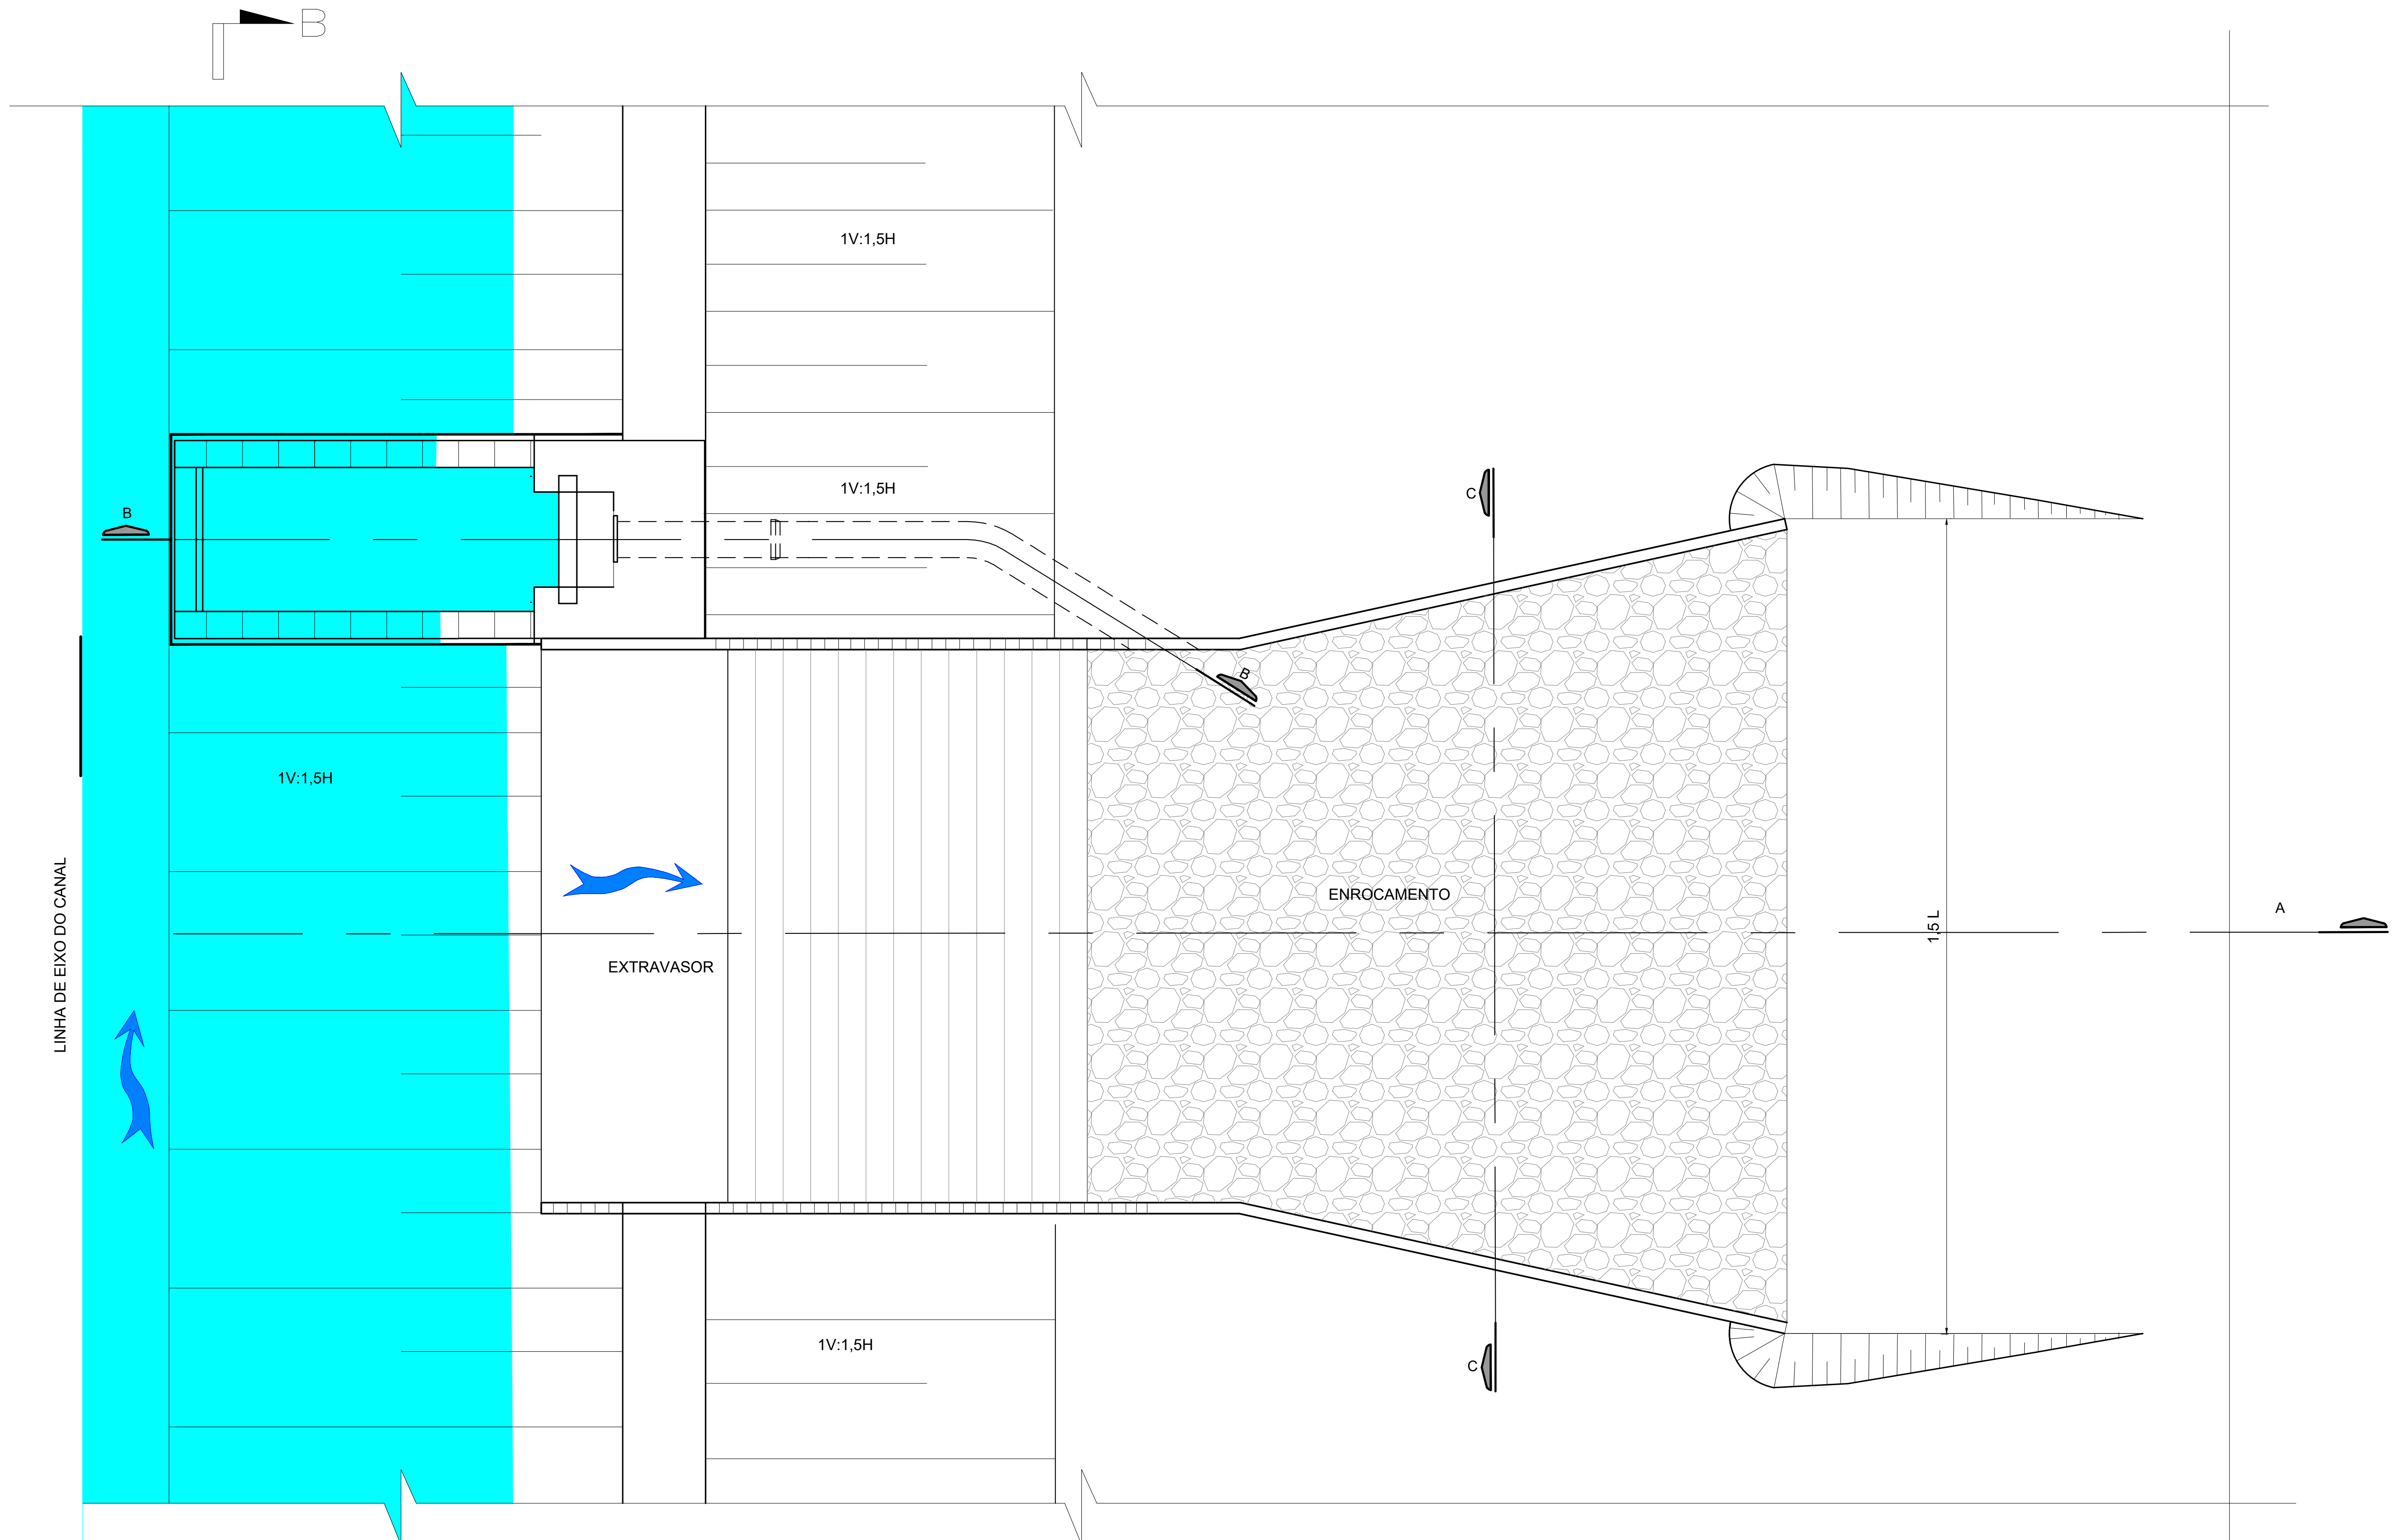
B
B
B
C
C
A
1V:1,5H
1V:1,5H
1V:1,5H
1V:1,5H
EXTRAVASOR
ENROCAMENTO
1,5 L
LINHA DE EIXO DO CANAL

PLANTA - ESTRAVASOR LATERAL
ESC.: 1:200

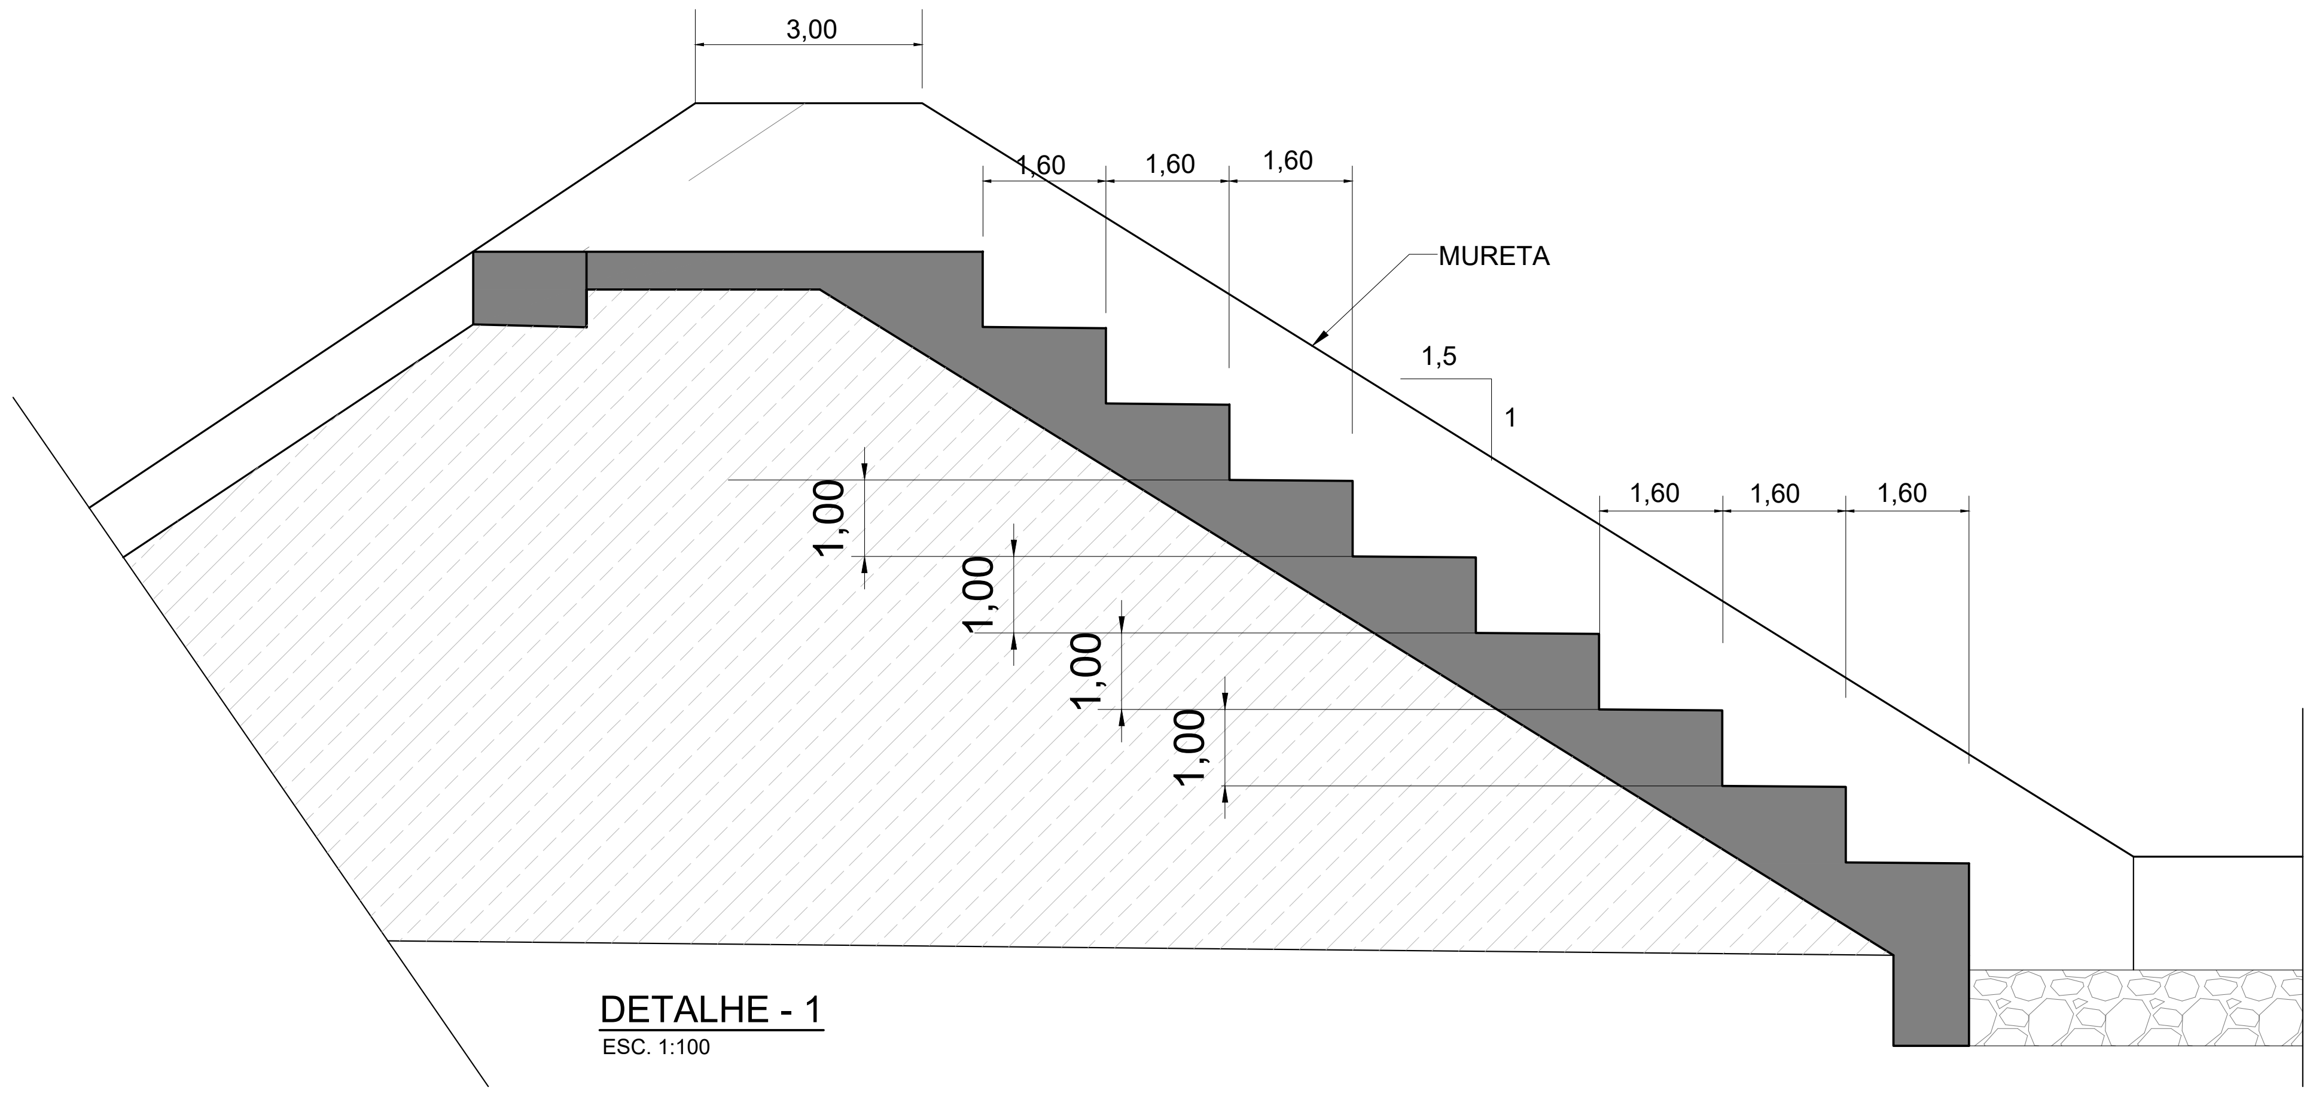
3,00
1,60
1,60
1,60
MURETA
1,5
1
1,60
1,60
1,60
1,00
1,00
1,00
1,00

DETALHE - 1
ESC. 1:100

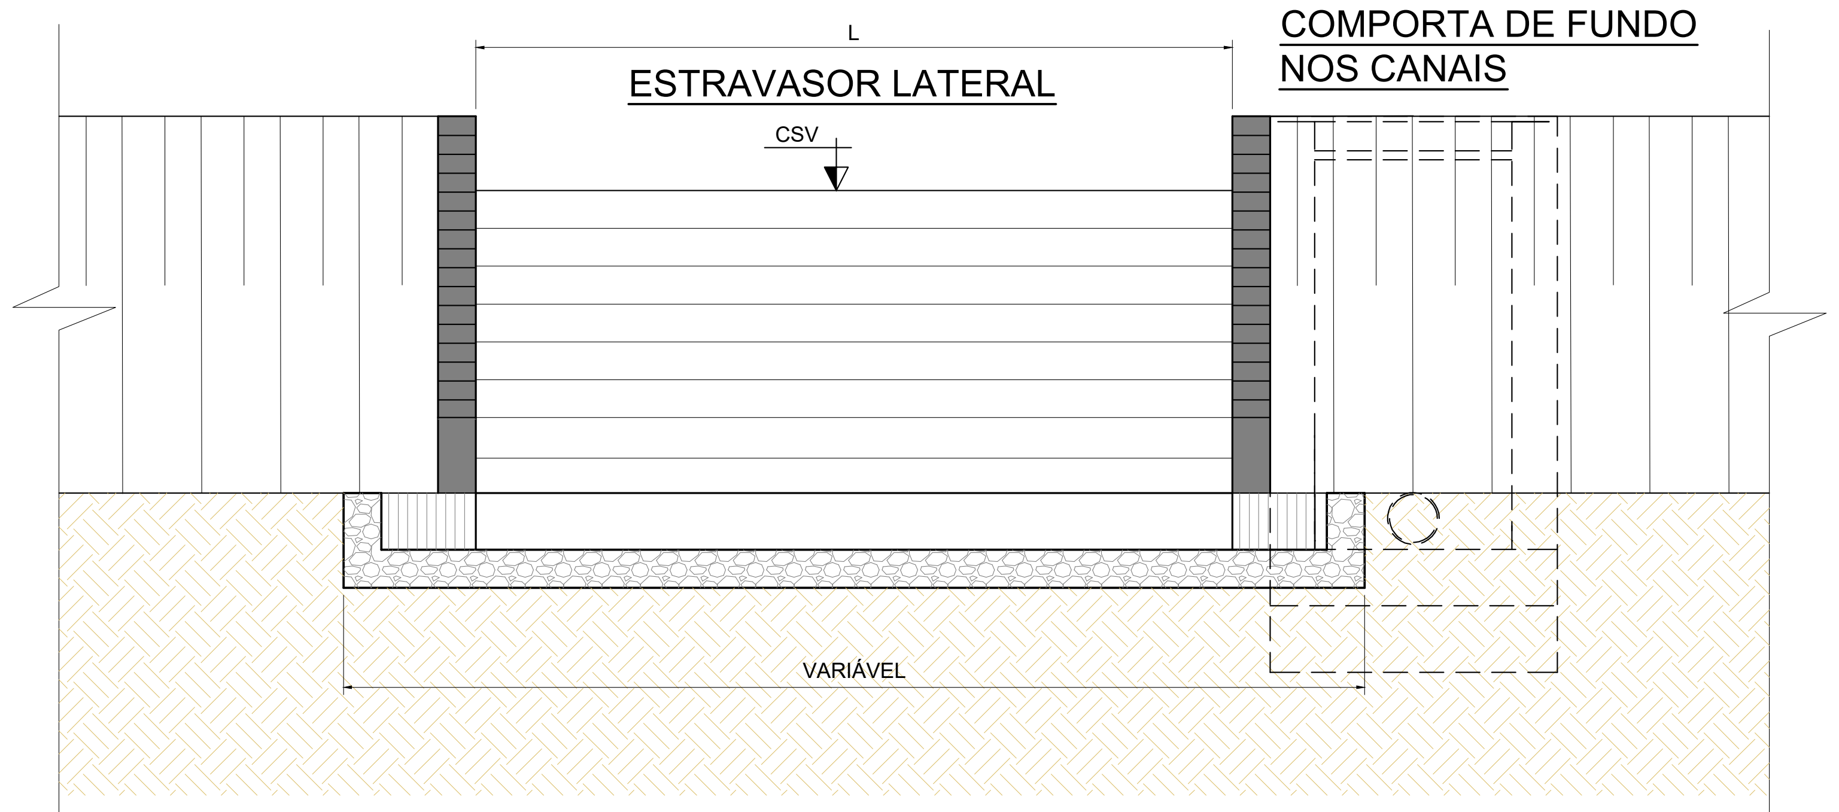
L
ESTRAVASOR LATERAL
COMPORTA DE FUNDO NOS CANAIS
CSV
VARIÁVEL

CORTE C - C
ESC. 1:200

Etapa	Obra	Trecho	Posição do extravasor (km+m)	Margem do canal (E/D)	Vazão no canal (m³/s)	NA estático (m)	Cota da soleira do extravasor (CSV) (m)	% da vazão do canal	Q extravasor (m³/s)	Comprimento do extravasor (L) (m)	Lâmina vertente (h) (m)	Cota da berma (m)
3	EX-1	CS19-Trecho 2	4+200	D	3,81	475,05	475,10	50%	1,91	20,50	0,15	475,35
	EX-2	CS19-Trecho 3	9+400	D	2,74	474,16	474,21	50%	1,37	14,80	0,15	474,41
	EX-3	CS19-Trecho 4	10+750	E	2,01	473,31	473,36	50%	1,00	10,80	0,15	473,56
	EX-4	CS19-Trecho 5	19+500	D	2,01	472,47	472,52	50%	1,00	10,80	0,15	472,72
	EX-5	CT1-CS19-Trecho 1	3+950	D	1,16	474,49	474,54	50%	0,58	6,20	0,15	474,74
	EX-6	CT1-CS19-Trecho 2	10+500	D	0,38	473,01	473,06	100%	0,38	4,10	0,15	473,21
3	EX-1	CS21	1+350	E	6,59	478,22	478,27	35%	2,31	24,90	0,15	478,52
	EX-2	CS21a - Trecho 1	3+300	D	4,73	479,98	480,03	35%	1,66	17,80	0,15	480,28
	EX-3	CS21a - Trecho 2	7+900	D	3,93	479,28	479,33	50%	1,97	21,20	0,15	479,53
	EX-4	CS21a - Trecho 3.1	11+700	E	2,81	463,76	463,81	50%	1,41	15,10	0,15	464,01
	EX-5	CS21a - Trecho 4	15+900	D	1,62	463,12	463,17	50%	0,81	8,70	0,15	463,37
	EX-6	CS21a - Trecho 5	0+021	D	1,62	462,18	462,23	50%	0,81	8,70	0,15	462,43
	CT2-S21		2+200	D	0,89	479,93	479,98	50%	0,45	4,80	0,15	480,18
4	EX-1	CP3 - Trecho 2	5+500	E	8,74	478,87	478,92	35%	3,06	33,00	0,15	479,17
	EX-2	CP3 - Trecho 3	9+750	D	4,42	477,83	477,88	35%	1,55	16,70	0,15	478,13
	EX-3	CP3a - Trecho 1	2+700	D	3,43	480,95	481,00	50%	1,71	18,50	0,15	481,20
	EX-4	CP3a - Trecho 2	7+500	D	2,13	479,95	480,00	50%	1,06	11,50	0,15	480,20
	EX-5	CP3b - Trecho 1	1+400	D	1,53	486,04	486,09	50%	0,76	8,30	0,15	486,29
4	EX-6	CS23	1+750	E	0,28	477,14	477,19	100%	0,28	3,10	0,15	477,34
	EX-7	CS25 - Trecho 1	3+550	E	2,68	480,42	480,47	50%	1,34	14,40	0,15	480,67
	EX-8	CS25 - Trecho 2	4+800	D	1,14	479,42	479,47	50%	0,57	6,20	0,15	479,67
	EX-9	CS27	2+400	E	0,54	480,12	480,17	50%	0,27	2,90	0,15	480,32

1

1

NOTAS:

1 - MEDIDAS, COORDENADAS E ELEVAÇÕES EM METRO.

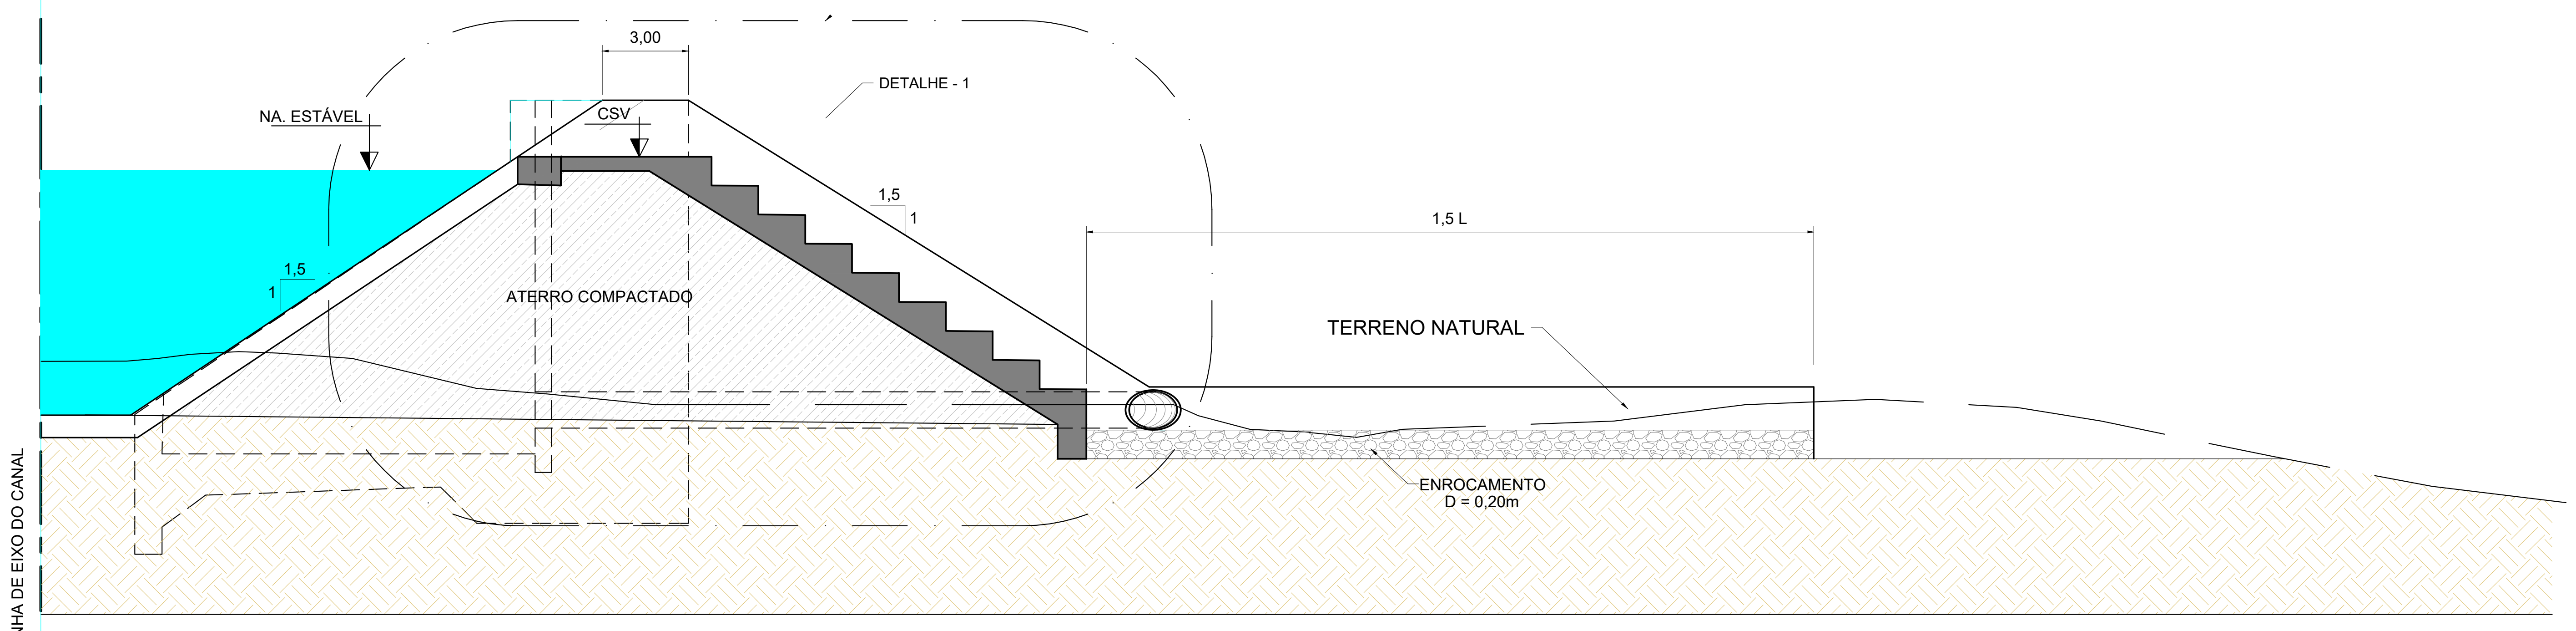
NA. ESTÁVEL
CSV
3,00
DETALHE - 1
1,5
1
1,5
1
ATERRO COMPACTADO
1,5 L
TERRENO NATURAL
ENROCAMENTO
D = 0,20m
LINHA DE EIXO DO CANAL

CORTE A - A
ESC. 1:200

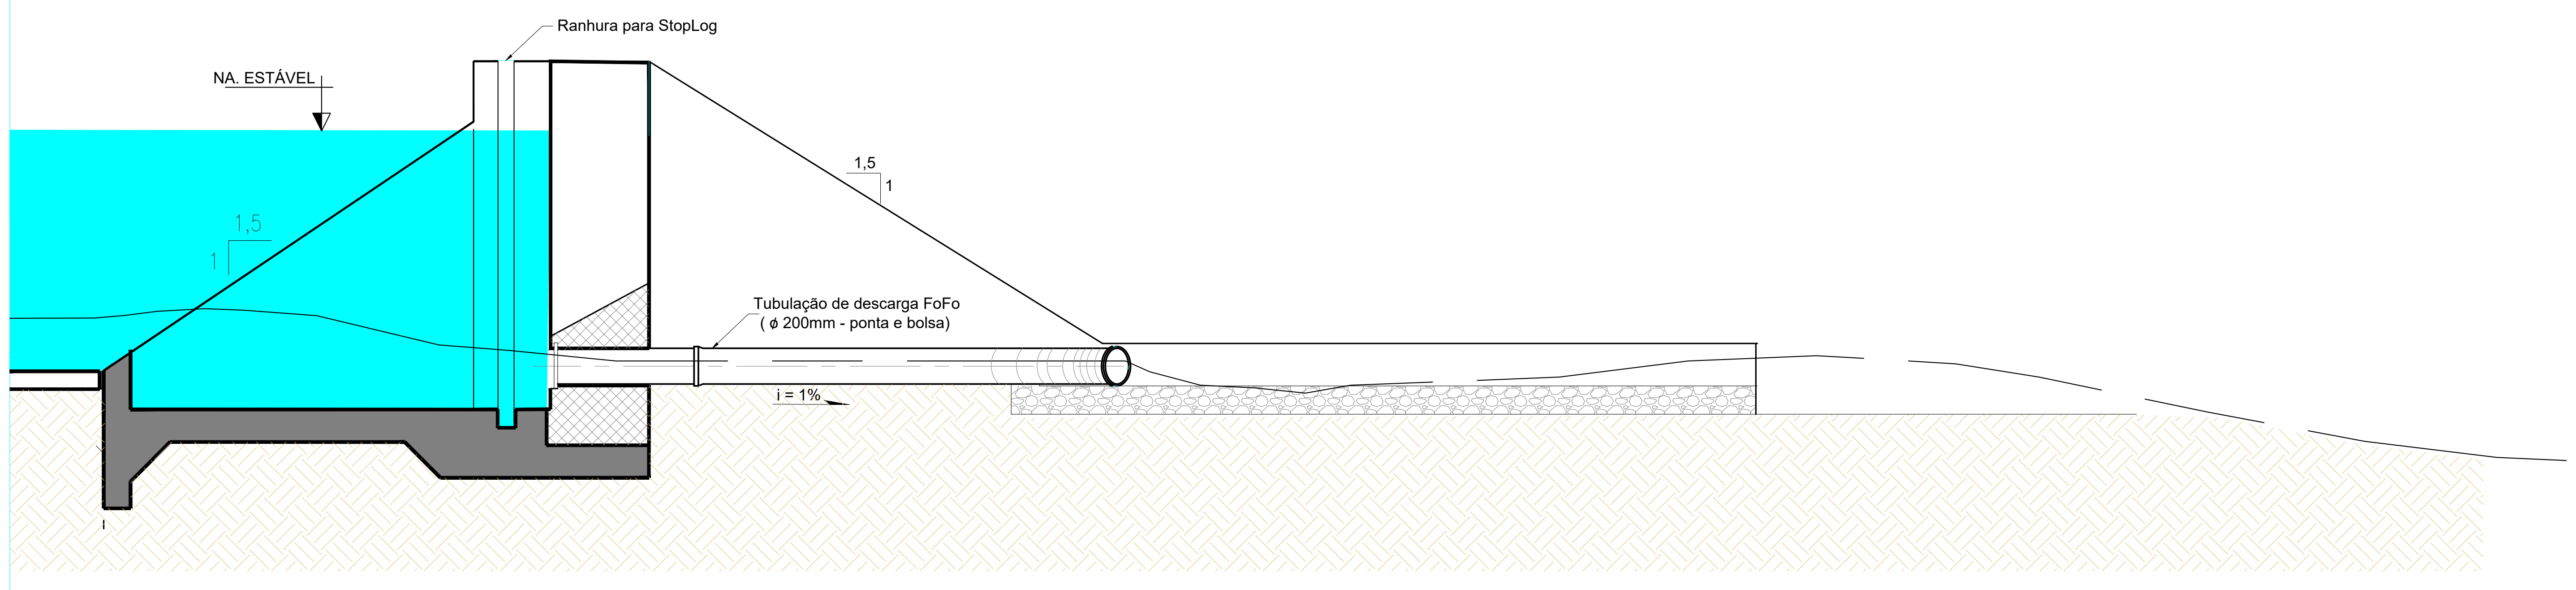
Ranhura para StopLog
NA. ESTÁVEL
1,5
1
1,5
1
Tubulação de descarga FoFo
(ø 200mm - ponta e bolsa)
i = 1%

CORTE B - B -COMPORTA DE FUNDO NOS CANAIS
ESC. 1:200

REVISÕES - 1

AS ESTRUTURAS INDICADAS FORAM REPOSICIONADAS EM DECORRÊNCIA DA ALTERAÇÃO DO PERÍMETRO IRRIGÁVEL DA ETAPA 3, CONFORME SOLICITAÇÕES FEITAS APÓS CONSULTA PÚBLICA. OS PARÂMETROS DE PROJETO PERMANECEM CONFORME ESTABELECIDO NA VERSÃO ANTERIOR DO ESTUDO.

Revisão	Data	Descrição	Elab.	Verif.	Aprov.	Aut.
1	06/07/26	REPOSICIONAMENTO DAS ESTRUTURAS	NP	AHL	EDK	
0	19/11/25	EMISSÃO INICIAL	NP	AHL	EDK	

FUNDO DE DESENVOLVIMENTO DA INFRAESTRUTURA
REGIONAL SUSTENTÁVEL - FDIRS

ESTRUTURAÇÃO DE PROJETO DE CONCESSÃO DO
PERÍMETRO IRRIGADO DO JAÍBA (ETAPAS 3 E 4)

ANTEPROJETO

EXTRAVASOR LATERAL E COMPORTA DE FUNDO
PROJETO TÍPICO
PLANTA BAIXA, CORTES E TABELA

Finalidade de Emissão	1 Para Informação	☐ 2 Para Comentários	▨ 3 Para Aprovação	☐ 4 Para Execução	☐ 5 Como Construído	☐ 6 Para Utilização	☐ 7 Para Providências

Moysés & Pires
Sociedade de advogados
ENGECORPS
GrupoTYPSA
A&M
Plena
Consultoria e Projetos

Data:
Escala: INDICADA
Elaboração:
Aprovação
Verificação:
Autorização
Referência:
Revisão: 1
Desenho nº JA-DS-HI-0002