

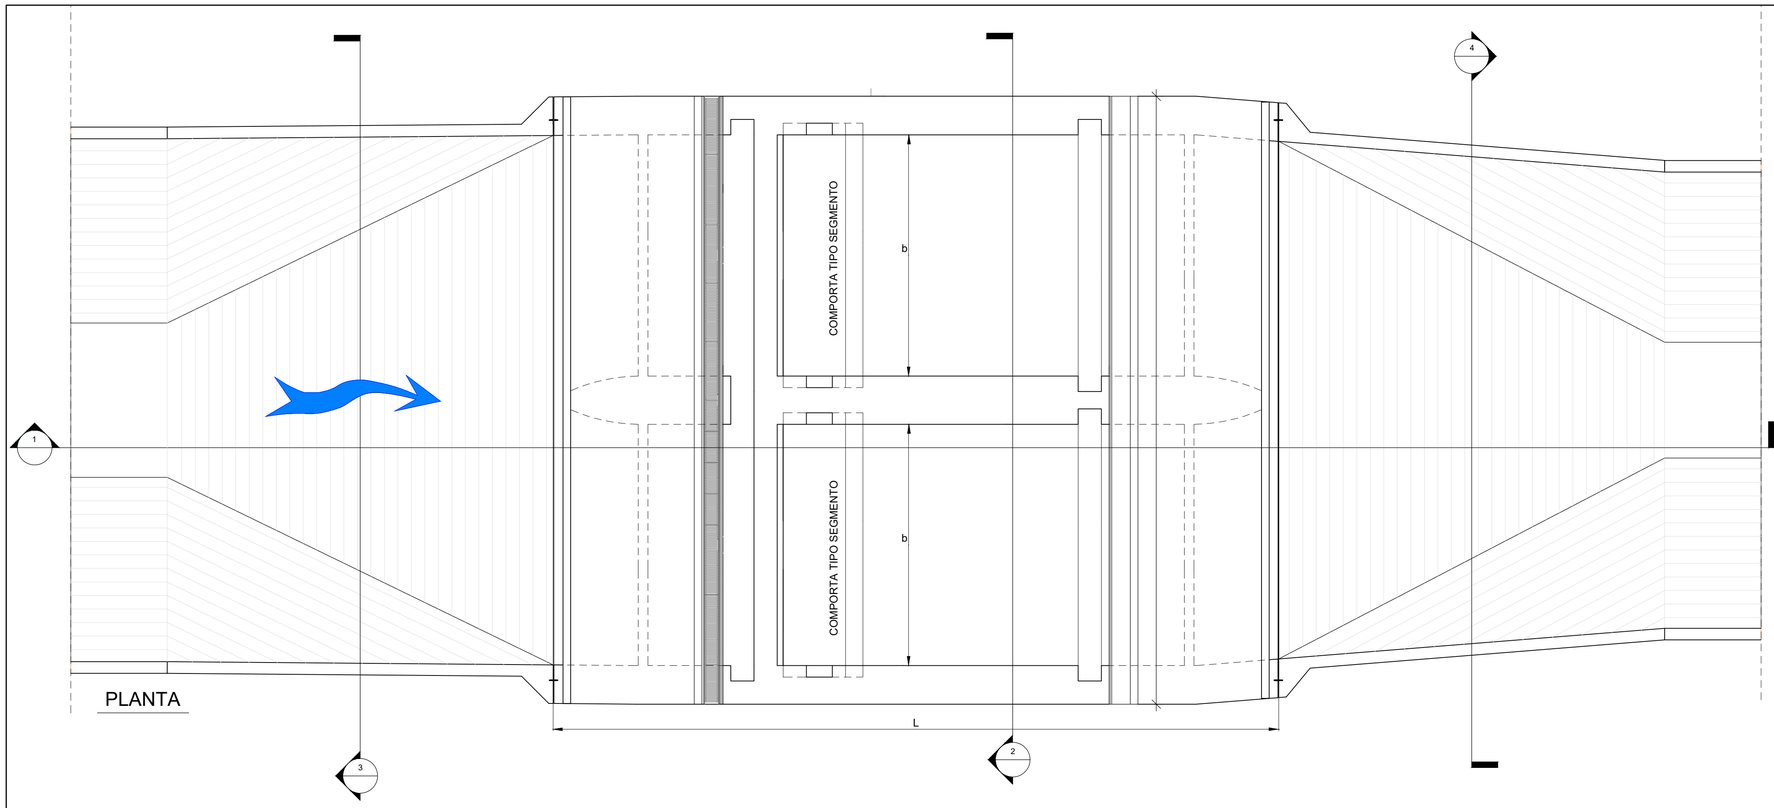



Etapa	Canal	Obra	Estaca (em km)		Extensão (L)	Cota de fundo(C.F.)	Vazão	Base (b)	Profundidade (h)	N.A. estático	Borda livre (B.L.)	Cota da berma (C.B.)
			Início	Fim	(m)	(m)	(m³/s)	(m)	(m)	(m)	(m)	(m)
3	CS19	EC2	5+800,00	5+808,00	8,00	472,83	2,366	3,20	1,06	473,89	0,25	474,14
		EC3	10+100,00	10+108,00	8,00	471,97	1,922	2,60	1,11	473,08	0,25	473,33
		EC4	14+300,00	14+308,00	8,00	471,13	1,922	2,60	1,11	472,24	0,25	472,49
		EC5	20+500,00	20+508,00	8,00	469,89	0,436	1,30	0,67	470,56	0,20	470,76
	CT1-CS19	EC6	5+600,00	5+608,00	8,00	473,42	0,366	1,30	0,59	474,01	0,20	474,21
	CS21a	EC2	4+000,00	4+008,00	8,00	477,80	3,986	4,00	1,39	479,19	0,25	479,44
		EC3	8+000,00	8+008,00	8,00	477,20	3,204	3,30	1,42	478,62	0,25	478,87
		EC4	12+000,00	12+008,00	8,00	461,92	2,796	3,10	1,37	463,29	0,25	463,54
		EC5	16+000,00	16+008,00	8,00	461,32	1,478	2,30	1,03	462,35	0,25	462,60
					57066,00							
4	CP3	EC2	6+850,00	6+858,00	8,00	476,12	6,806	4,00	2,41	478,52	0,30	478,82
	CP3a	EC3	5+000,00	5+008,00	8,00	478,73	2,300	2,70	1,22	479,95	0,25	480,20
	CS25	EC4	4+000,00	4+008,00	8,00	478,51	1,097	2,10	0,90	479,41	0,25	479,66

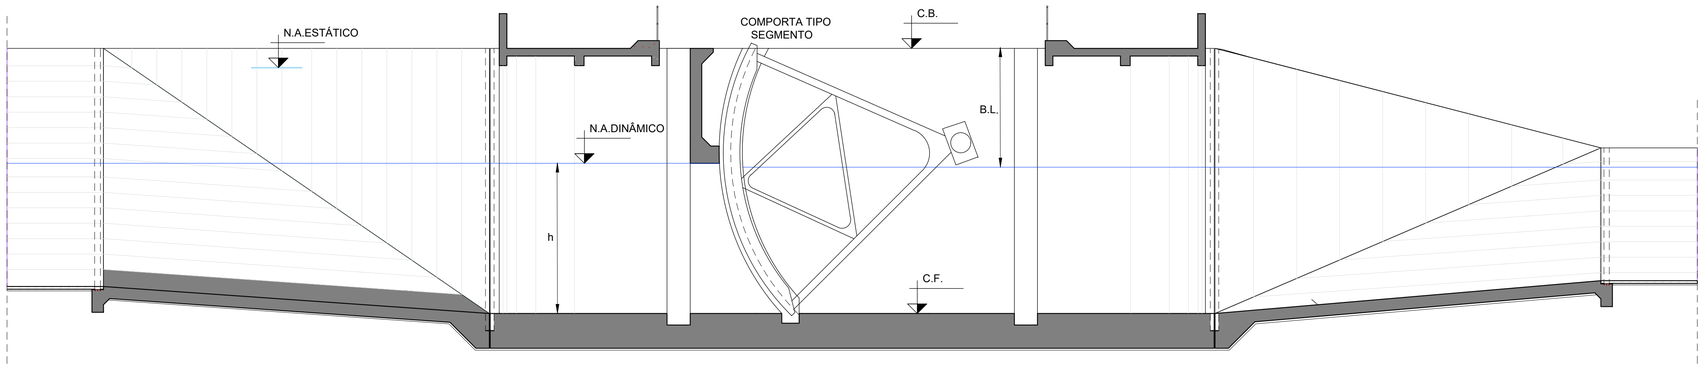


1 CORTE 1 - SEÇÃO LONGITUDINAL

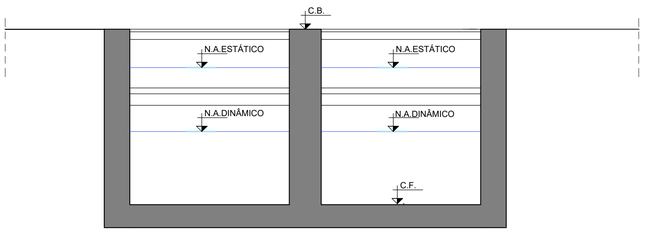

2 CORTE 2 - SEÇÃO TRANSVERSAL

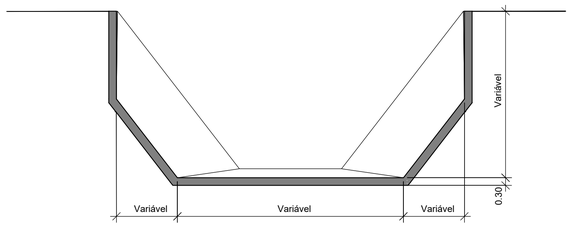

3 SEÇÃO TRANSVERSAL DA TRANSIÇÃO À MONTANTE

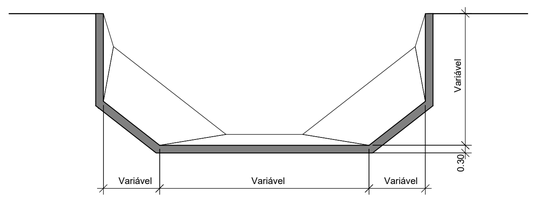

4 SEÇÃO TRANSVERSAL DA TRANSIÇÃO À JUSANTE

NOTAS:
1 - MEDIDAS, COORDENADAS E ELEVAÇÕES EM METRO.

REVISÕES - 2

AS ESTRUTURAS INDICADAS FORAM REPOSICIONADAS EM DECORRÊNCIA DA ALTERAÇÃO DO PERÍMETRO IRRIGÁVEL DA ETAPA 3, CONFORME SOLICITAÇÕES FEITAS APÓS CONSULTA PÚBLICA. OS PARÂMETROS DE PROJETO PERMANECEM CONFORME ESTABELECIDO NA VERSÃO ANTERIOR DO ESTUDO.

Revisão	Data	Descrição	Elab.	Verif.	Aprov.	Aut.
2	06/07/26	REPOSICIONAMENTO DAS ESTRUTURAS	NP	AHL	EDK	
1	04/12/25	ATUALIZAÇÃO DAS VAZÕES DE PROJETO	NP	AHL	EDK	
0	19/11/25	EMISSÃO INICIAL	NP	AHL	EDK	

FUNDO DE DESENVOLVIMENTO DA INFRAESTRUTURA REGIONAL SUSTENTÁVEL - FDIRS

ESTRUTURAÇÃO DE PROJETO DE CONCESSÃO DO PERÍMETRO IRRIGADO DO JAÍBA (ETAPAS 3 E 4)

ANTEPROJETO

ESTRUTURA DE CONTROLE

PROJETO TÍPICO
PLANTA BAIXA, CORTES E TABELA

Finalidade de Emissão: 1 Para Informação | 2 Para Comentários | Para Aprovação | 4 Para Execução | 5 Como Construído | 6 Para Utilização | 7 Para Providências

Moyses & Pires | ENGECORPS | Plena Consultoria e Projetos

Data:
Elaboração:
Verificação:
Escala: sem escala
Aprovação:
Autorização:
Referência:
Revisão: 2
Desenho nº JA-DS-HI-0003