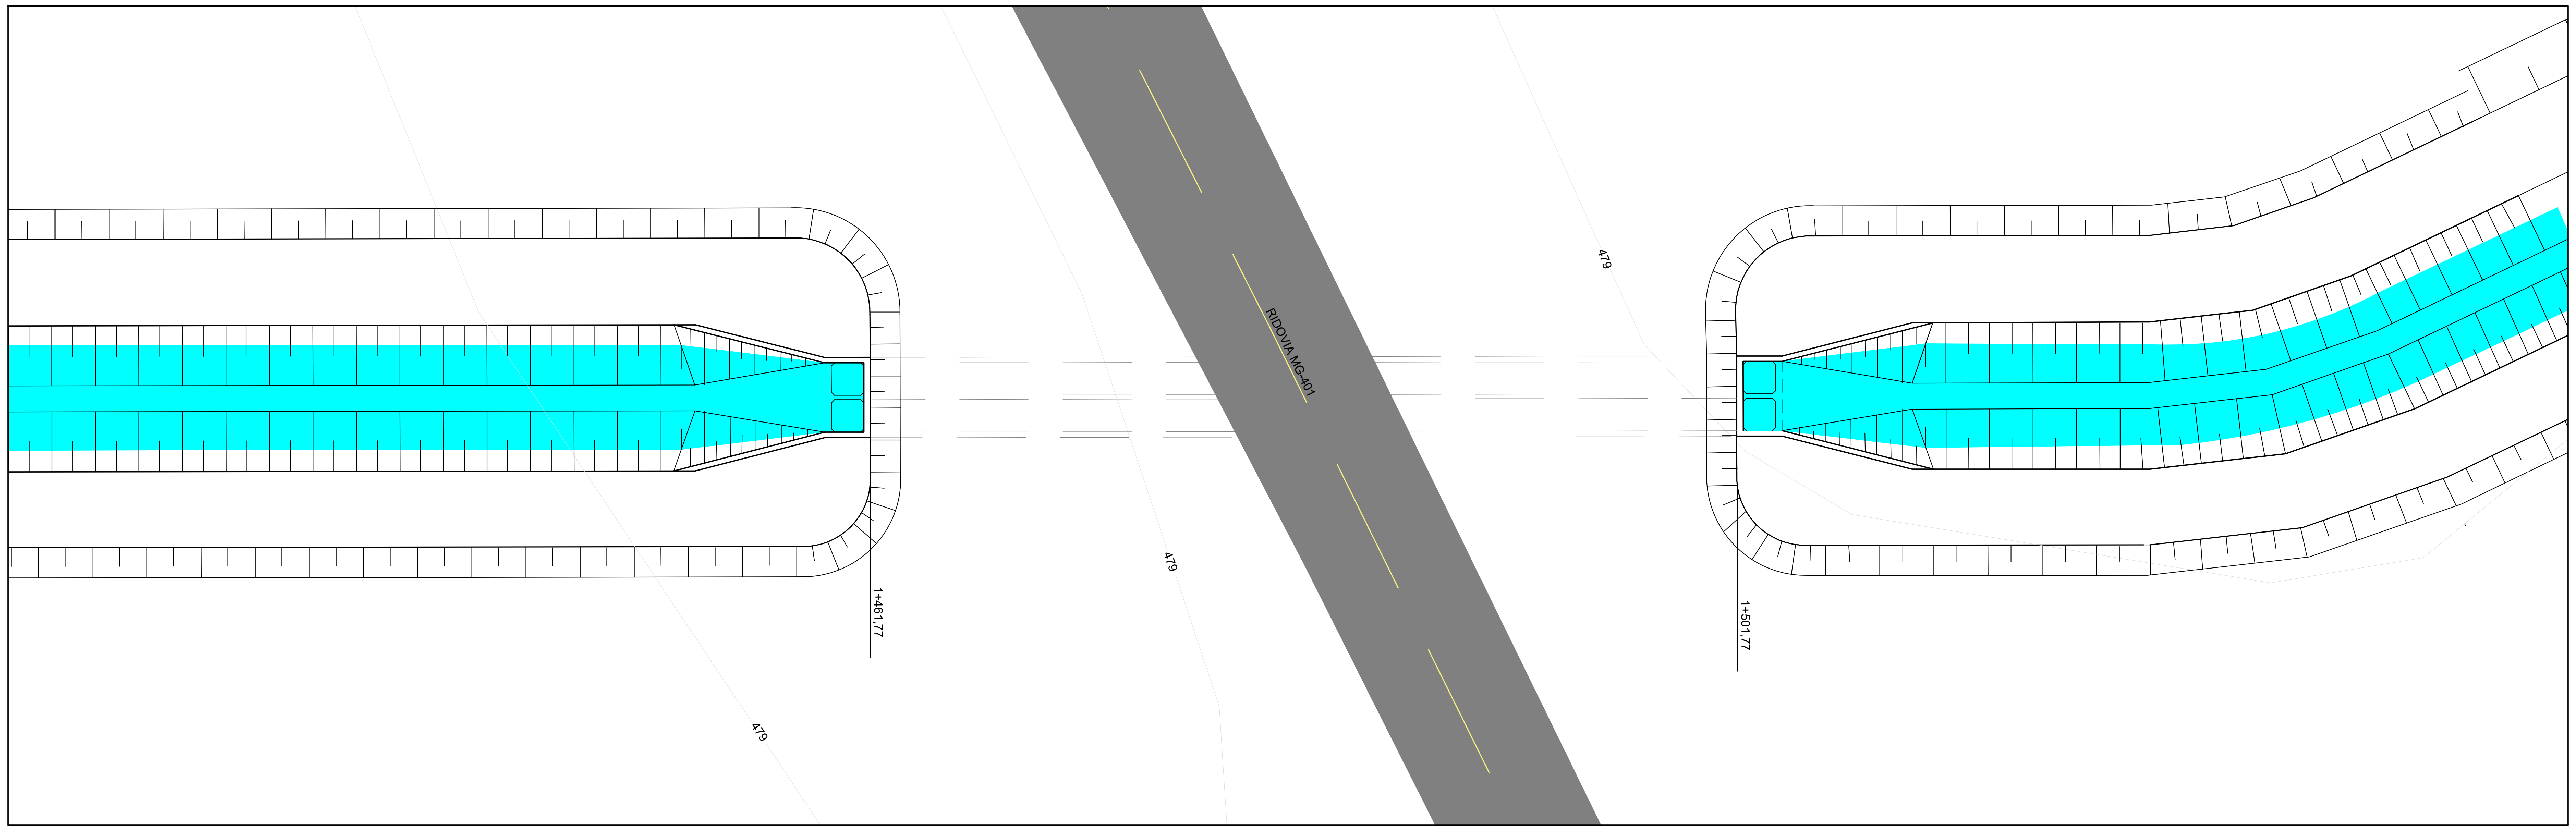
RODOVIA MG-401
479
479
479
1+461,77
1+501,77

PLANTA
ESC.: 1:200

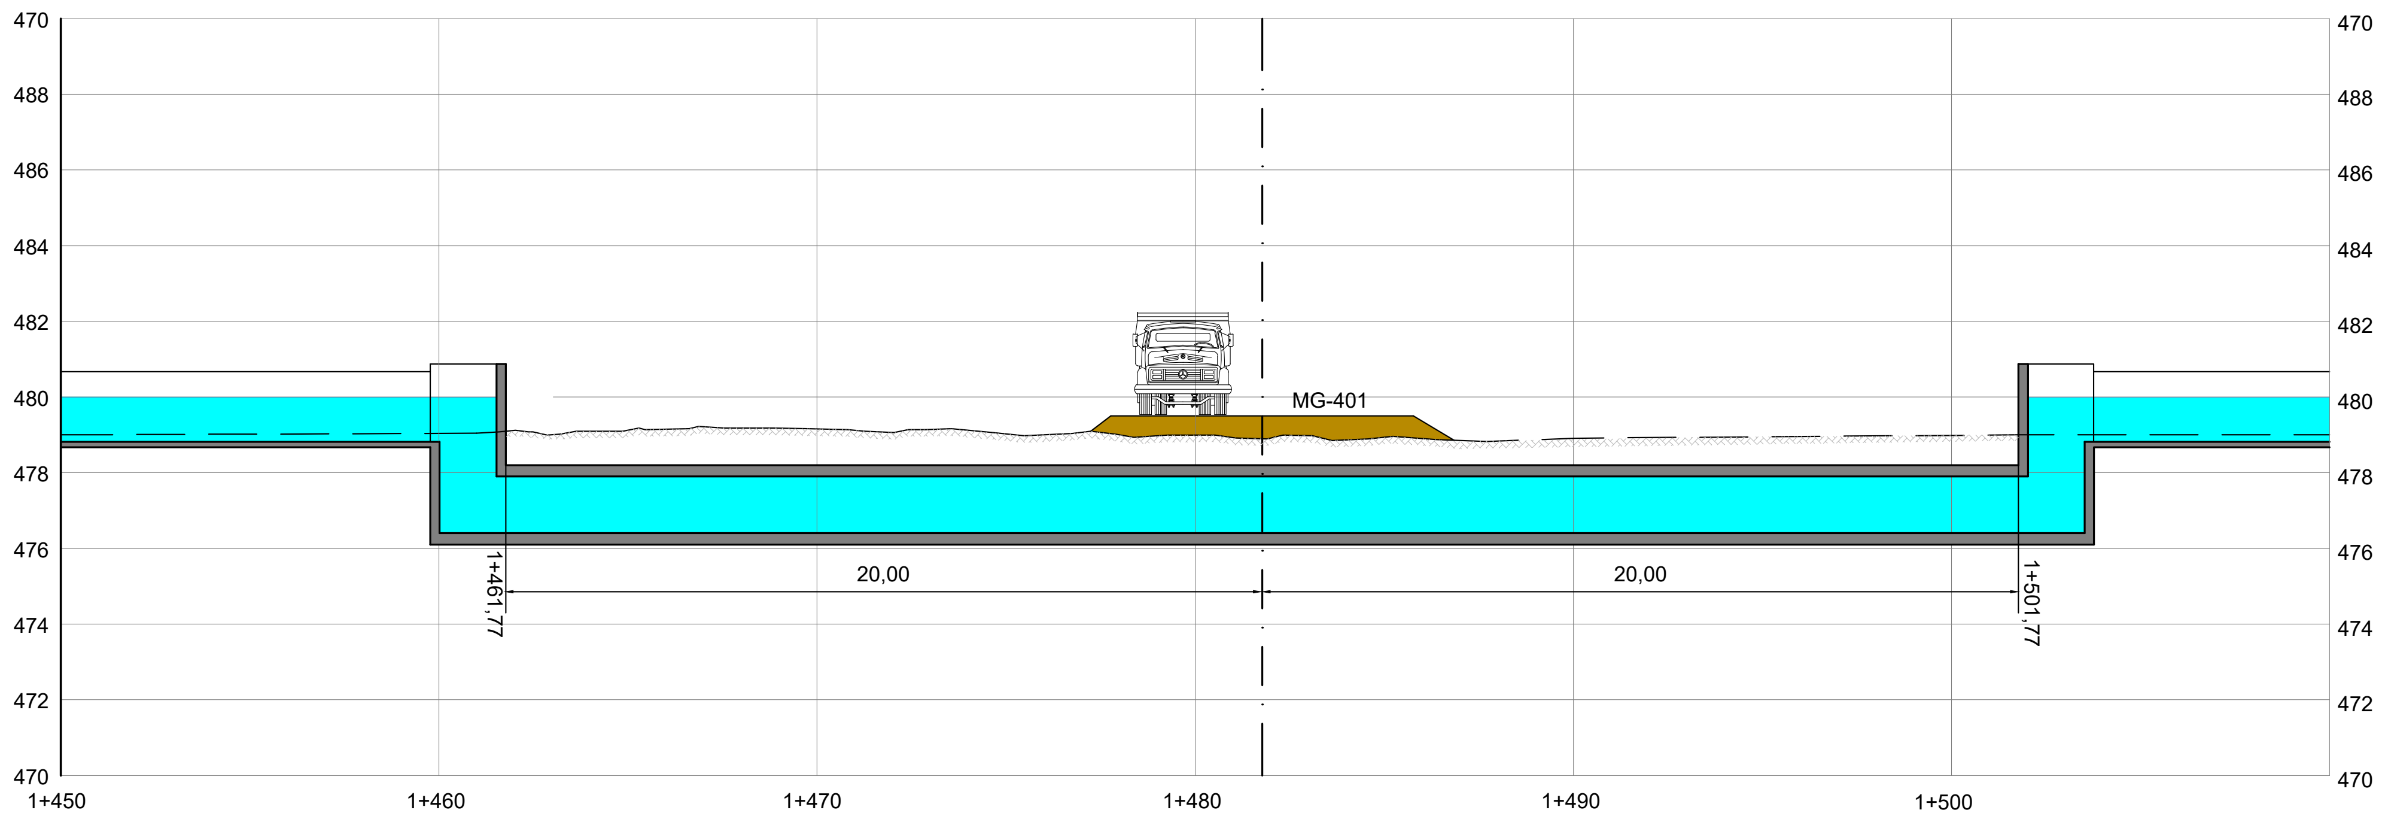
470
488
486
484
482
480
478
476
474
472
470
MG-401
20,00
20,00
1+461,77
1+501,77
1+450
1+460
1+470
1+480
1+490
1+500

PERFIL LONGITUDINAL
ESC. 1:200

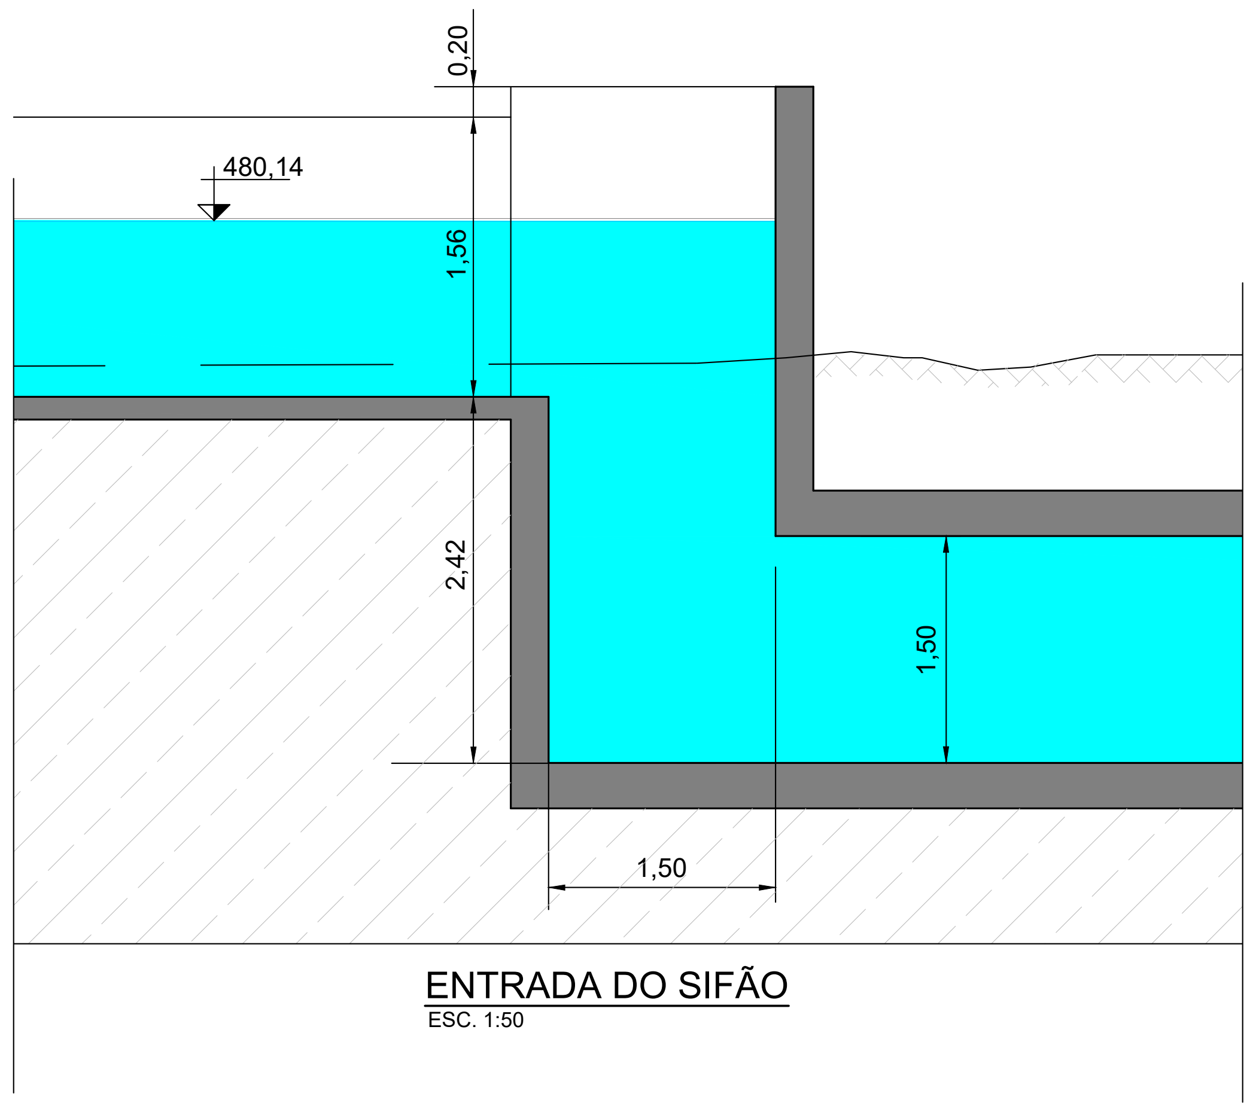
0,20
480,14
1,56
2,42
1,50
1,50

ENTRADA DO SIFÃO
ESC. 1:50

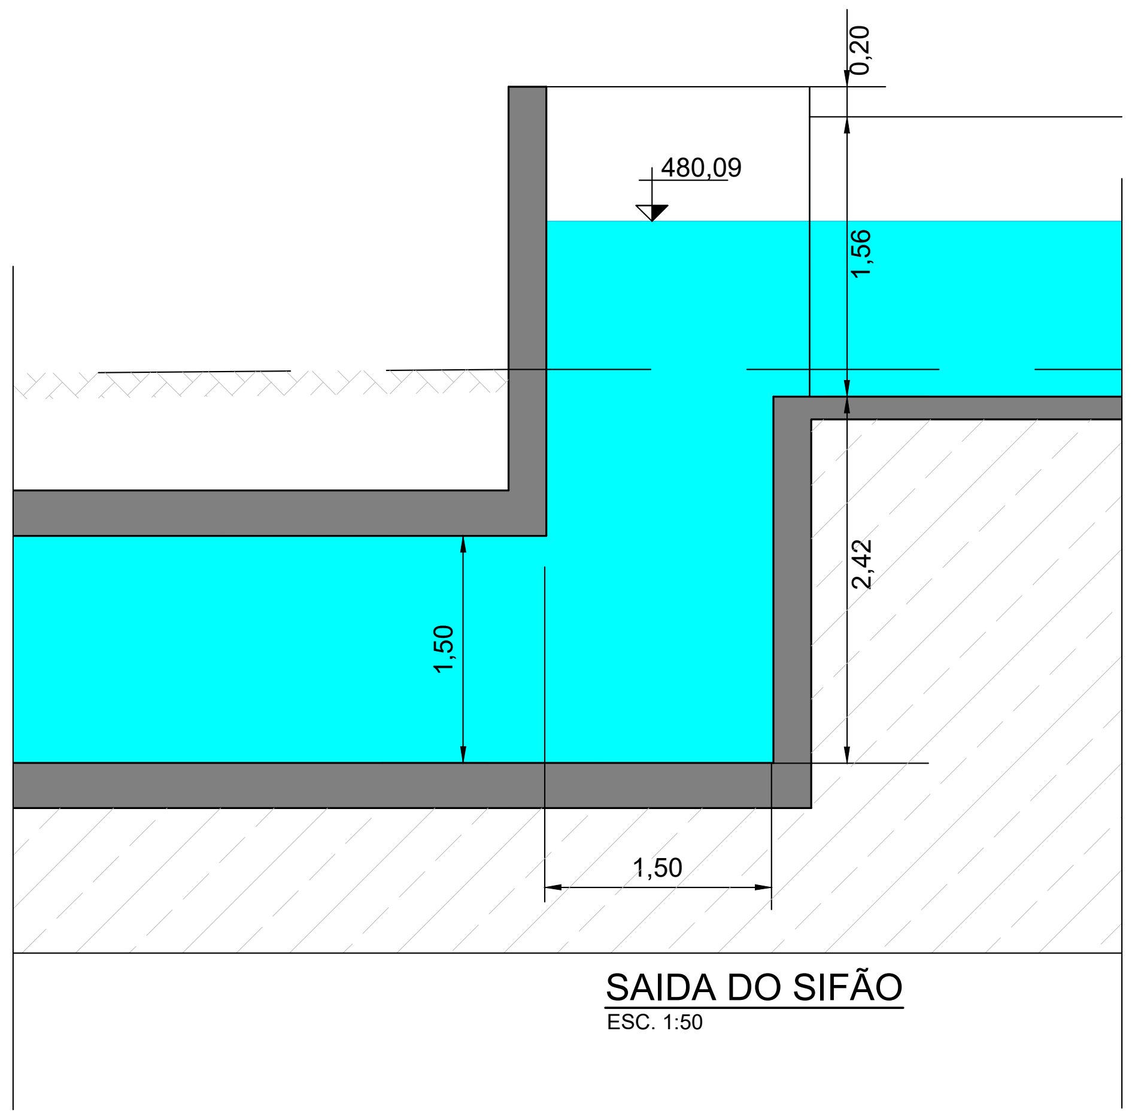
0,20
480,09
1,56
2,42
1,50
1,50

SAIDA DO SIFÃO
ESC. 1:50

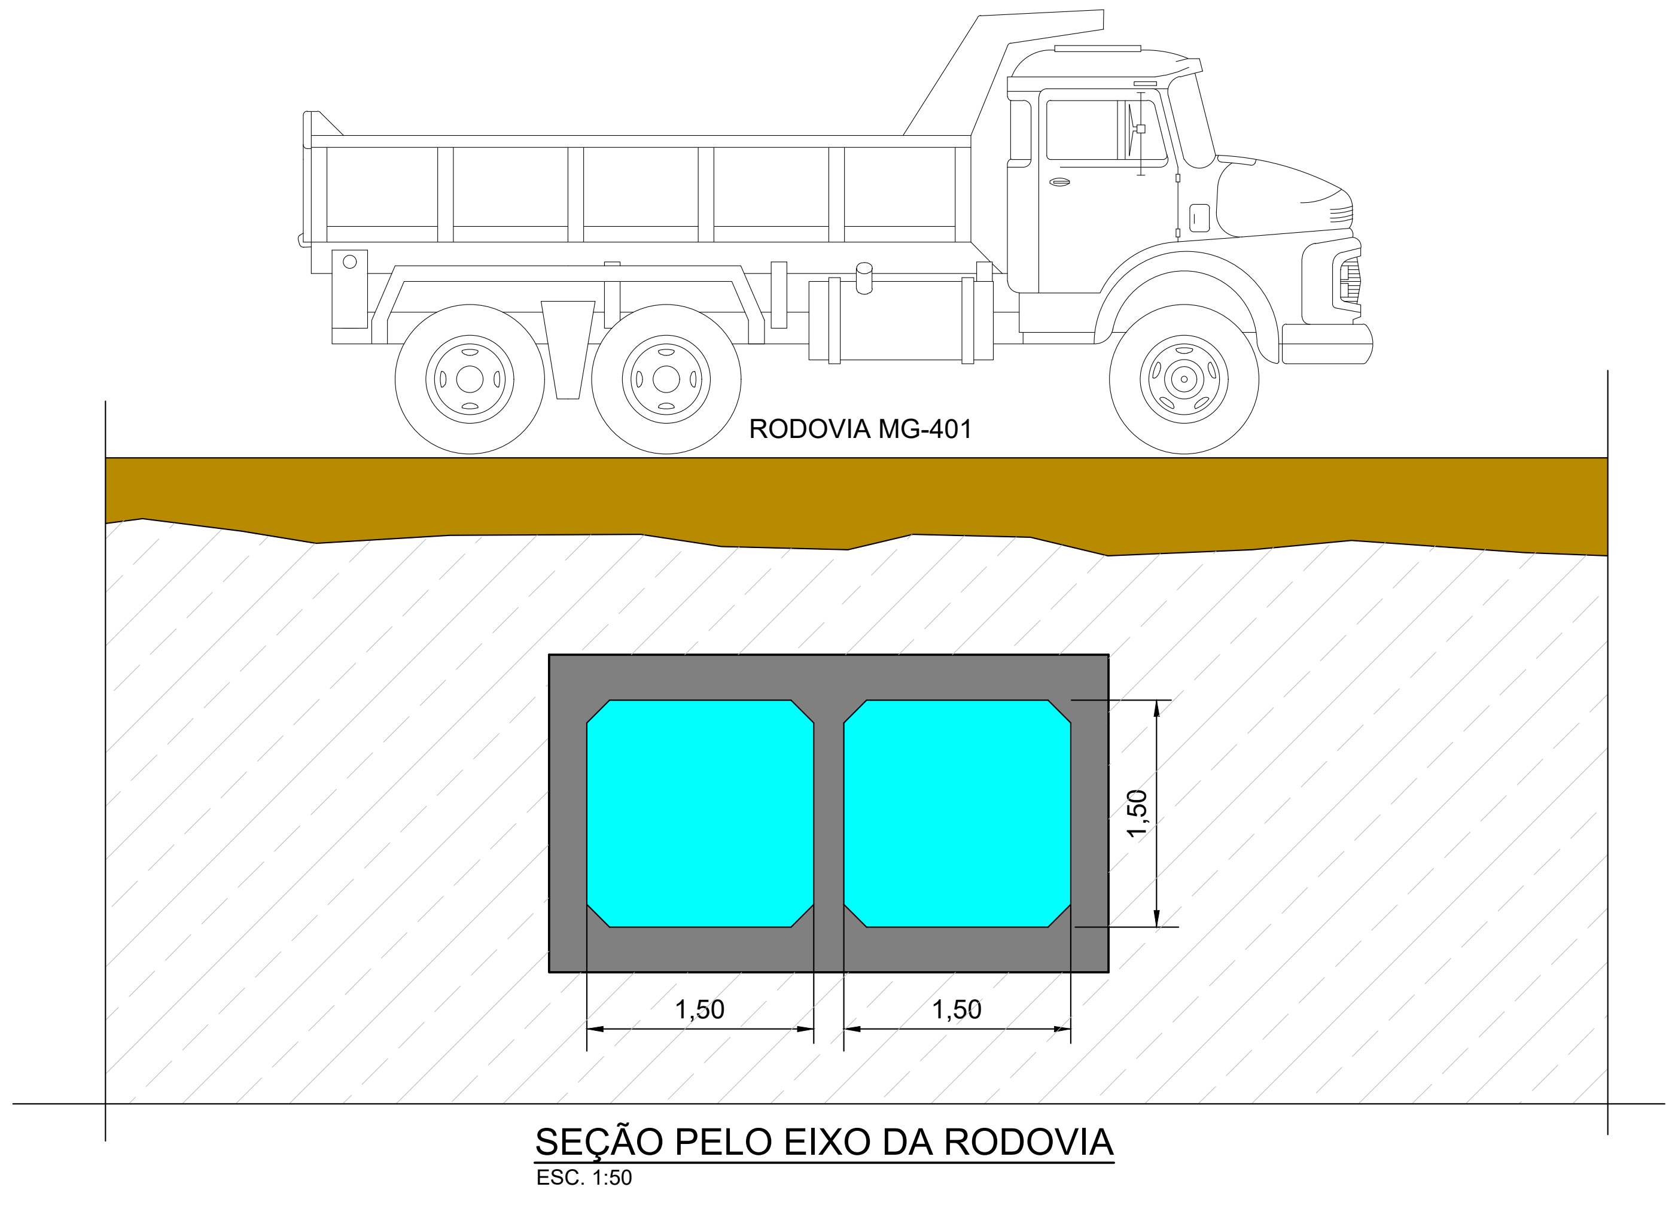
RODOVIA MG-401
1,50
1,50
1,50

SEÇÃO PELO EIXO DA RODOVIA
ESC. 1:50

NOTAS:

1 - MEDIDAS, COORDENADAS E ELEVAÇÕES EM METRO.

Revisão	Data	Descrição	Elab.	Verif.	Aprov.	Aut.
0	19/11/25	EMISSÃO INICIAL	NP	AHL	EDK	

FUNDO DE DESENVOLVIMENTO DA INFRAESTRUTURA
REGIONAL SUSTENTÁVEL - FDIRS

ESTRUTURAÇÃO DE PROJETO DE CONCESSÃO DO
PERÍMETRO IRRIGADO DO JAÍBA (ETAPAS 3 E 4)

ANTEPROJETO

SIFÃO INVERTIDO
PLANTA BAIXA
CORTES E DETALHE

Finalidade de Emissão	1 Para Informação	2 Para Comentários	▨ 3 Para Aprovação	4 Para Execução	5 Como Construído	6 Para Utilização	7 Para Providências

Data:
Escala: INDICADA
Elaboração:
Verificação:
Aprovação
Autorização
Referência:
Revisão: 0
Desenho nº JA-DS-HI-0004