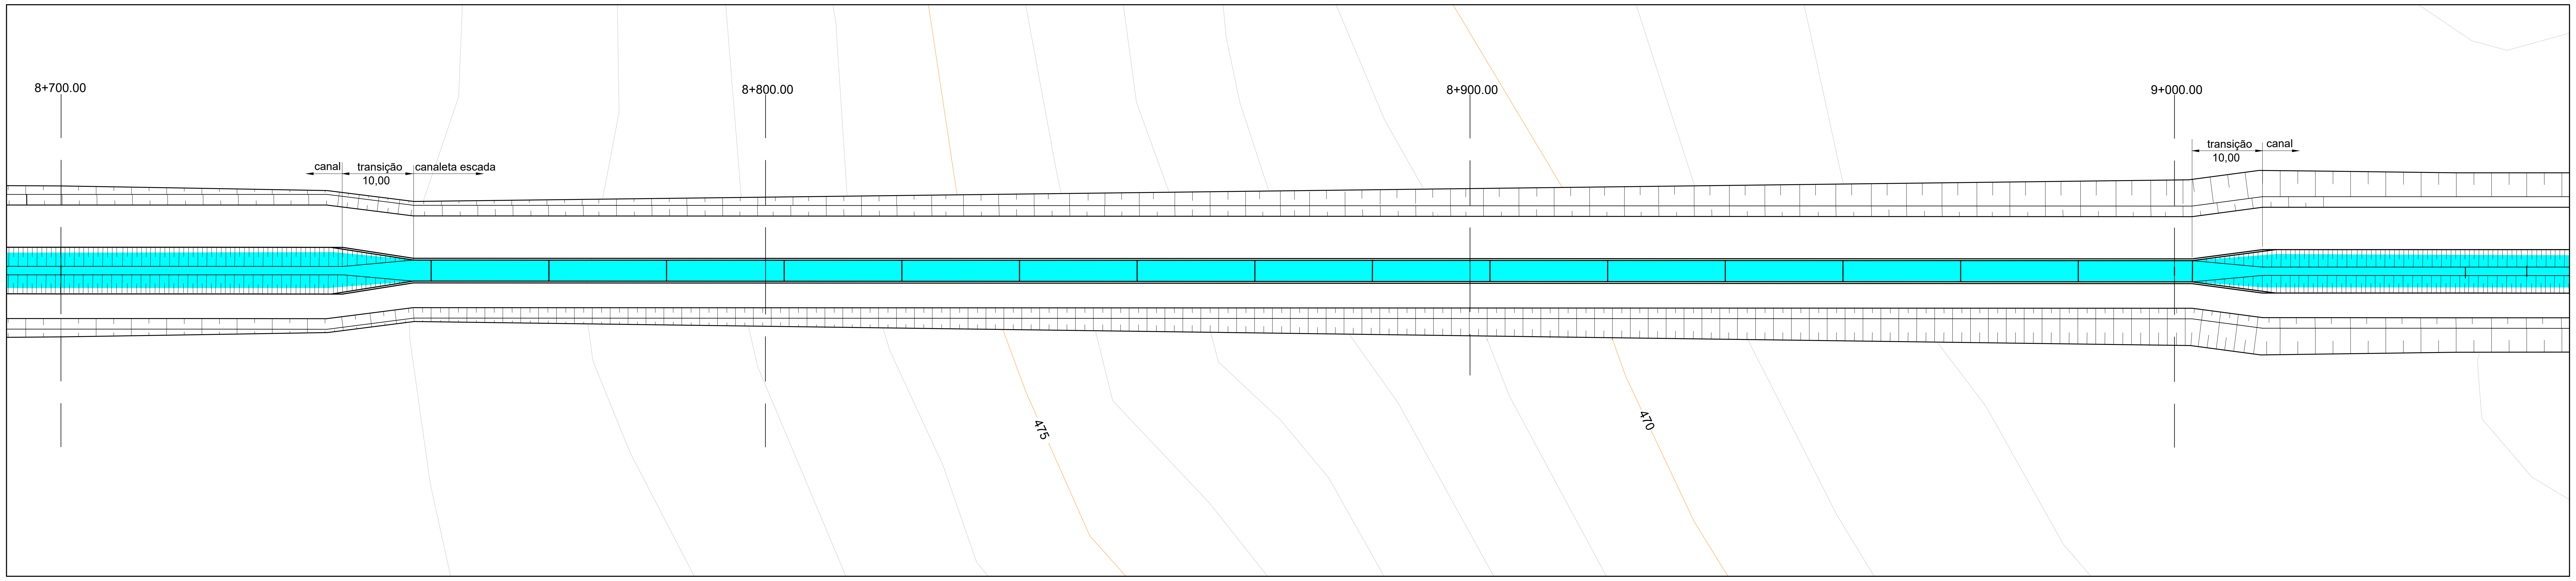

PLANTA
ESC.: 1:500

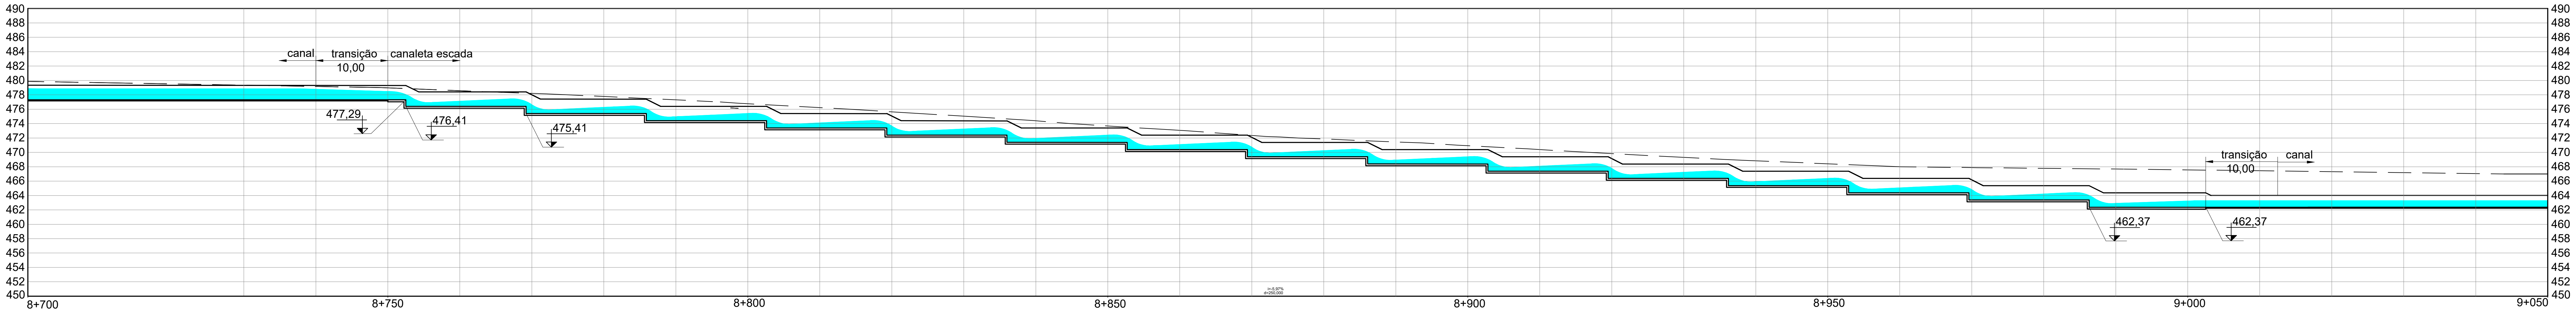

PERFIL LONGITUDINAL
ESC. 1:500

1

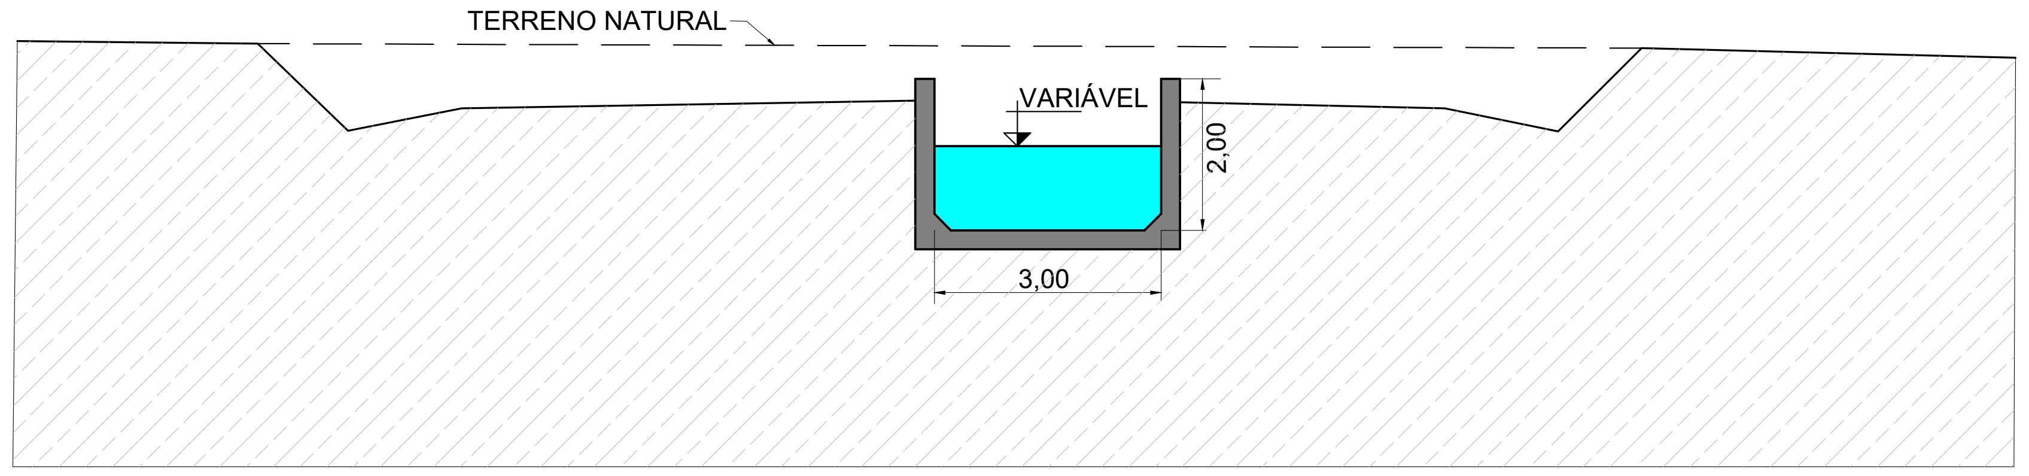

DETALHE DA ESCADA DISSIPADORA
ESC. 1:100

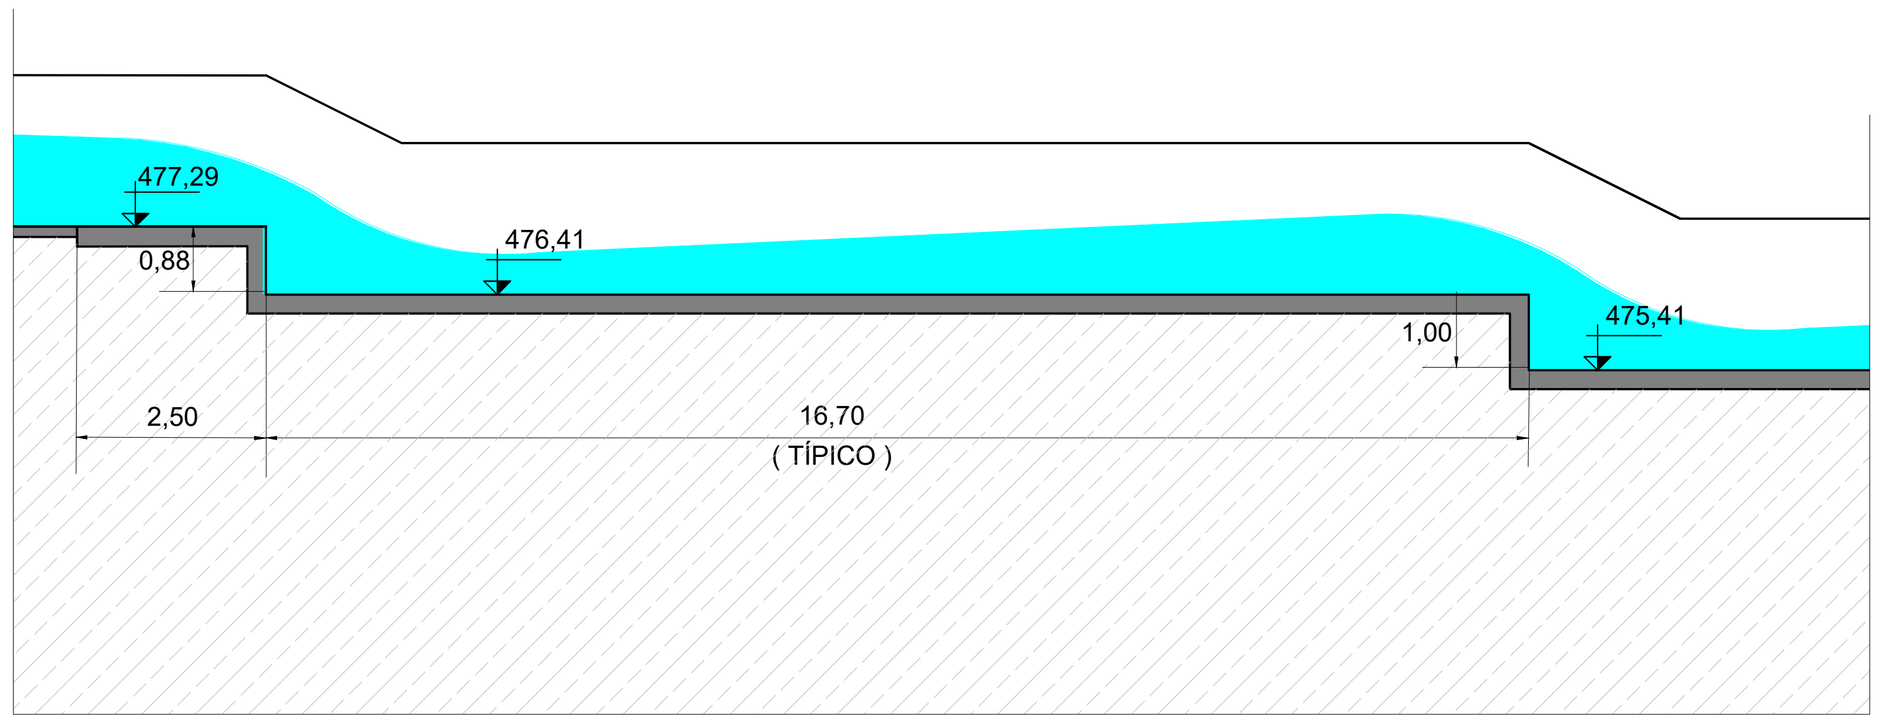

INÍCIO DA ESCADA DISSIPADORA
ESC. 1:100

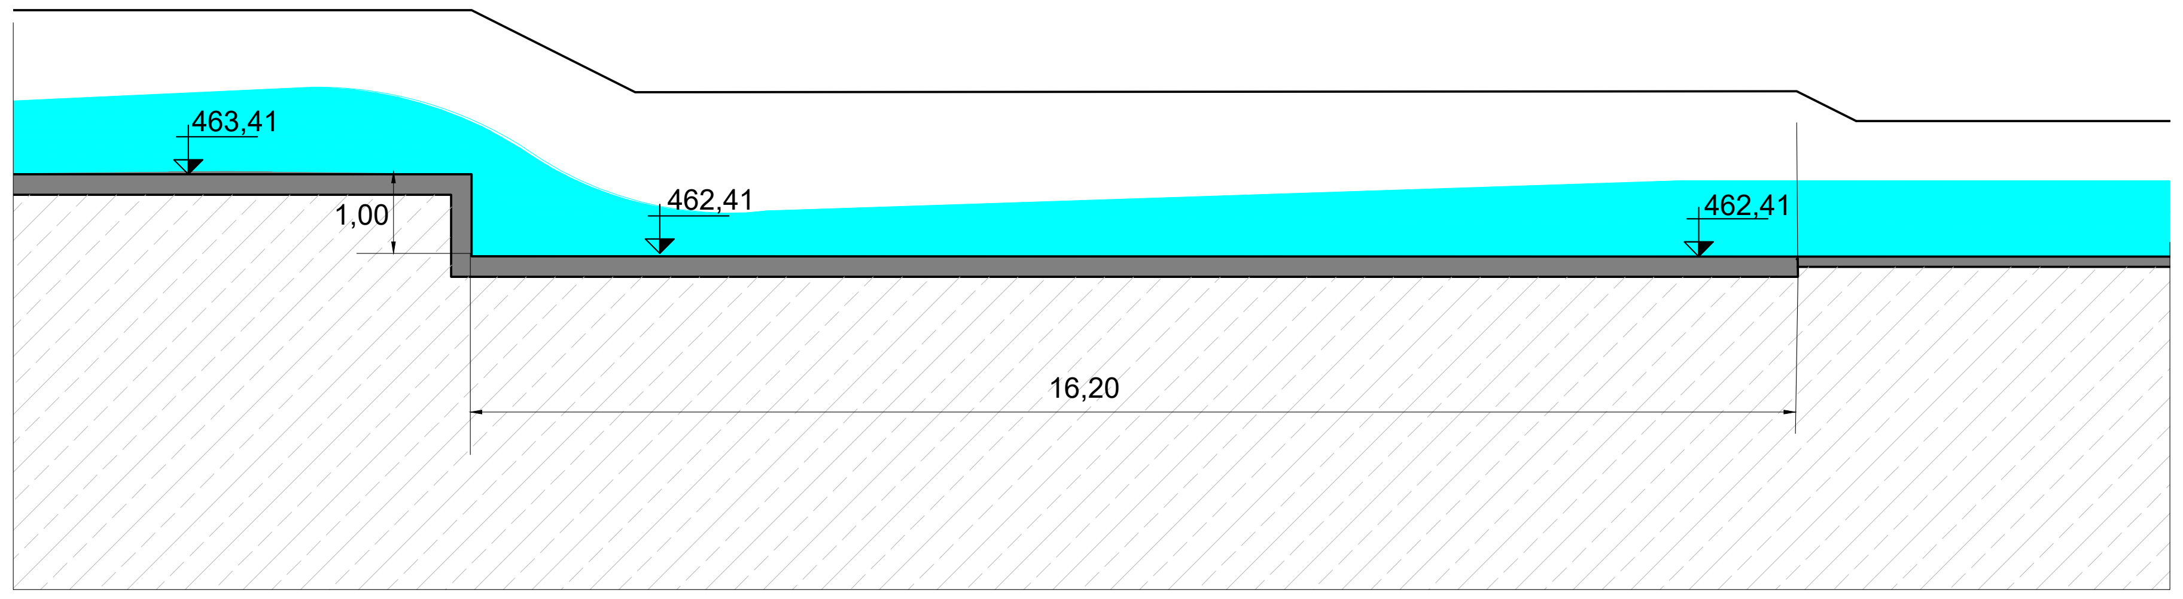

FINAL DA ESCADA DISSIPADORA
ESC. 1:100

NOTAS:

1 - MEDIDAS, COORDENADAS E ELEVAÇÕES EM METRO.

REVISÕES - 1

AS ESTRUTURAS INDICADAS FORAM REPOSICIONADAS EM DECORRÊNCIA DA ALTERAÇÃO DO PERÍMETRO IRRIGÁVEL DA ETAPA 3, CONFORME SOLICITAÇÕES FEITAS APÓS CONSULTA PÚBLICA. OS PARÂMETROS DE PROJETO PERMANECEM CONFORME ESTABELECIDO NA VERSÃO ANTERIOR DO ESTUDO.

1	06/07/26	REPOSICIONAMENTO DAS ESTRUTURAS	NP	AHL	EDK	
0	19/11/25	EMISSÃO INICIAL	NP	AHL	EDK	
Revisão	Data	Descrição	Elab.	Verif.	Aprov.	Aut.

FUNDO DE DESENVOLVIMENTO DA INFRAESTRUTURA
REGIONAL SUSTENTÁVEL - FDIRS

ESTRUTURAÇÃO DE PROJETO DE CONCESSÃO DO
PERÍMETRO IRRIGADO DO JAÍBA (ETAPAS 3 E 4)

ANTEPROJETO

ESCADA DISSIPADORA DE ENERGIA
PLANTA BAIXA
CORTES E DETALHES

Finalidade de Emissão	1 Para Informação	2 Para Comentários	▨ 3 Para Aprovação	4 Para Execução	5 Como Construído	6 Para Utilização	7 Para Providências

Moysés & Pires ENGECORPS A&M Plena	Data:	Elaboração:		Verificação:	
	Escala: INDICADA	Aprovação	. .	Autorização	. .
Referência:		Revisão: 1	Desenho nº	JA-DS-HI-0005	