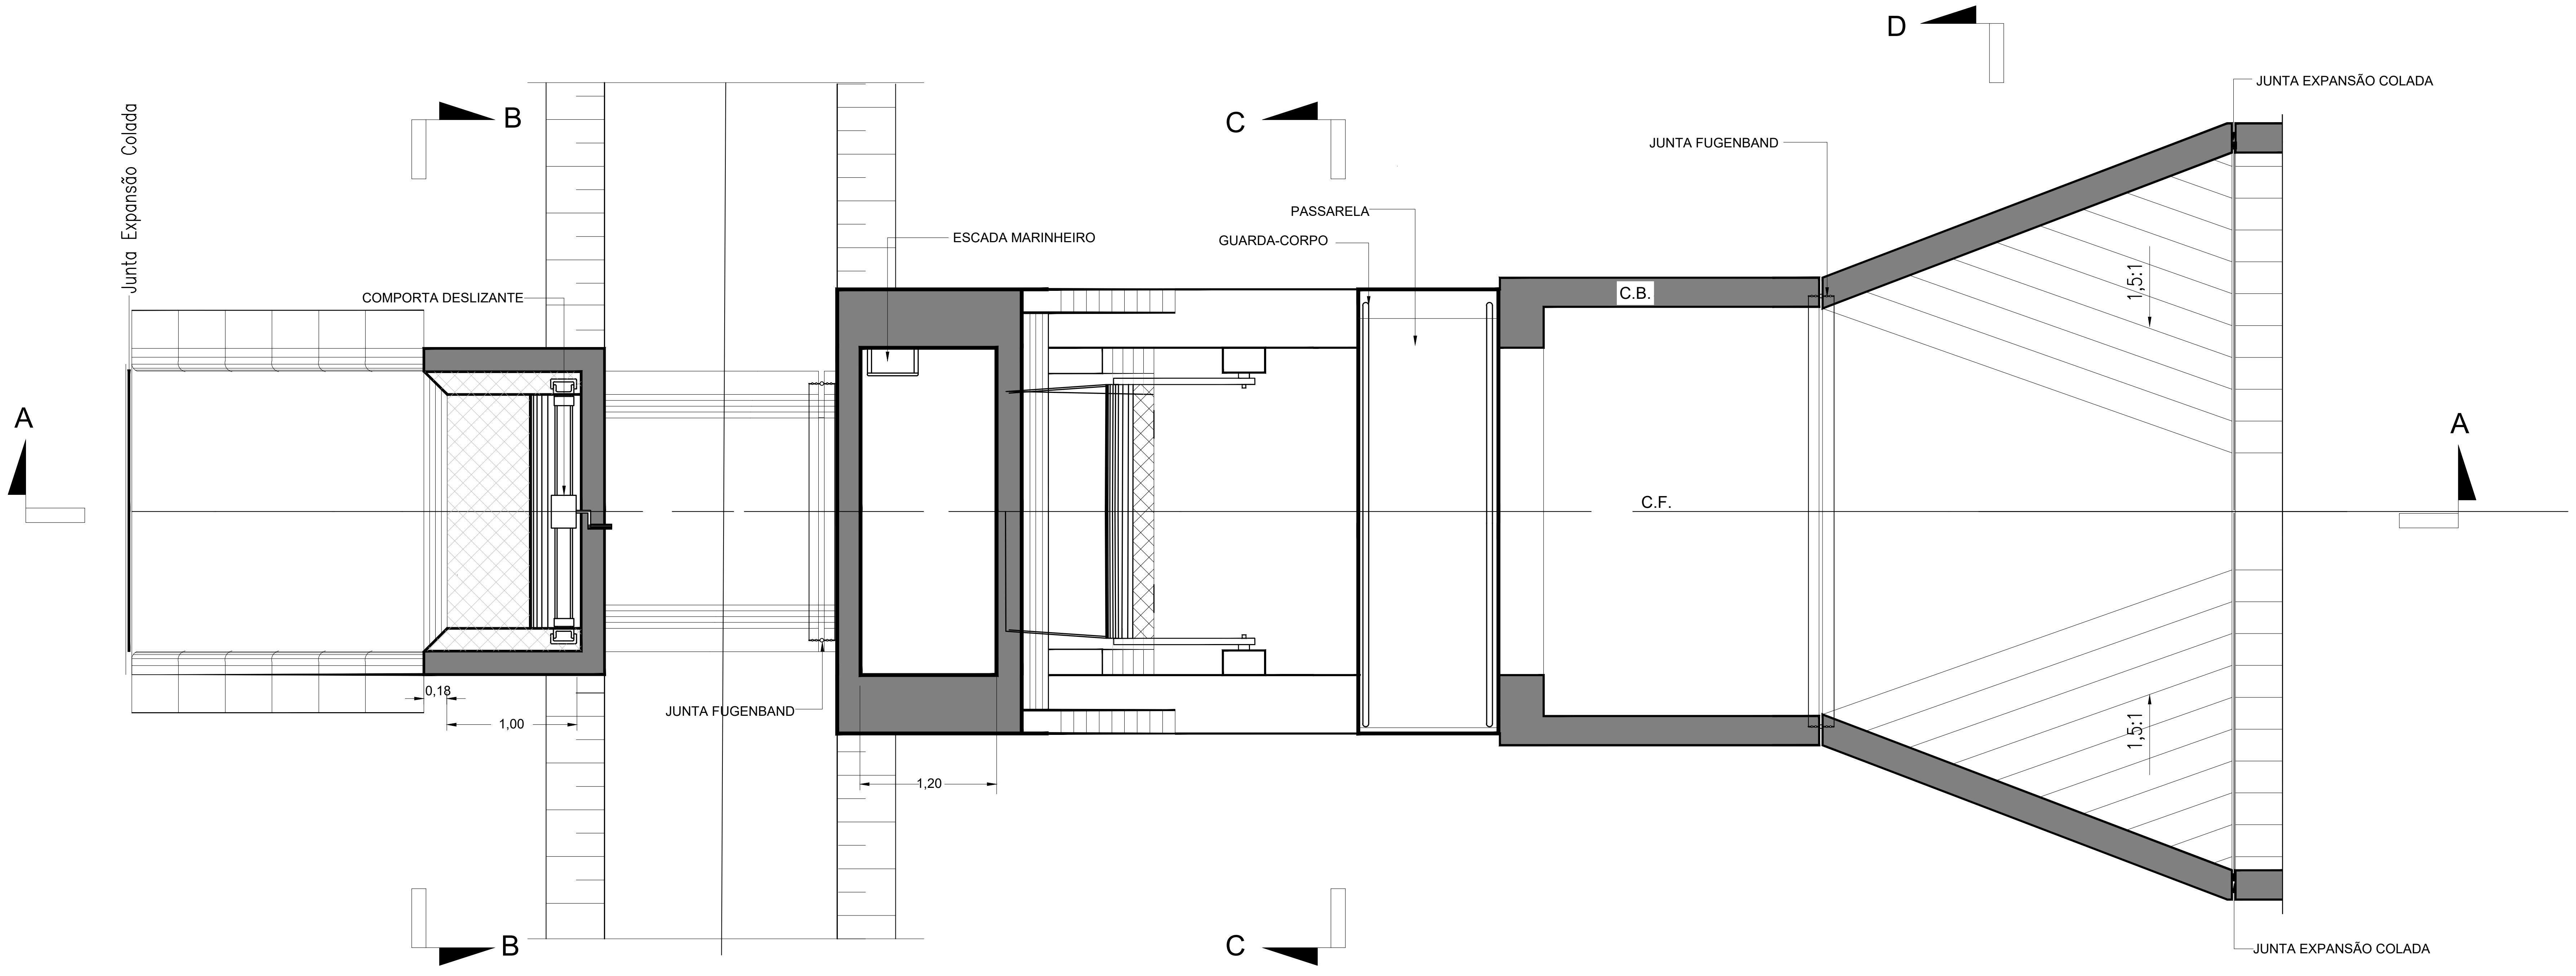
Junta Expansão Colada
B
B
C
C
D
D
A
A
COMPORTA DESLIZANTE
ESCADA MARINHEIRO
PASSARELA
GUARDA-CORPO
JUNTA FUGENBAND
JUNTA EXPANSÃO COLADA
C.B.
C.F.
1,5:1
1,5:1
0,18
1,00
1,20
JUNTA FUGENBAND
JUNTA EXPANSÃO COLADA

PLANTA BAIXA

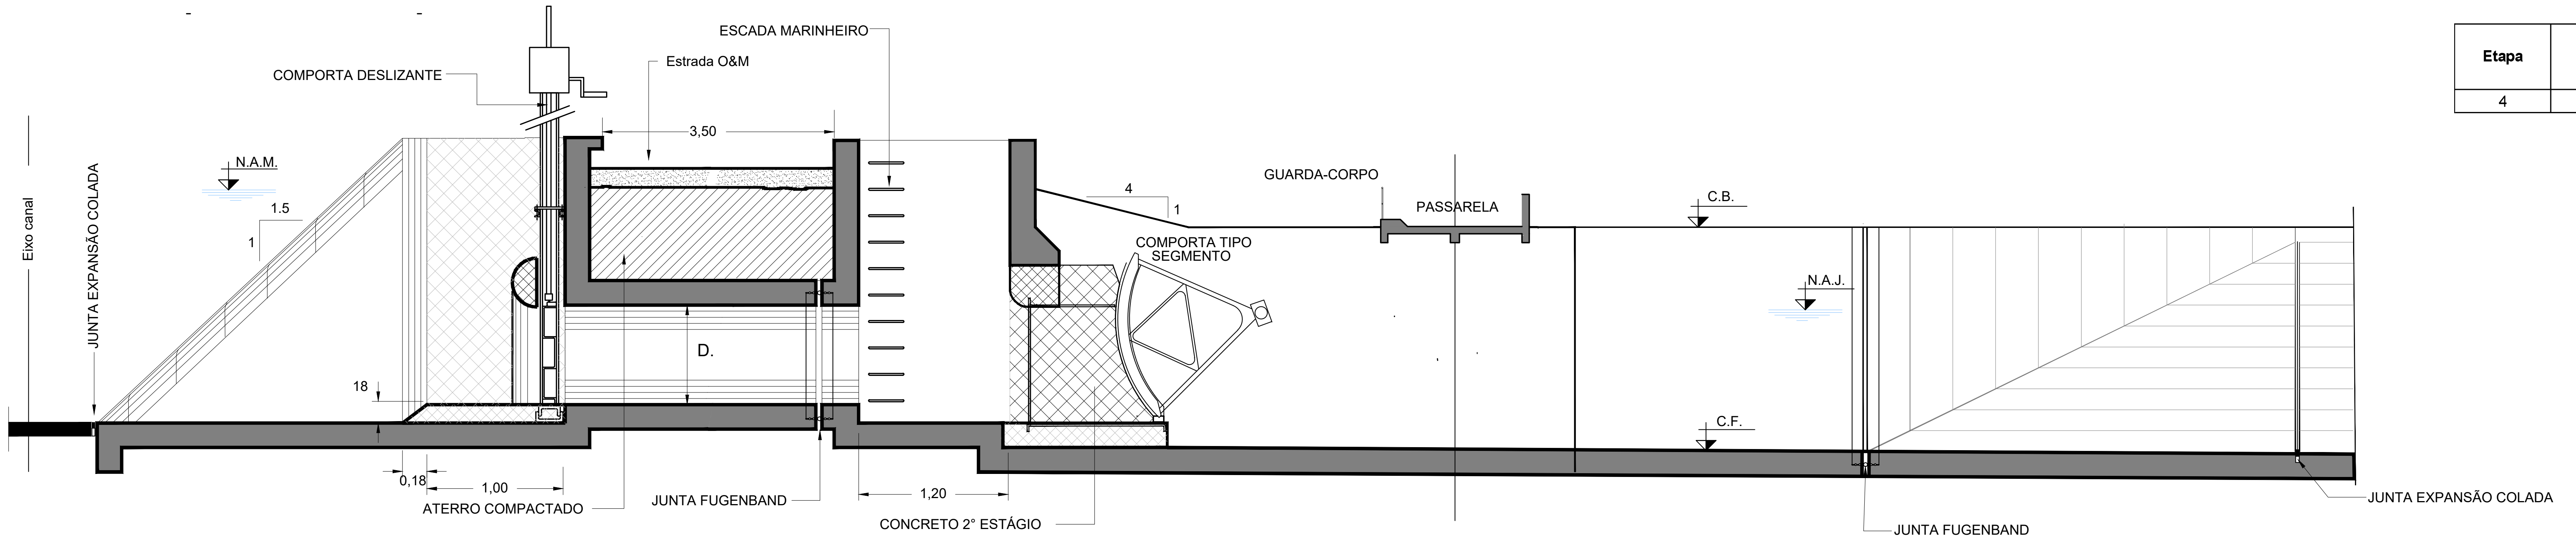
ESCADA MARINHEIRO
Estrada O&M
COMPORTA DESLIZANTE
3,50
N.A.M.
1,5
1
Eixo canal
JUNTA EXPANSÃO COLADA
D.
18
0,18
1,00
ATERRO COMPACTADO
JUNTA FUGENBAND
1,20
CONCRETO 2° ESTÁGIO
4
1
GUARDA-CORPO
PASSARELA
COMPORTA TIPO SEGMENTO
C.B.
N.A.J.
C.F.
JUNTA FUGENBAND
JUNTA EXPANSÃO COLADA

CORTE A - A

Etapa	Canal	Localizção / Estaca	Derivação	Cota de fundo (C.F.)	N.A. estático	N.A. dinâmico (N.A.M)	N.A. dinâmico (N.A.J)	Cota terreno (C.T.)	Cota da berma (C.B.)	D
		(km)		(m)	(m)	(m)	(m)	(m)	(m)	(m)
4	CP3	1+950,00	CS-23	476,61	479,10	2,30	478,83	477,00	479,12	0,50

NOTAS:

1 - MEDIDAS, COORDENADAS E ELEVAÇÕES EM METRO.

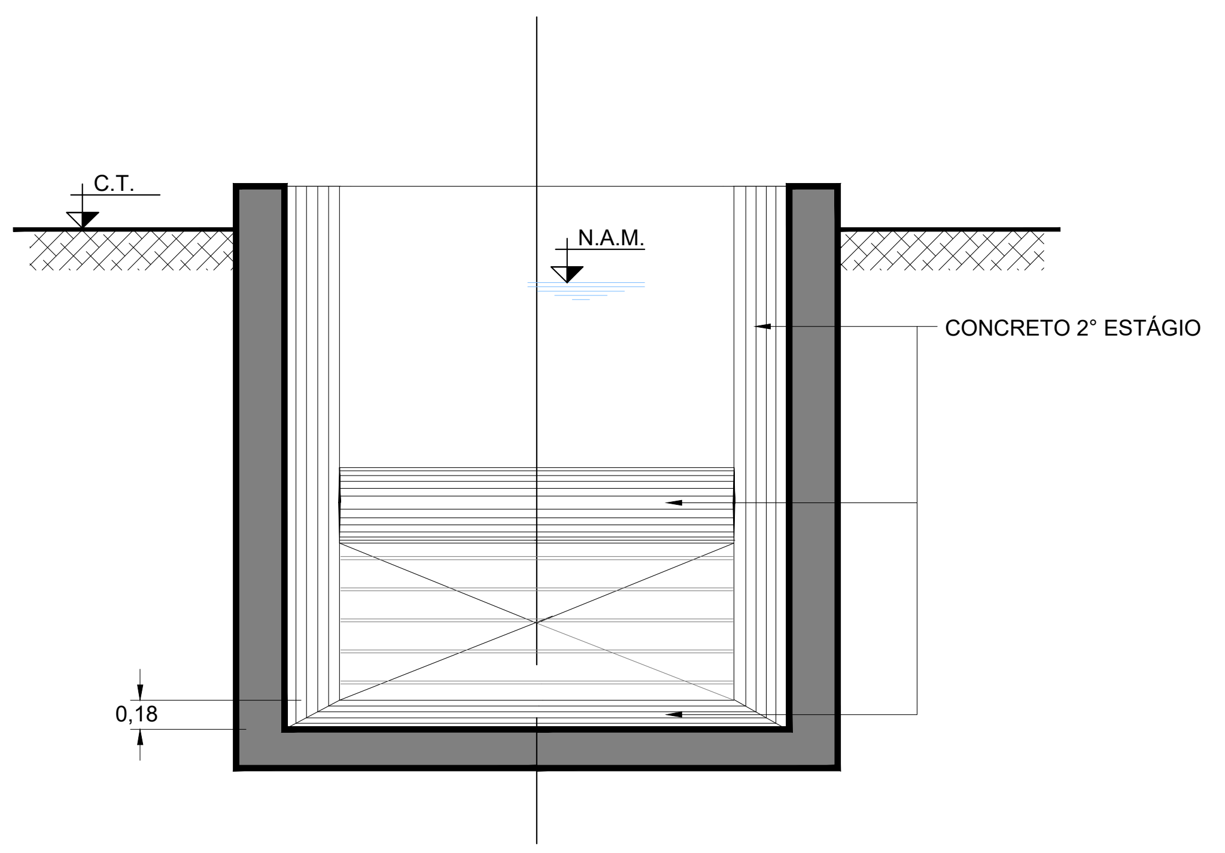
C.T.
N.A.M.
CONCRETO 2° ESTÁGIO
0,18

CORTE B - B

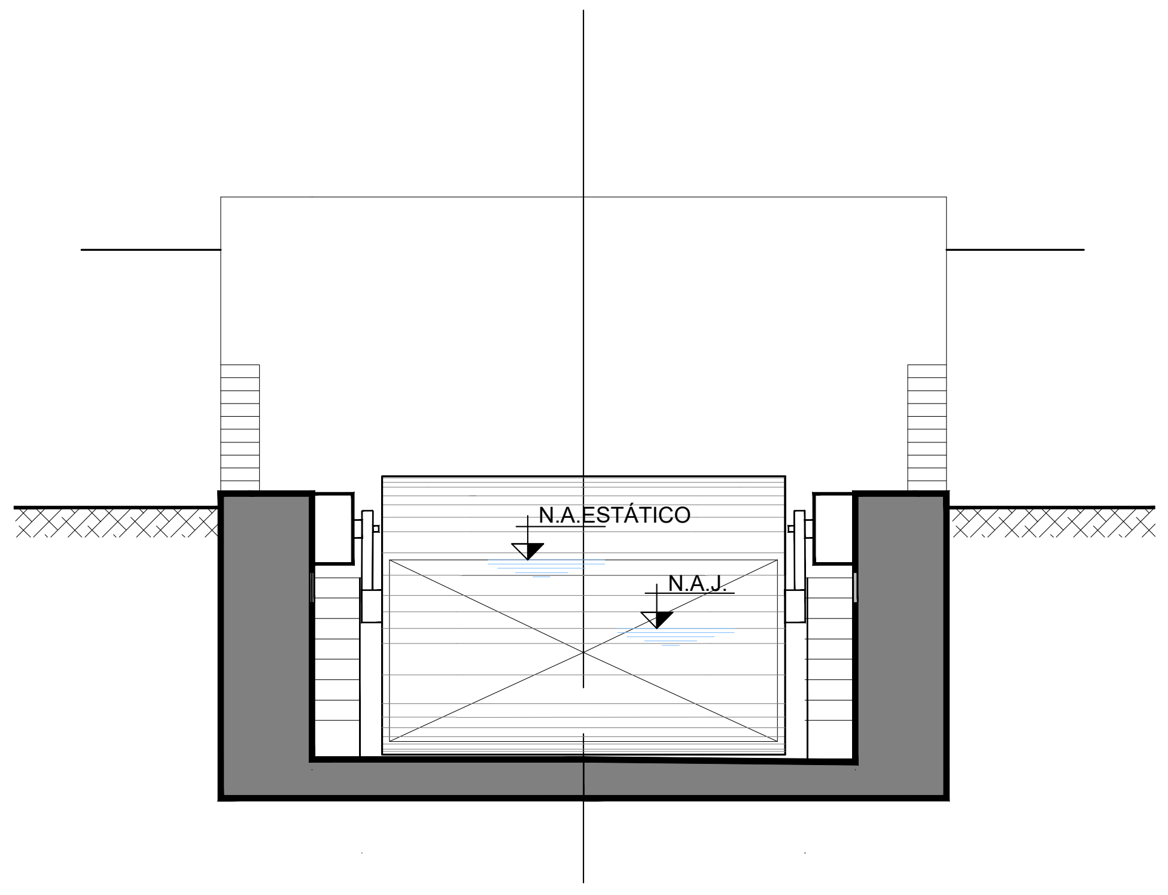
N.A.ESTÁTICO
N.A.J.

CORTE C - C

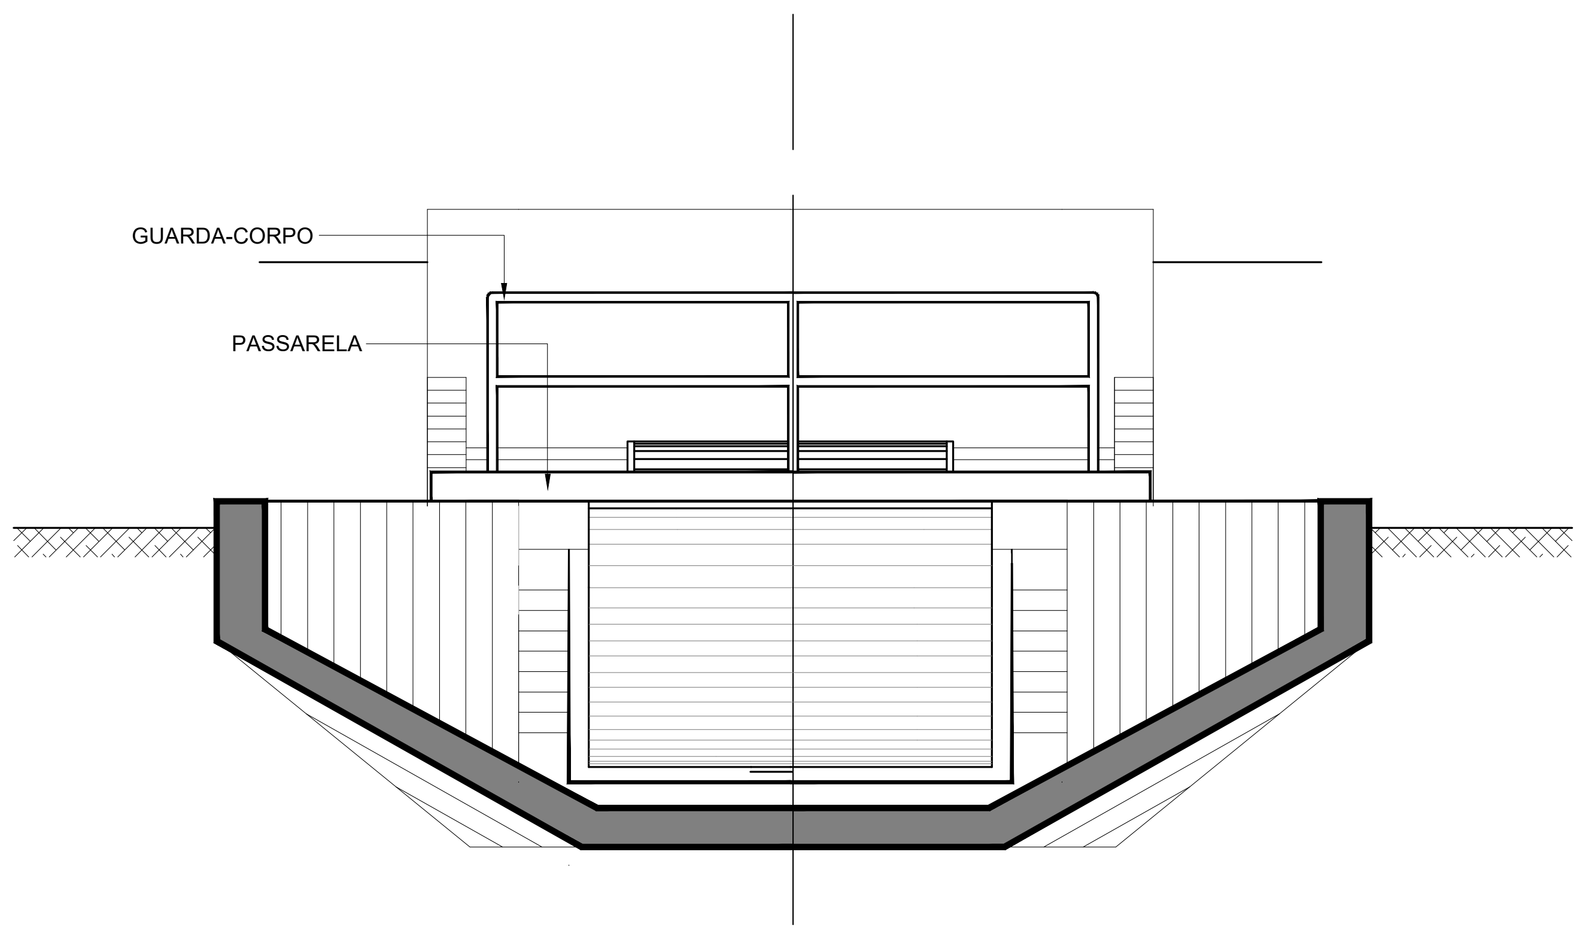
GUARDA-CORPO
PASSARELA

CORTE D - D

1	04/12/25	REVISÃO DAS VAZÕES DE PROJETO	NP	AHL	EDK	
0	19/11/25	EMISSÃO INICIAL	NP	AHL	EDK	
Revisão	Data	Descrição	Elab.	Verif.	Aprov.	Aut.

FUNDO DE DESENVOLVIMENTO DA INFRAESTRUTURA
REGIONAL SUSTENTÁVEL - FDIRS

ESTRUTURAÇÃO DE PROJETO DE CONCESSÃO DO
PERÍMETRO IRRIGADO DO JAÍBA (ETAPAS 3 E 4)

ANTEPROJETO

DERIVAÇÃO COM COMPORTA
PLANTA BAIXA
CORTES E TABELA

Finalidade de Emissão	1 Para Informação	☐ 2 Para Comentários	▨ 3 Para Aprovação	☐ 4 Para Execução	☐ 5 Como Construído	☐ 6 Para Utilização	☐ 7 Para Providências

Moysés & Pires Sociedade de advogados
ENGECORPS GrupoTYPSA
A&M
Plena Consultoria e Projetos

Data:
Elaboração:
Verificação:
Escala: sem escala
Aprovação .
Autorização .
Referência:
Revisão: 1
Desenho nº JA-DS-HI-0007