
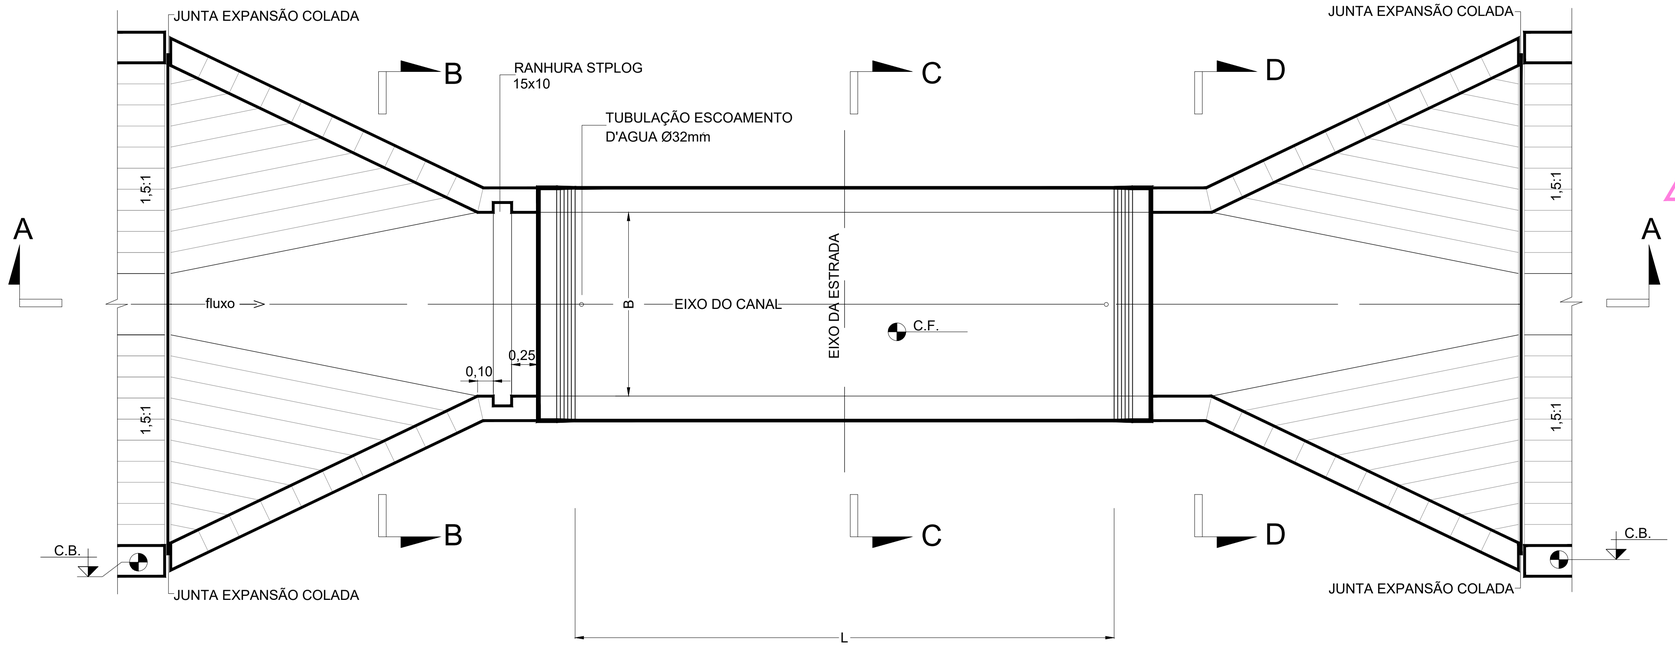



PLANTA BAIXA

Etapa	Obra	Trecho	Estaca	Extensão (L)	Cota de fundo (C.F.)	Vazão	Base (B)	Altura (H)	N.A. estático (N.A.E.)	Cota da berma (C.B.)
			(em km)	(m)	(m)	(m³/s)	(m)	(m)	(m)	(m)
3	GT1	CS19-Trecho 5	19+550	7,00	470,30	1,173	1,30	2,40	472,47	472,72
	GT2	CT1-S19-Trecho 1	5+150,00	7,00	472,55	0,605	1,30	2,10	474,49	474,69
	GT3	CT1-S19-Trecho 2	7+900,00	7,00	471,88	0,366	1,30	1,30	473,06	473,26
	GT1	CS21a - Trecho 5	15+580	7,00	461,24	1,751	2,20	1,80	463,22	463,47
	GT2	CS21a - Trecho 6	17+800,00	7,00	460,76	1,183	1,80	1,80	462,16	462,41
4	GT1	CS27	1+550,00	7,00	479,08	0,490	1,30	1,25	480,12	480,32


1

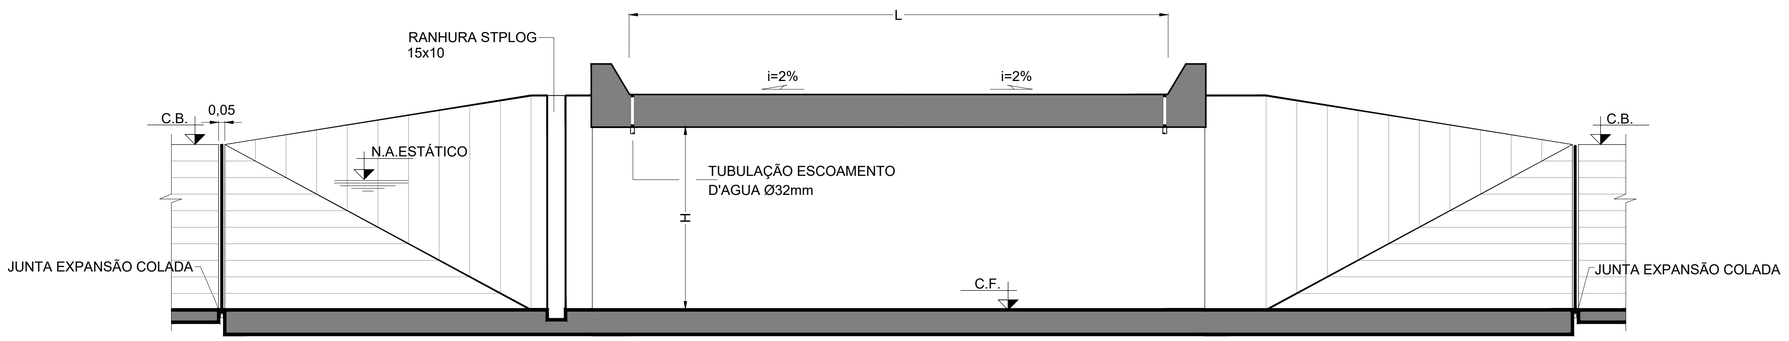


CORTE A - A

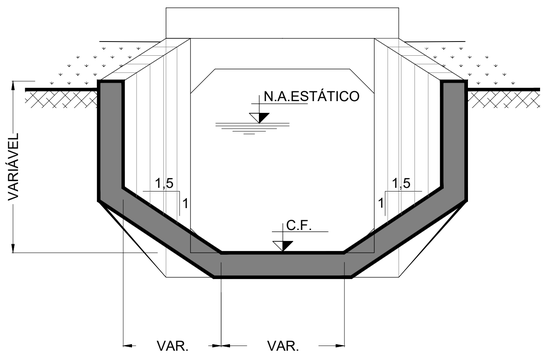

CORTE B - B

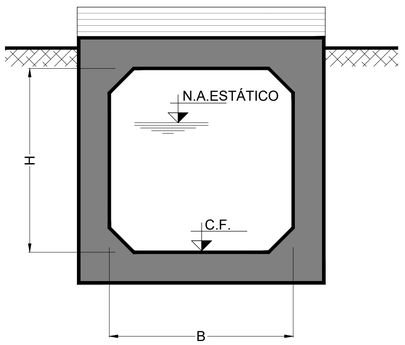

CORTE C - C

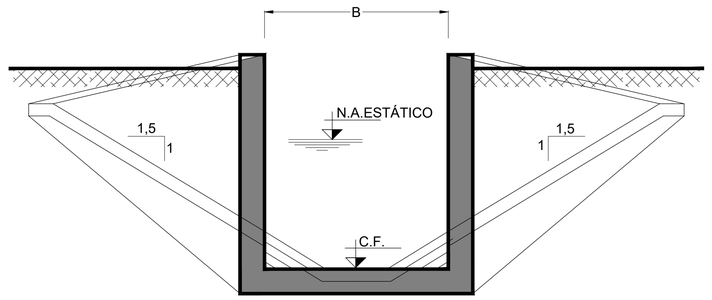

CORTE D - D

NOTAS:

1 - MEDIDAS, COORDENADAS E ELEVAÇÕES EM METRO.

REVISÕES - 1

AS ESTRUTURAS INDICADAS FORAM REPOSICIONADAS EM DECORRÊNCIA DA ALTERAÇÃO DO PERÍMETRO IRRIGÁVEL DA ETAPA 3, CONFORME SOLICITAÇÕES FEITAS APÓS CONSULTA PÚBLICA. OS PARÂMETROS DE PROJETO PERMANECEM CONFORME ESTABELECIDO NA VERSÃO ANTERIOR DO ESTUDO.

Revisão	Data	Descrição	Elab.	Verif.	Aprov.	Aut.
1	06/07/26	REPOSICIONAMENTO DAS ESTRUTURAS	NP	AHL	EDK	
0	19/11/25	EMISSÃO INICIAL	NP	AHL	EDK	

FUNDO DE DESENVOLVIMENTO DA INFRAESTRUTURA REGIONAL SUSTENTÁVEL - FDIRS

ESTRUTURAÇÃO DE PROJETO DE CONCESSÃO DO PERÍMETRO IRRIGADO DO JAÍBA (ETAPAS 3 E 4)

ANTEPROJETO

GALERIA DE TRANSPOSIÇÃO SIMPLES
PLANTA BAIXA
CORTES E TABELA

Finalidade de Emissão	1 Para Informação	2 Para Comentários	Para Aprovação	4 Para Execução	5 Como Construído	6 Para Utilização	7 Para Providências

Moysés & Pires Engenharia | ENGECORPS | Plena Consultoria e Projetos

Data:
Elaboração:
Verificação:
Escala: sem escala
Aprovação
Autorização
Referência:
Revisão: 1
Desenho nº JA-DS-HI-0008