
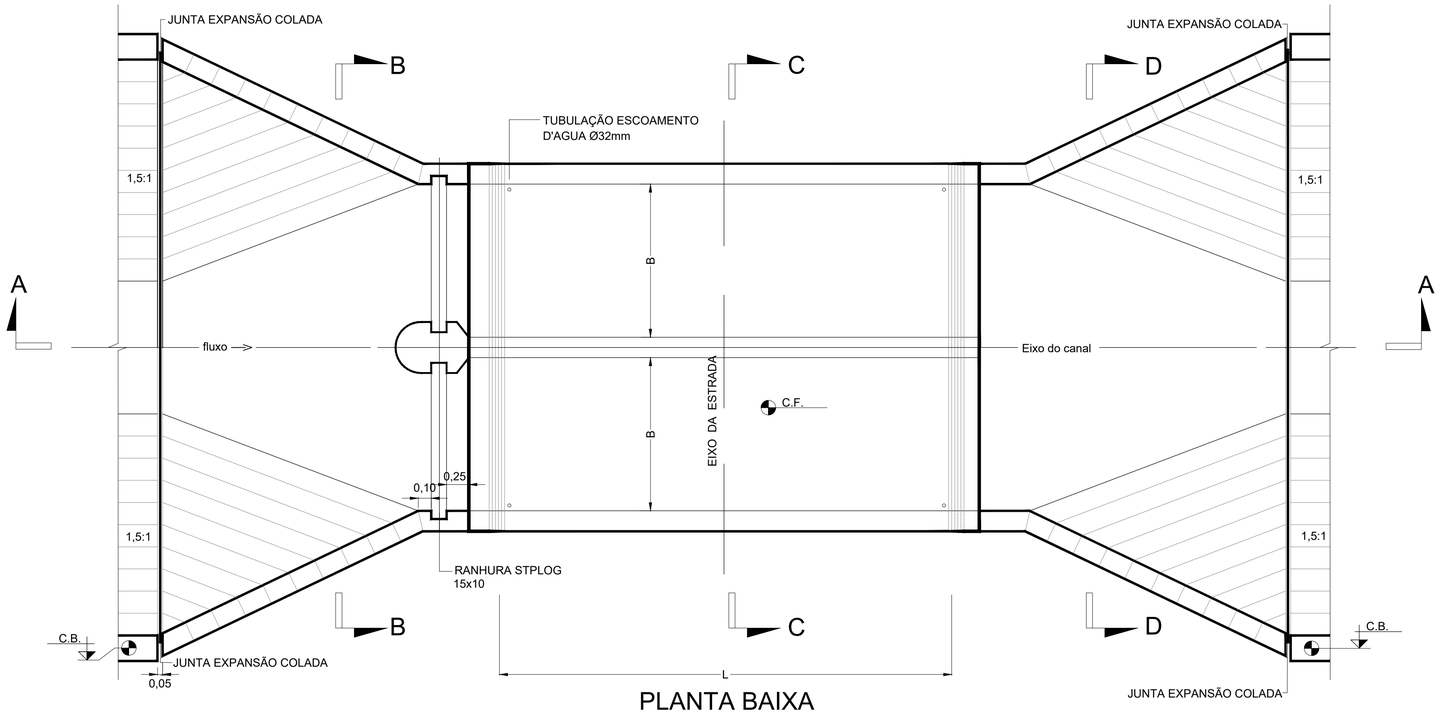



PLANTA BAIXA

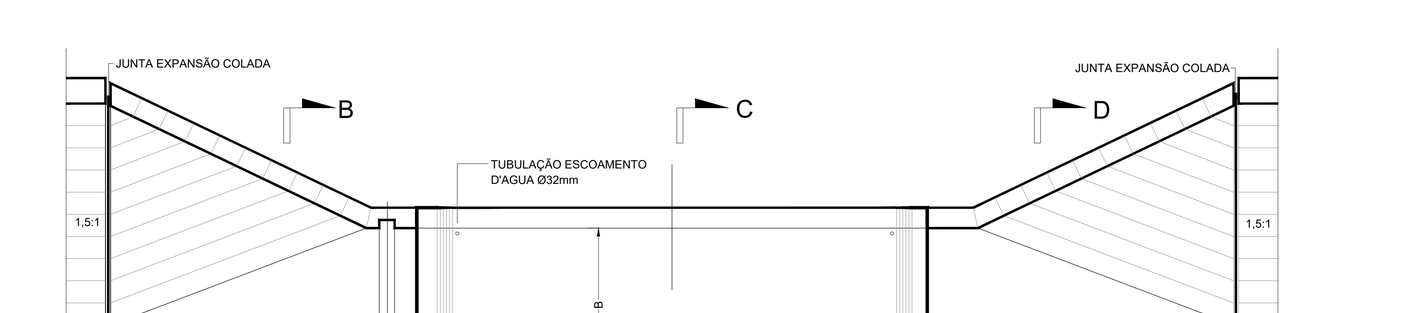


CORTE A - A

CORTE B - B

CORTE C - C

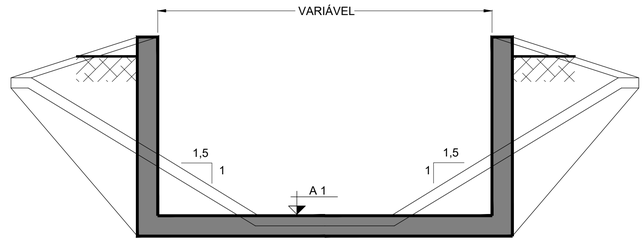

CORTE D - D

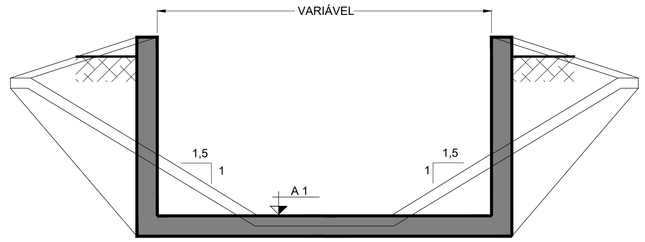

CORTE D - D

Etapa	Obra	Trecho	Estaca (em km)	Extensão (L) (m)	Cota de fundo (C.F.) (m)	Vazão (m³/s)	Base (B) (m)	Altura (H) (m)	N.A. estático (N.A.E.) (m)	Cota da berma (C.B.) (m)
3	GTD1	CS19-Trecho 1	0+850	7,00	473,58	4,997	2,20	2,20	475,44	475,74
	GTD1	CS21	1+670	7,00	476,10	5,926	2,20	2,20	478,25	478,55
	GTD2	CS21a - Trecho 1	2+050	7,00	478,00	4,535	2,20	2,20	479,98	480,28
	GTD3	CS21a - Trecho 3.1	10+350	7,00	462,17	3,204	1,80	1,80	463,77	464,02
4	GTD1	CP3 - Trecho 2	0+925,00	7,00	476,12	6,806	3,00	2,00	477,84	478,14
	GTD2	CP3a - Trecho 2	4+650,00	7,00	478,87	2,039	1,30	1,42	480,04	480,29
	GTD3	CS25 - Trecho 1	3+050,00	7,00	478,50	1,660	2,20	2,20	480,42	480,67

1

NOTAS:

1 - MEDIDAS, COORDENADAS E ELEVAÇÕES EM METRO.

REVISÕES - 1

AS ESTRUTURAS INDICADAS FORAM REPOSICIONADAS EM DECORRÊNCIA DA ALTERAÇÃO DO PERÍMETRO IRRIGÁVEL DA ETAPA 3, CONFORME SOLICITAÇÕES FEITAS APÓS CONSULTA PÚBLICA. OS PARÂMETROS DE PROJETO PERMANECEM CONFORME ESTABELECIDO NA VERSÃO ANTERIOR DO ESTUDO.

Revisão	Data	Descrição	Elab.	Verif.	Aprov.	Aut.
1	06/07/26	REPOSICIONAMENTO DAS ESTRUTURAS	NP	AHL	EDK	
0	19/11/25	EMISSÃO INICIAL	NP	AHL	EDK	

FUNDO DE DESENVOLVIMENTO DA INFRAESTRUTURA REGIONAL SUSTENTÁVEL - FDIRS

ESTRUTURAÇÃO DE PROJETO DE CONCESSÃO DO PERÍMETRO IRRIGADO DO JAÍBA (ETAPAS 3 E 4)

ANTEPROJETO

GALERIA DE TRANSPOSIÇÃO DUPLA
PLANTA BAIXA
CORTES DETALHE E TABELA

Finalidade de Emissão	1 Para Informação	2 Para Comentários	Para Aprovação	4 Para Execução	5 Como Construído	6 Para Utilização	7 Para Providências

Moyses & Pires / Engecorps / Plena / AGM	Data:	Elaboração:		Verificação:
	Escala: sem escala	Aprovação		Autorização
Referência:		Revisão: 1	Desenho nº JA-DS-HI-0009	