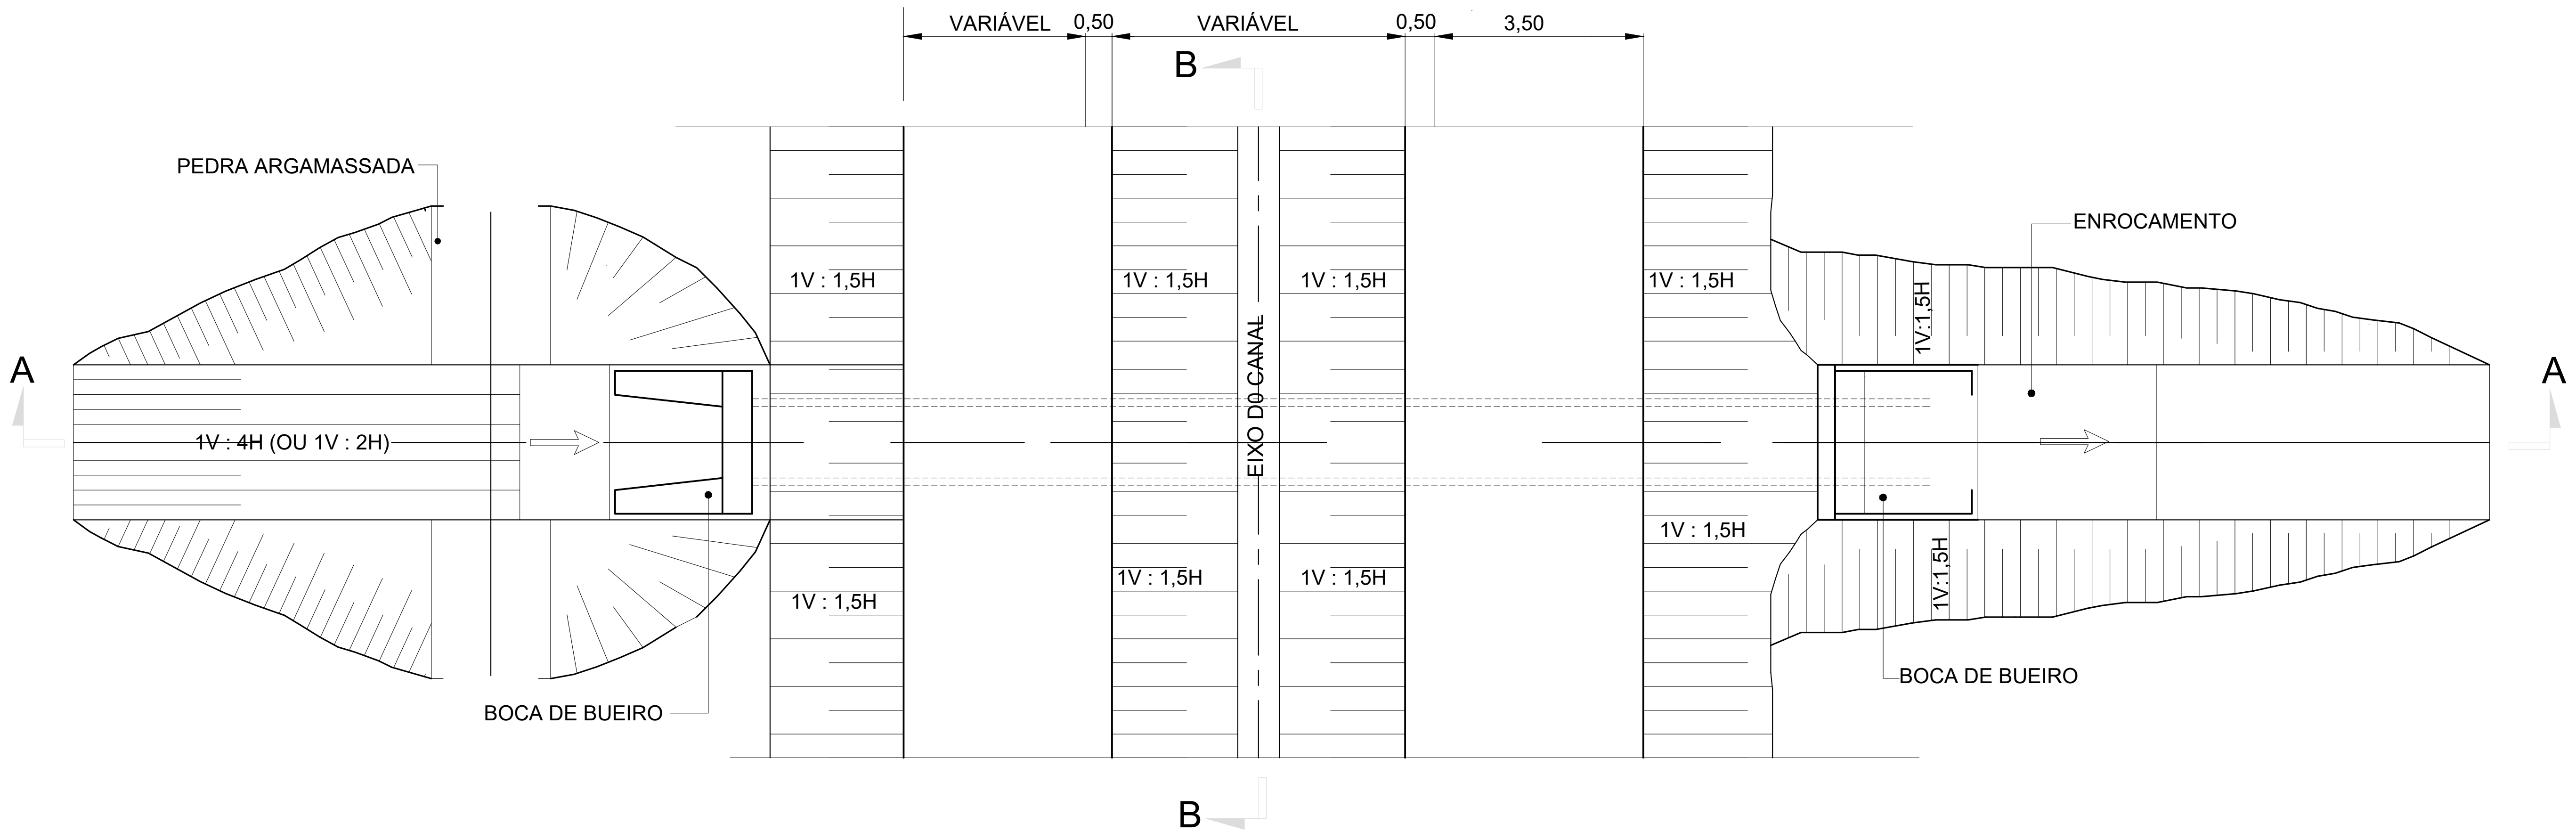

PLANTA BAIXA
Esc. 1:100

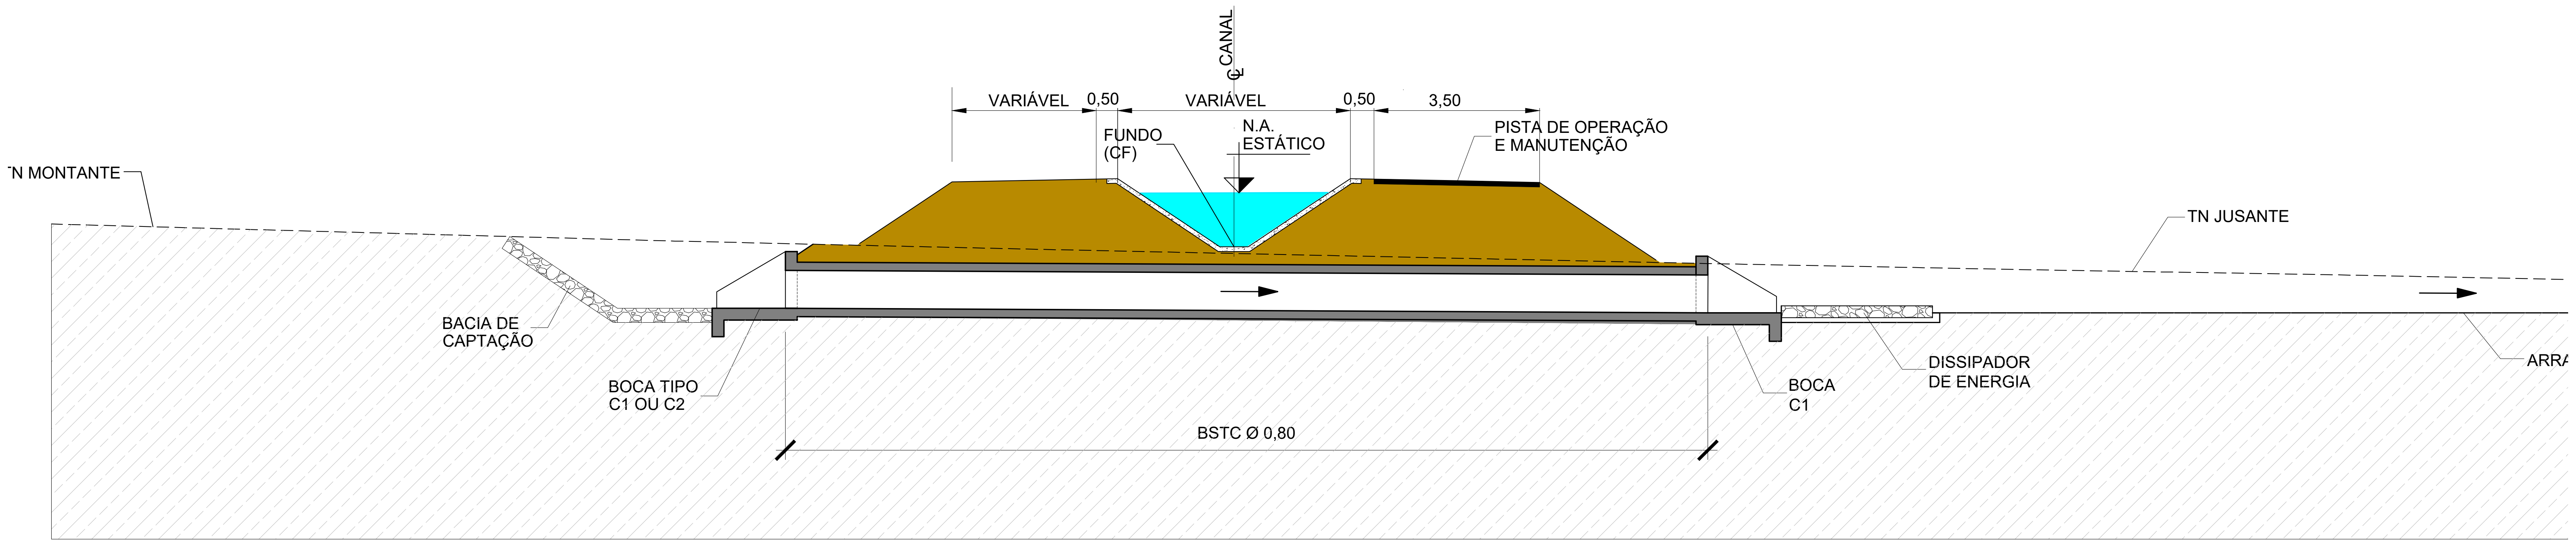

CORTE A - A
ESC. 1:500

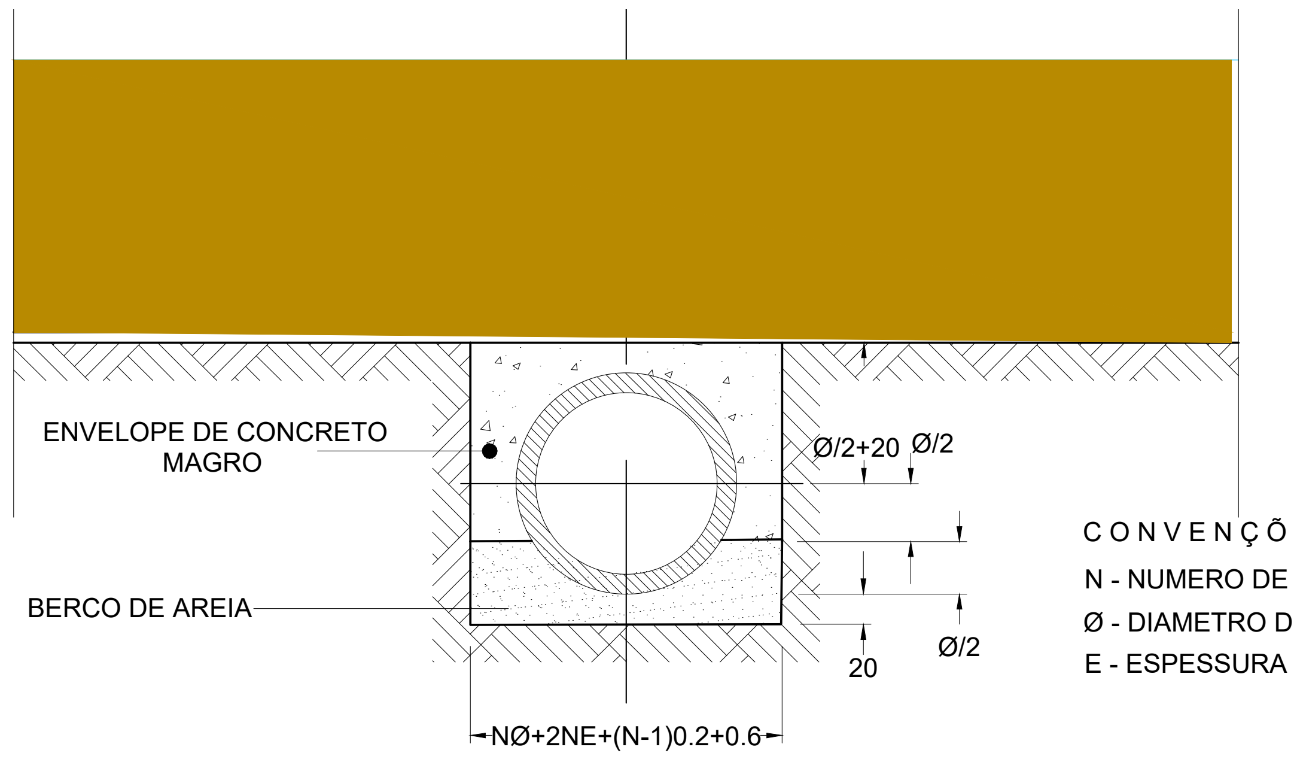

CONVENÇÕES:

N - NUMERO DE BUEIROS
Ø - DIAMETRO DO BUEIRO
E - ESPESSURA DO BUEIRO

CORTE B - B

QUADRO RESUMO - BUEIROS J3

BUEIRO	LOCALIZAÇÃO DO TRECHO				DIÂM. (m)	DECLIV. (m/m)	COMPRI-MENTO (m)
	CANAL	KM		TIPO			
BC-01	CANAL CS19	4 +	200,00	BSTC	0,80	0,005	25,50
BC-02	CANAL CS19	7 +	83,00	BSTC	0,80	0,01	22,00
BC-03	CANAL CS19	9 +	196,00	BSTC	0,80	0,005	25,00
BC-04	CANAL CS19	14 +	600,00	BSTC	0,80	0,005	20,00
BC-05	CANAL CS19	15 +	590,00	BSTC	0,80	0,005	19,50
BC-06	CANAL CS19	18 +	250,00	BSTC	0,80	0,005	22,50
BC-07	CANAL CS19	19 +	600,00	BSTC	0,80	0,005	24,50
BC-08	CANAL CT2-CS21a	0 +	920,00	BSTC	0,80	0,033	18,50
BC-09	CANAL CS21a	1 +	882,00	BSTC	0,80	0,005	26,00
BC-10	CANAL CS21a	5 +	200,00	BSTC	0,80	0,015	35,00
BC-11	CANAL CS21a	7 +	400,00	BSTC	0,80	0,007	36,00
BC-12	CANAL CS21a	7 +	887,00	BSTC	0,80	0,005	27,50
BC-13	CANAL CS21a	17 +	0,00	BSTC	0,80	0,025	21,00

1

QUADRO RESUMO - BUEIROS J4

BUEIRO	LOCALIZAÇÃO DO TRECHO				DIÂM. (m)	DECLIV. (m/m)	COMPRI-MENTO (m)
	CANAL	KM		TIPO			
BC-01	CANAL CS25	1 +	273,00	273,00	0,80	0,005	26,00
BC-02	CANAL CS25	2 +	548,00	548,00	0,80	0,005	25,50
BC-03	CANAL CS25	3 +	0,00	0,00	0,80	0,005	26,50
BC-04	CANAL CS25	4 +	811,00	811,00	0,80	0,005	35,00
BC-05	CANAL CS25	5 +	600,00	600,00	0,80	0,005	31,00
BC-06	CANAL CP3a	0 +	38,00	38,00	0,80	0,005	27,00
BC-07	CANAL CP3a	2 +	122,00	122,00	0,80	0,036	28,50
BC-08	CANAL CP3a	2 +	600,00	600,00	0,80	0,007	28,00
BC-09	CANAL CP3a	7 +	550,00	550,00	0,80	0,005	21,00
BC-10	CANAL CS27	2 +	389,00	389,00	0,80	0,005	19,50

REVISÕES - 1

AS ESTRUTURAS INDICADAS FORAM REPOSICIONADAS EM DECORRÊNCIA DA ALTERAÇÃO DO PERÍMETRO IRRIGÁVEL DA ETAPA 3, CONFORME SOLICITAÇÕES FEITAS APÓS CONSULTA PÚBLICA. OS PARÂMETROS DE PROJETO PERMANECEM CONFORME ESTABELECIDO NA VERSÃO ANTERIOR DO ESTUDO.

Revisão	Data	Descrição	Elab.	Verif.	Aprov.	Aut.
-	-	-	-	-	-	-
-	-	-	-	-	-	-
-	-	-	-	-	-	-
1	06/07/26	REPOSICIONAMENTO DAS ESTRUTURAS	NP	AHL	EDK	
0	19/11/25	EMISSÃO INICIAL	NP	AHL	EDK	

FUNDO DE DESENVOLVIMENTO DA INFRAESTRUTURA
REGIONAL SUSTENTÁVEL - FDIRS

ESTRUTURAÇÃO DE PROJETO DE CONCESSÃO DO
PERÍMETRO IRRIGADO DO JAÍBA (ETAPAS 3 E 4)

ANTEPROJETO

BUEIRO DE GREIDE
PLANTA BAIXA
CORTES

Finalidade de Emissão	1 Para Informação	2 Para Comentários	3 Para Aprovação	4 Para Execução	5 Como Construído	6 Para Utilização	7 Para Providências

Moysés & Pires Sociedade de advogados
ENGECORPS GrupoTYPSA
A&M
Plena Consultoria e Projetos

Data: / /
Elaboração:
Verificação:
Escala: INDICADA
Aprovação - -
Autorização - -
Referência:
Revisão: 1
Desenho nº JA-DS-HI-0010