



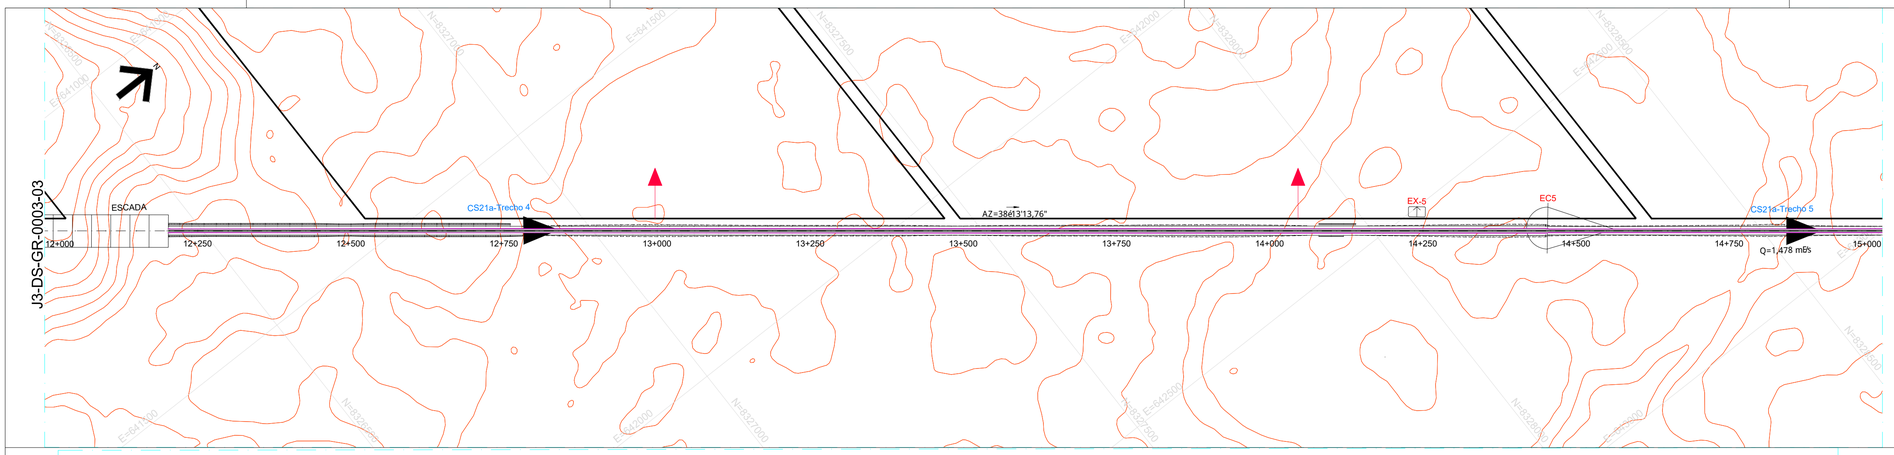


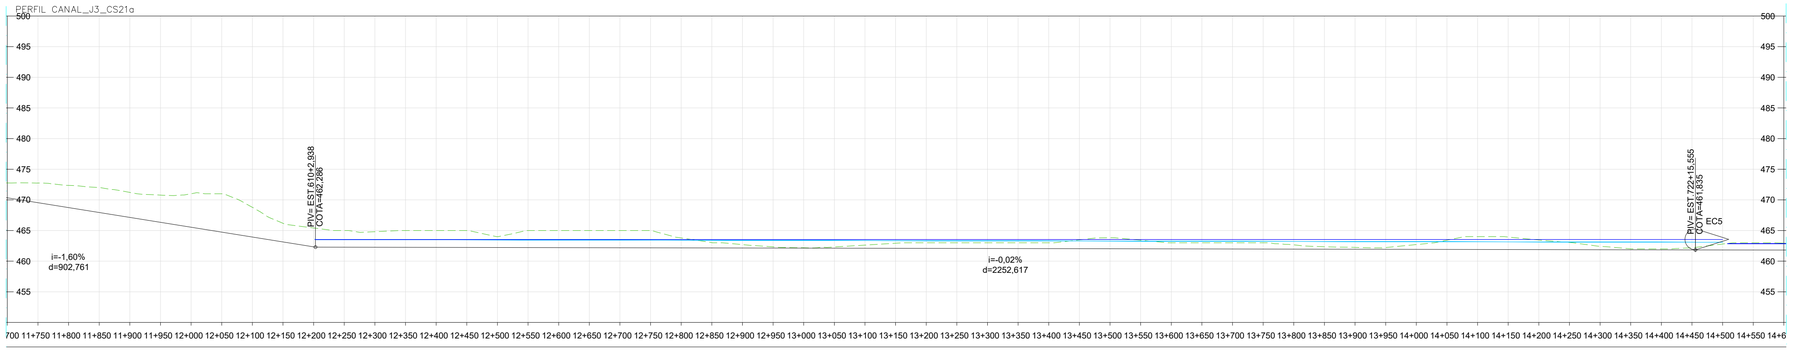

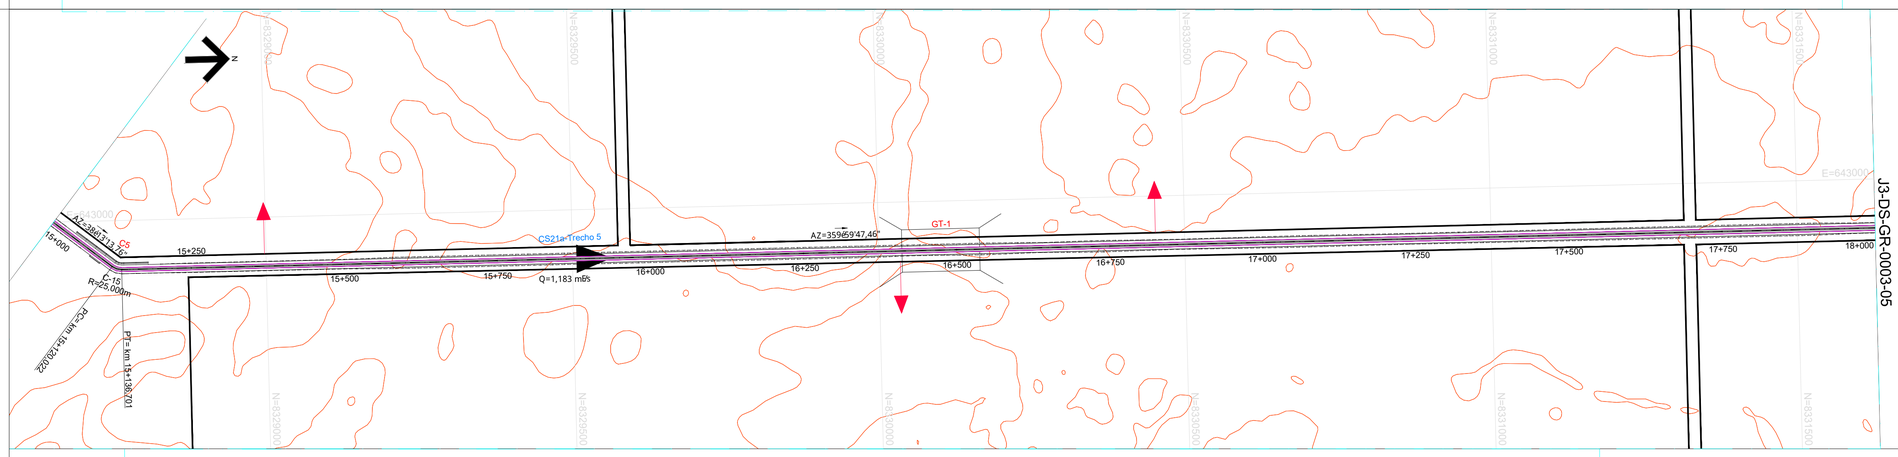

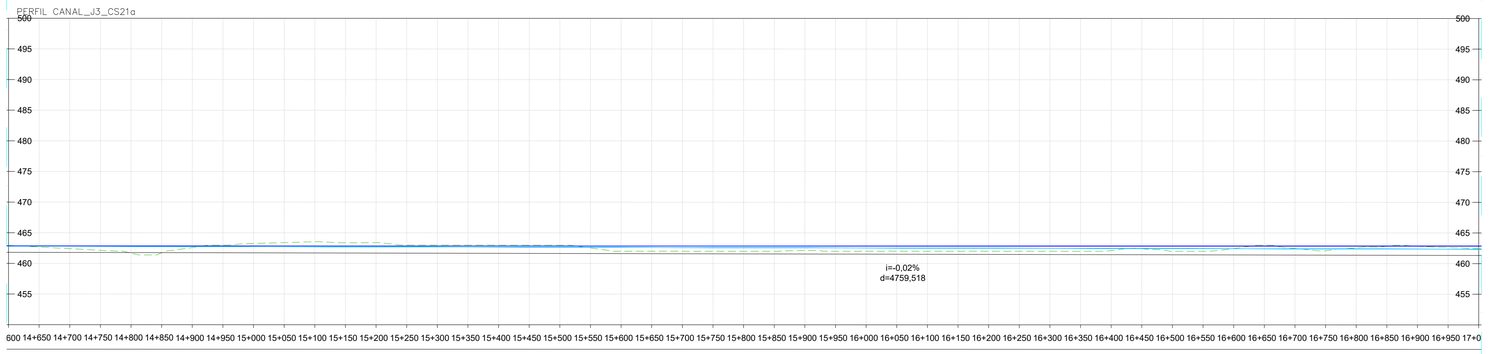

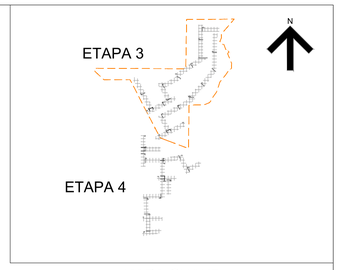

MAPA CHAVE

LEGENDA:

PLANTA:

- Canal Adutor
- Curvas de Nível Mestra
- Curvas de Nível Intermediárias
- Cursos d'Água
- Estradas
- Estrutura de Controle
- Valeta de Proteção de Corte e de Aterro
- Sarjeta Triangular de Corte
- Dissipador de Energia
- Bueiro Simples Tubular de Concreto
- Boca Simples
- Bacia de Captação

PERFIL:

- Terreno Natural
- Topo da Berma
- Nível D'água Dinâmico
- Nível D'água Estático
- Fundo do Canal
- Estrutura de Controle

NOTAS:

01 - MEDIDAS EM METROS, EXETO INDICAÇÃO CONTRÁRIA;
02 - SISTEMA DE COORDENADAS: DATUM SIRGAS 2000, UTM-23S;
03 - TERRENO OBTIDO DO LEVANTAMENTO TOPOGRÁFICO;

REVISÕES:
REVISÃO 1 - REVISÃO DO PERÍMETRO IRRIGÁVEL DA ETAPA 3, CONFORME SOLICITAÇÕES FEITAS APÓS CONSULTA PÚBLICA.

Revisão	Data	Descrição	Elab.	Verif.	Aprov.	Aut.
-	-	-	-	-	-	-
-	-	-	-	-	-	-
-	-	-	-	-	-	-
01	23/07/26	REVISÃO DO PERÍMETRO DE IRRIGAÇÃO DA ETAPA 3	JBA	AHL	EDK	-
00	21/11/25	EMISSÃO INICIAL	JOP	AHL	EDK	-

FUNDO DE DESENVOLVIMENTO DA INFRAESTRUTURA REGIONAL SUSTENTÁVEL - FDIRS

ESTRUTURAÇÃO DE PROJETO DE CONCESSÃO DO PERÍMETRO IRRIGADO DO JAÍBA (ETAPAS 3 E 4)

ANTEPROJETO

SISTEMA ADUTOR
PLANTA E PERFIL - ETAPA 3
FOLHA 04

Finalidade de Emissão	1 Para Informação	2 Para Comentários	3 Para Aprovação	4 Para Execução	5 Como Construído	6 Para Utilização	7 Para Provid. ncias

Moyses & Pires | ENGECORPS | Plena Consultoria e Projetos

Data: 21/11/25	Elaboração:		Verificação:
Escala: 1:5000 / 1:5000 (H:V)	Aprovação	- / -	Autorização: - / -
Referência:	Revisão: 01	Desenho nº	J3-DS-HI-0006