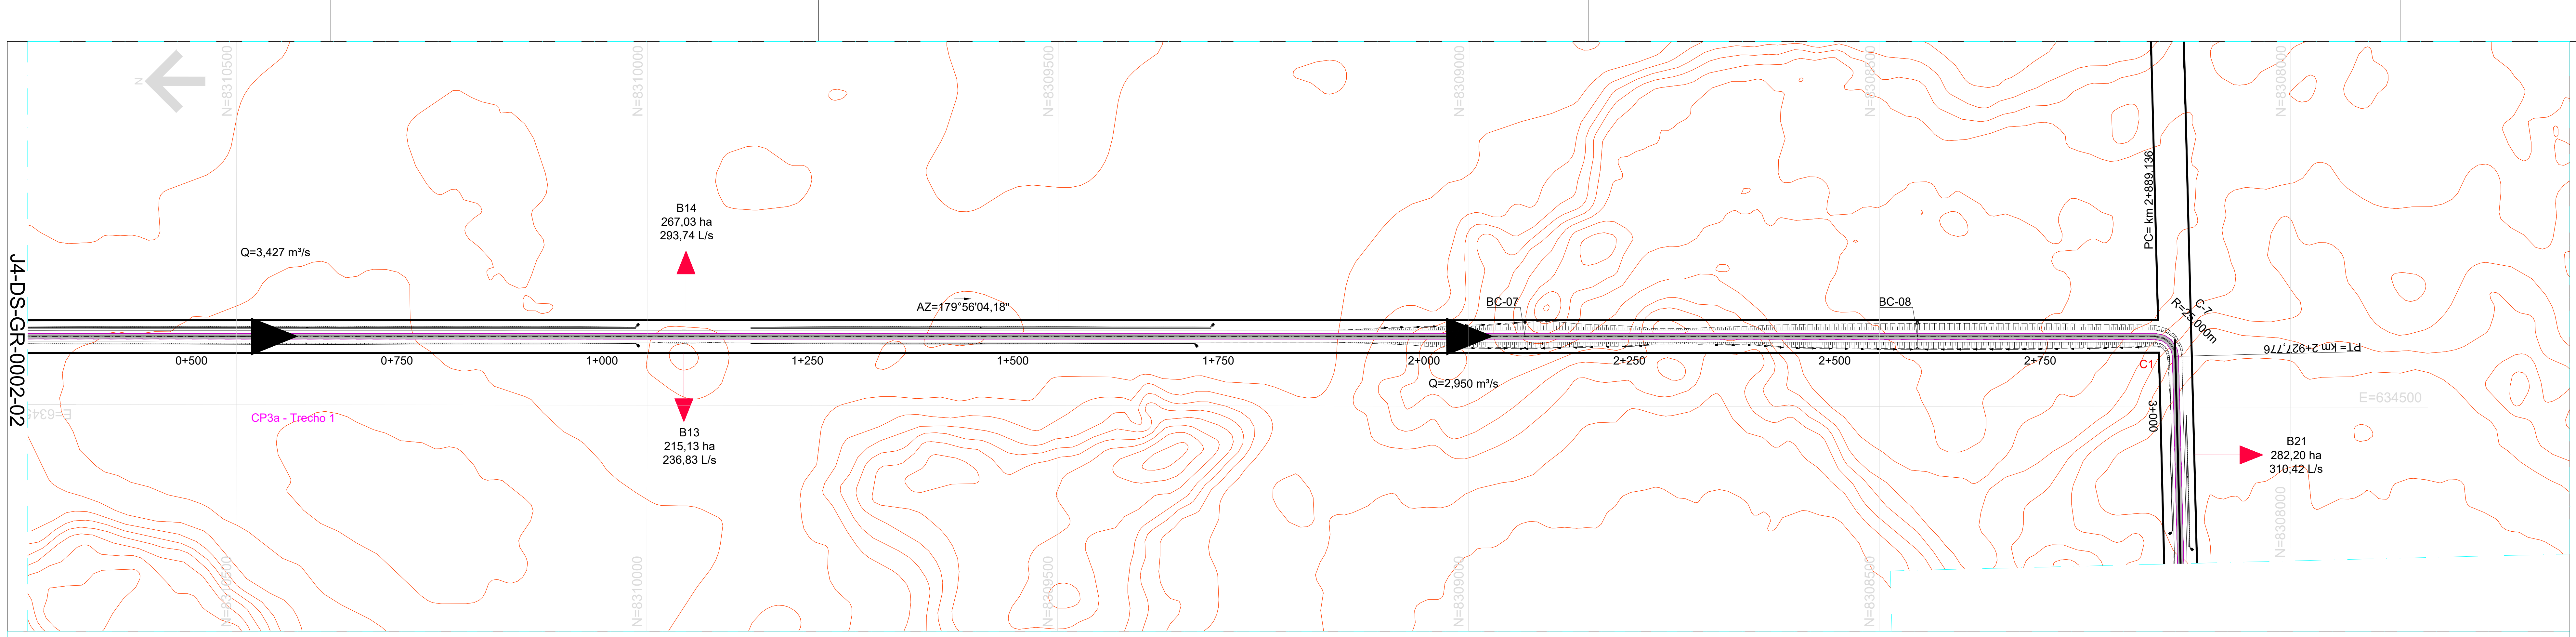
J4-DS-GR-0002-02
Q=3,427 m³/s
B14
267,03 ha
293,74 L/s
AZ=179°56'04,18"
BC-07
BC-08
0+500
0+750
1+000
1+250
1+500
1+750
2+000
2+250
2+500
2+750
B13
215,13 ha
236,83 L/s
CP3a - Trecho 1
Q=2,950 m³/s
PC= km 2+889,136
C-7
R=25,000m
PT= km 2+927,776
C1
3+000
B21
282,20 ha
310,42 L/s
E=634500
N=8310500
N=8310000
N=8309500
N=8309000
N=8308500
N=8308000

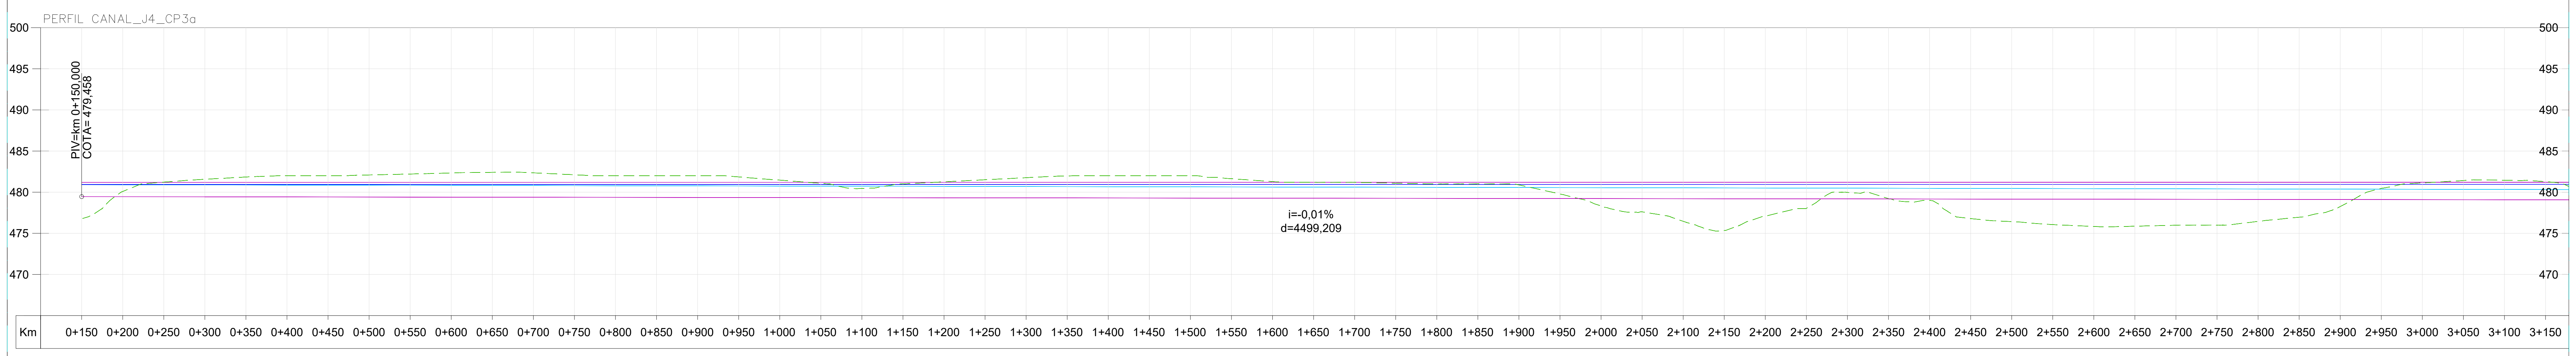

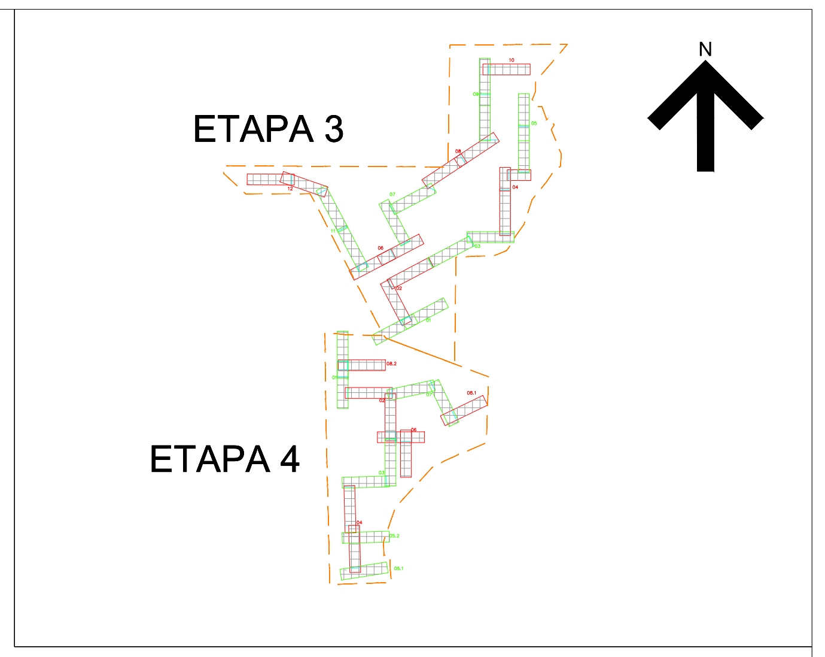
ETAPA 3
ETAPA 4
N

MAPA CHAVE

LEGENDA:

PLANTA:

▤	Canal Adutor
～	Curvas de Nível Mestra
～	Curvas de Nível Intermediárias
～	Cursos d'Água
═ ═	Estradas
◁	Estrutura de Controle
– ►	Valeta de Proteção de Corte e de Aterro
—►—	Sarjeta Triangular de Corte
▨	Dissipador de Energia
- -►- -	Bueiro Simples Tubular de Concreto
◁	Boca Simples
▨	Bacia de Captação

PERFIL:

～	Terreno Natural
—	Topo da Berma
—	Nível D'água Dinâmico
—	Nível D'água Estático
—	Fundo do Canal
◁	Estrutura de Controle

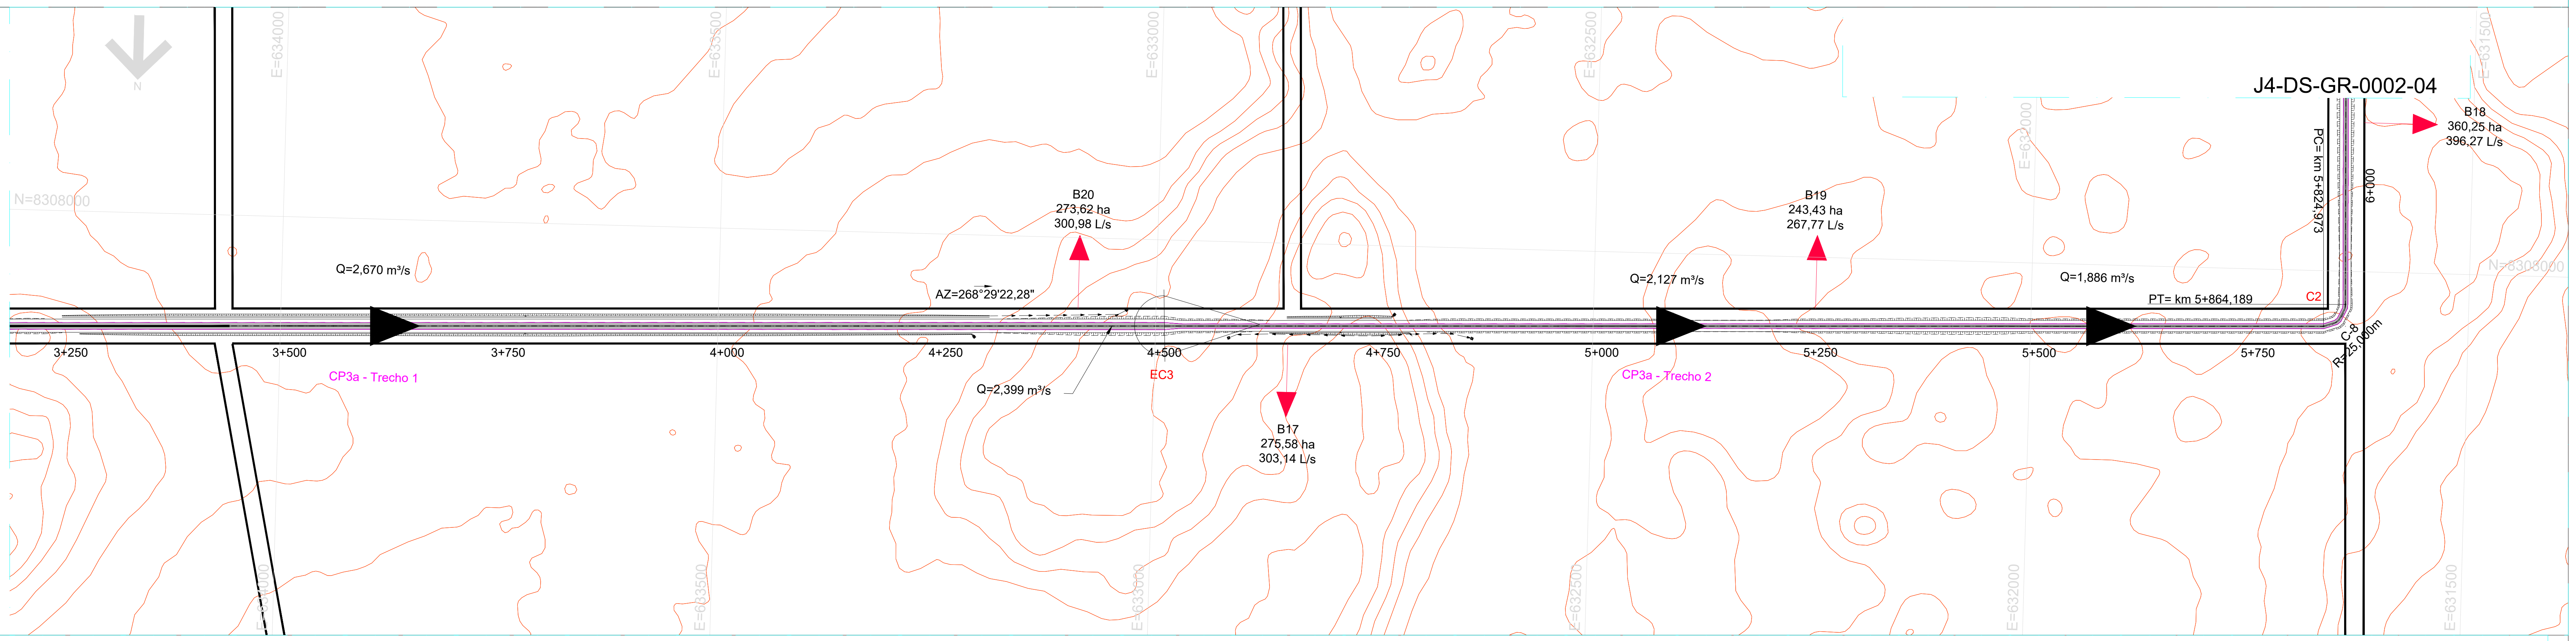
N
N=8308000
Q=2,670 m³/s
AZ=268°29'22,28"
B20
273,62 ha
300,98 L/s
3+250
3+500
3+750
4+000
4+250
4+500
4+750
5+000
5+250
5+500
5+750
CP3a - Trecho 1
Q=2,399 m³/s
EC3
B17
275,58 ha
303,14 L/s
Q=2,127 m³/s
B19
243,43 ha
267,77 L/s
Q=1,886 m³/s
PT= km 5+864,189
C2
CP3a - Trecho 2
J4-DS-GR-0002-04
PC= km 5+824,973
6+000
C-8
R=25,000m
B18
360,25 ha
396,27 L/s
E=634000
E=633500
E=633000
E=632500
E=632000
E=631500

NOTAS:

01 - MEDIDAS EM METROS, EXETO INDICAÇÃO CONTRÁRIA;
02 - SISTEMA DE COORDENADAS: DATUM SIRGAS 2000, UTM-23S;
03 - TERRENO OBTIDO DO LEVANTAMENTO TOPOGRÁFICO;

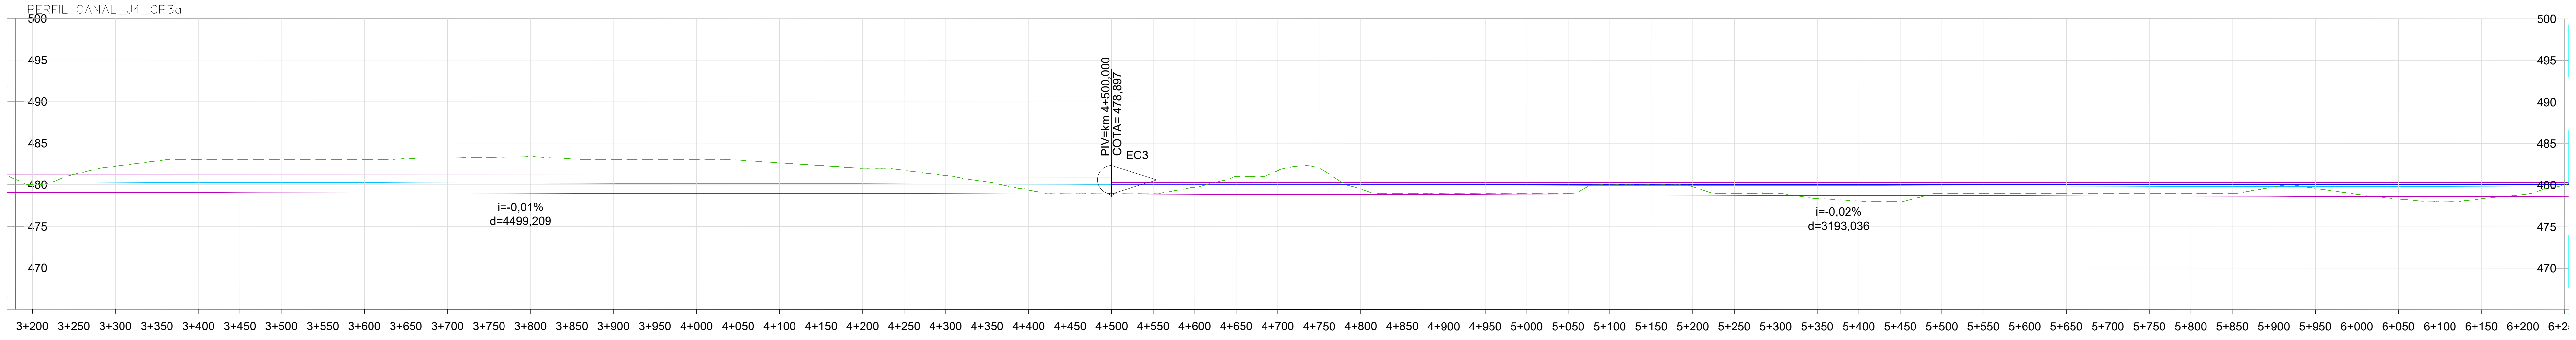

-	-	-	-	-	-	-
-	-	-	-	-	-	-
-	-	-	-	-	-	-
-	-	-	-	-	-	-
00	21/11/25	EMISSÃO INICIAL	JOP	AHL	EDK	-
Revisão	Data	Descrição	Elab.	Verif.	Aprov.	Aut.

FUNDO DE DESENVOLVIMENTO DA INFRAESTRUTURA
REGIONAL SUSTENTÁVEL - FDIRS

ESTRUTURAÇÃO DE PROJETO DE CONCESSÃO DO
PERÍMETRO IRRIGADO DO JAÍBA (ETAPAS 3 E 4)

ANTEPROJETO

SISTEMA ADUTOR
PLANTA E PERFIL - ETAPA 4
FOLHA 03

Finalidade de Emissão	1 Para Informação	2 Para Comentários	3 Para Aprovação	4 Para Execução	5 Como Construído	6 Para Utilização	7 Para Providências

Moysés & Pires Sociedade de advogados
ENGECORPS GrupoTYPSA
A&M
Plena Consultoria e Projetos

Data: 21/11/25	Elaboração:		Verificação:
Escala: 1:500 / 1:500 (H:V)	Aprovação	- -	Autorização - -
Referência:	Revisão: 00	Desenho nº	J4-DS-HI-005