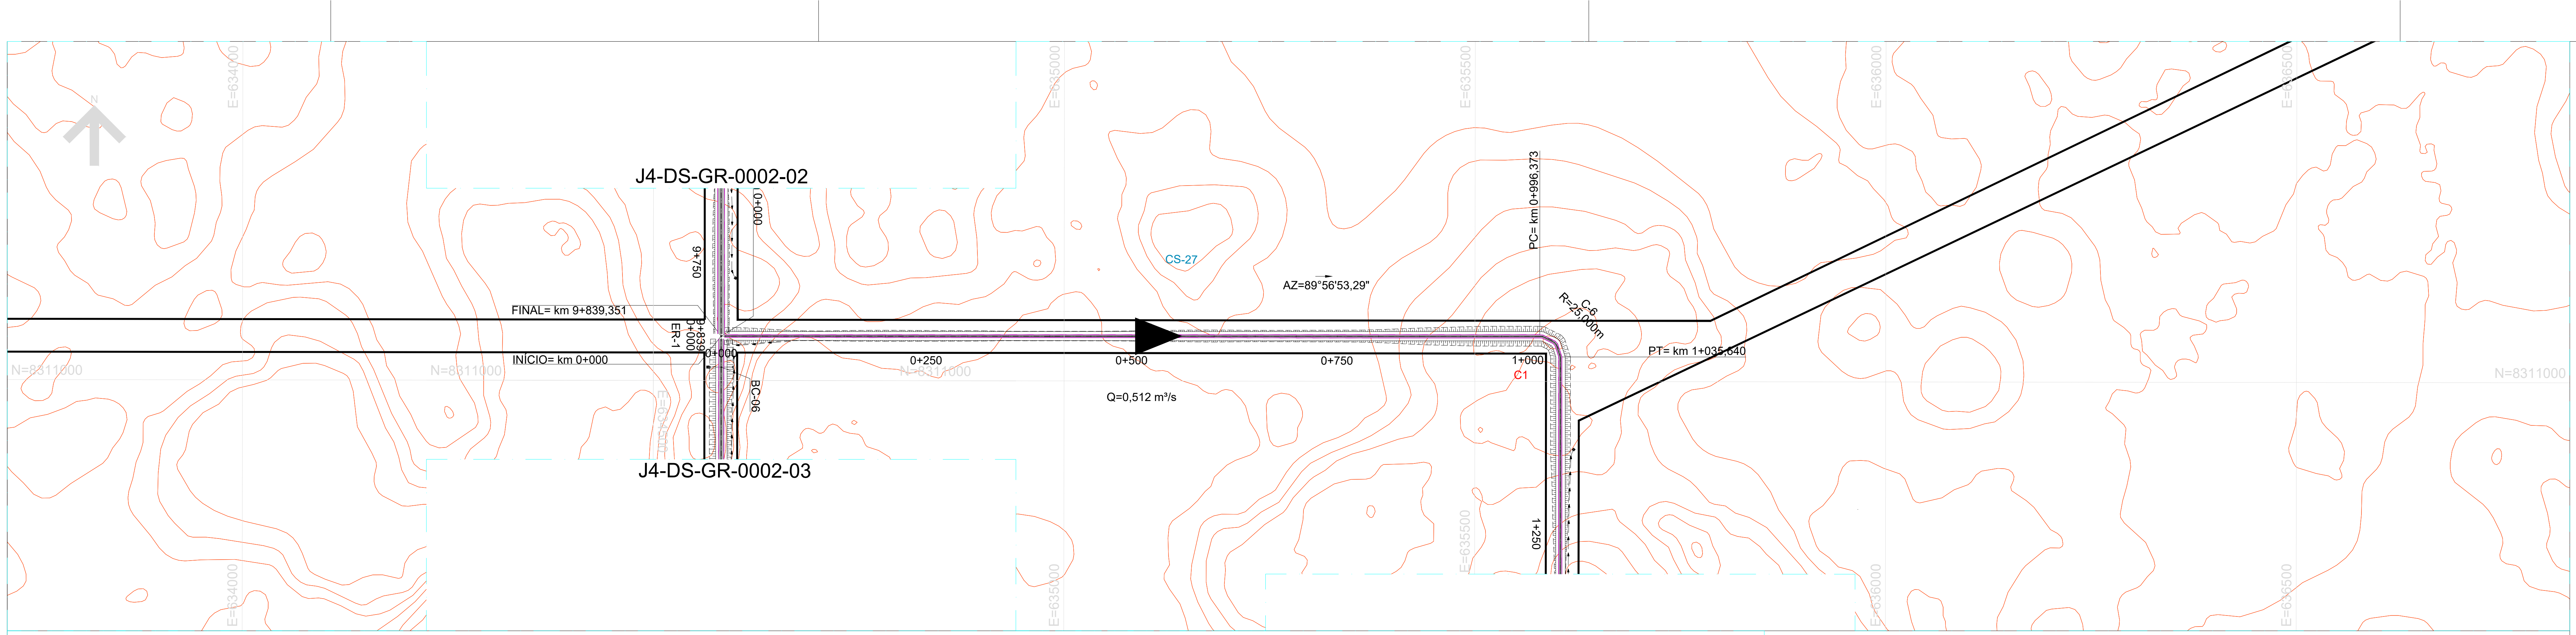
J4-DS-GR-0002-02
J4-DS-GR-0002-03
CS-27
AZ=89°56'53,29"
PC= km 0+996,373
C-6
R=25,000m
PT= km 1+035,640
FINAL= km 9+839,351
INÍCIO= km 0+000
9+750
0+000
9+839
0+000
ER-1
BC-06
0+250
0+500
0+750
1+000
1+250
C1
Q=0,512 m³/s
N=8311000
E=634500
E=635000
E=635500
E=636000
E=636500

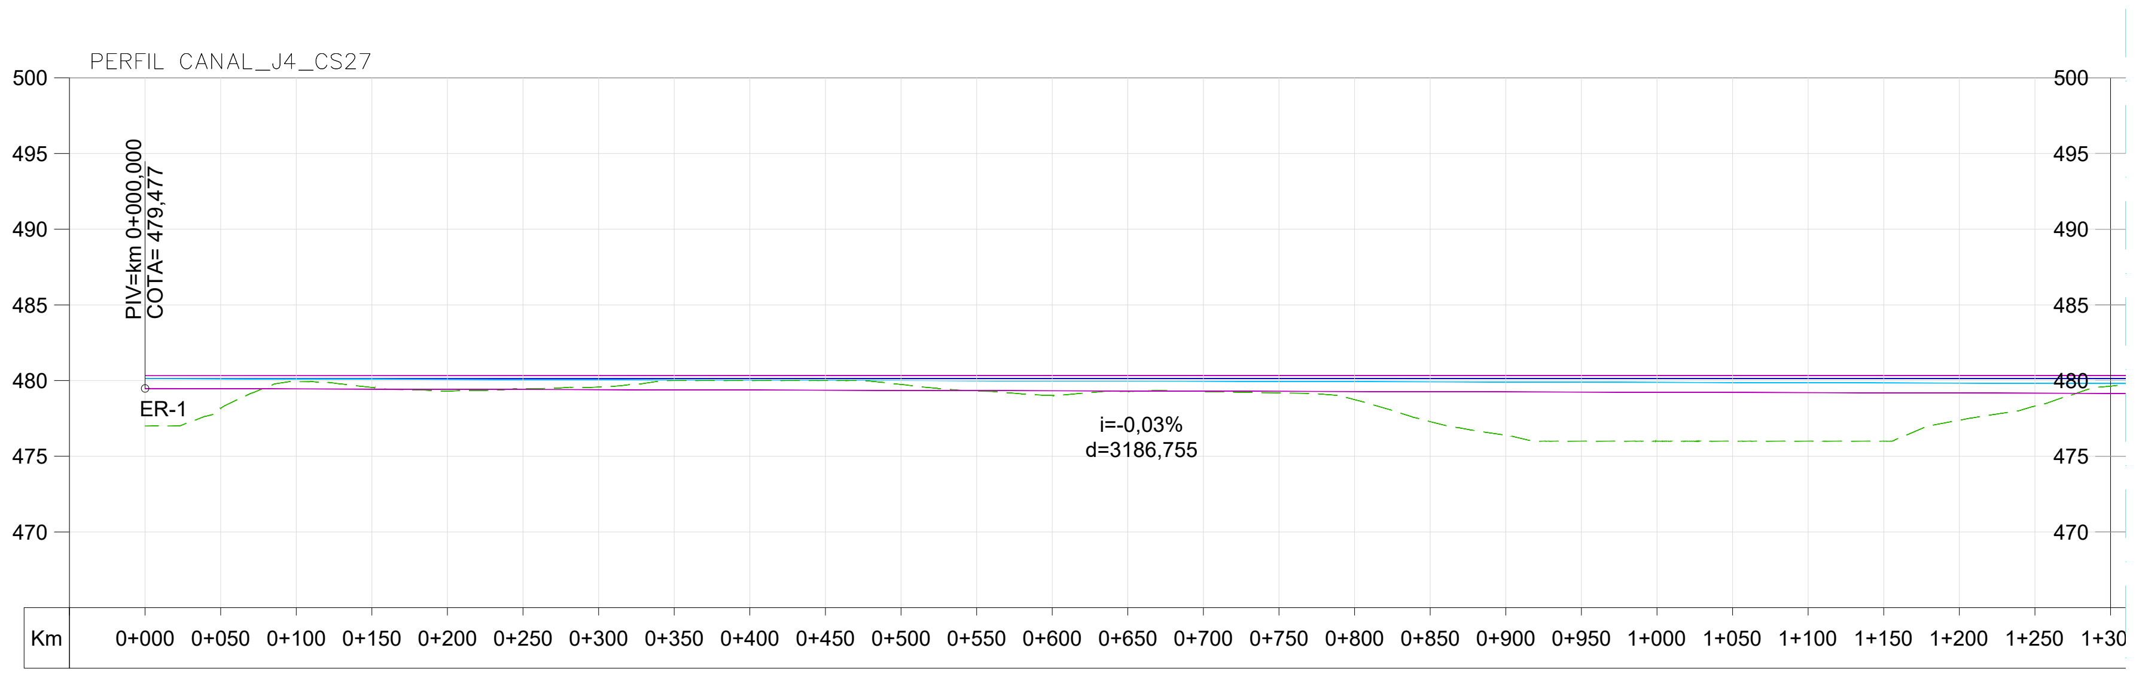
PERFIL CANAL_J4_CS27
500
495
490
485
480
475
470
PIV=km 0+000,000
COTA= 479,477
ER-1
i=-0,03%
d=3186,755
Km
0+000 0+050 0+100 0+150 0+200 0+250 0+300 0+350 0+400 0+450 0+500 0+550 0+600 0+650 0+700 0+750 0+800 0+850 0+900 0+950 1+000 1+050 1+100 1+150 1+200 1+250 1+30

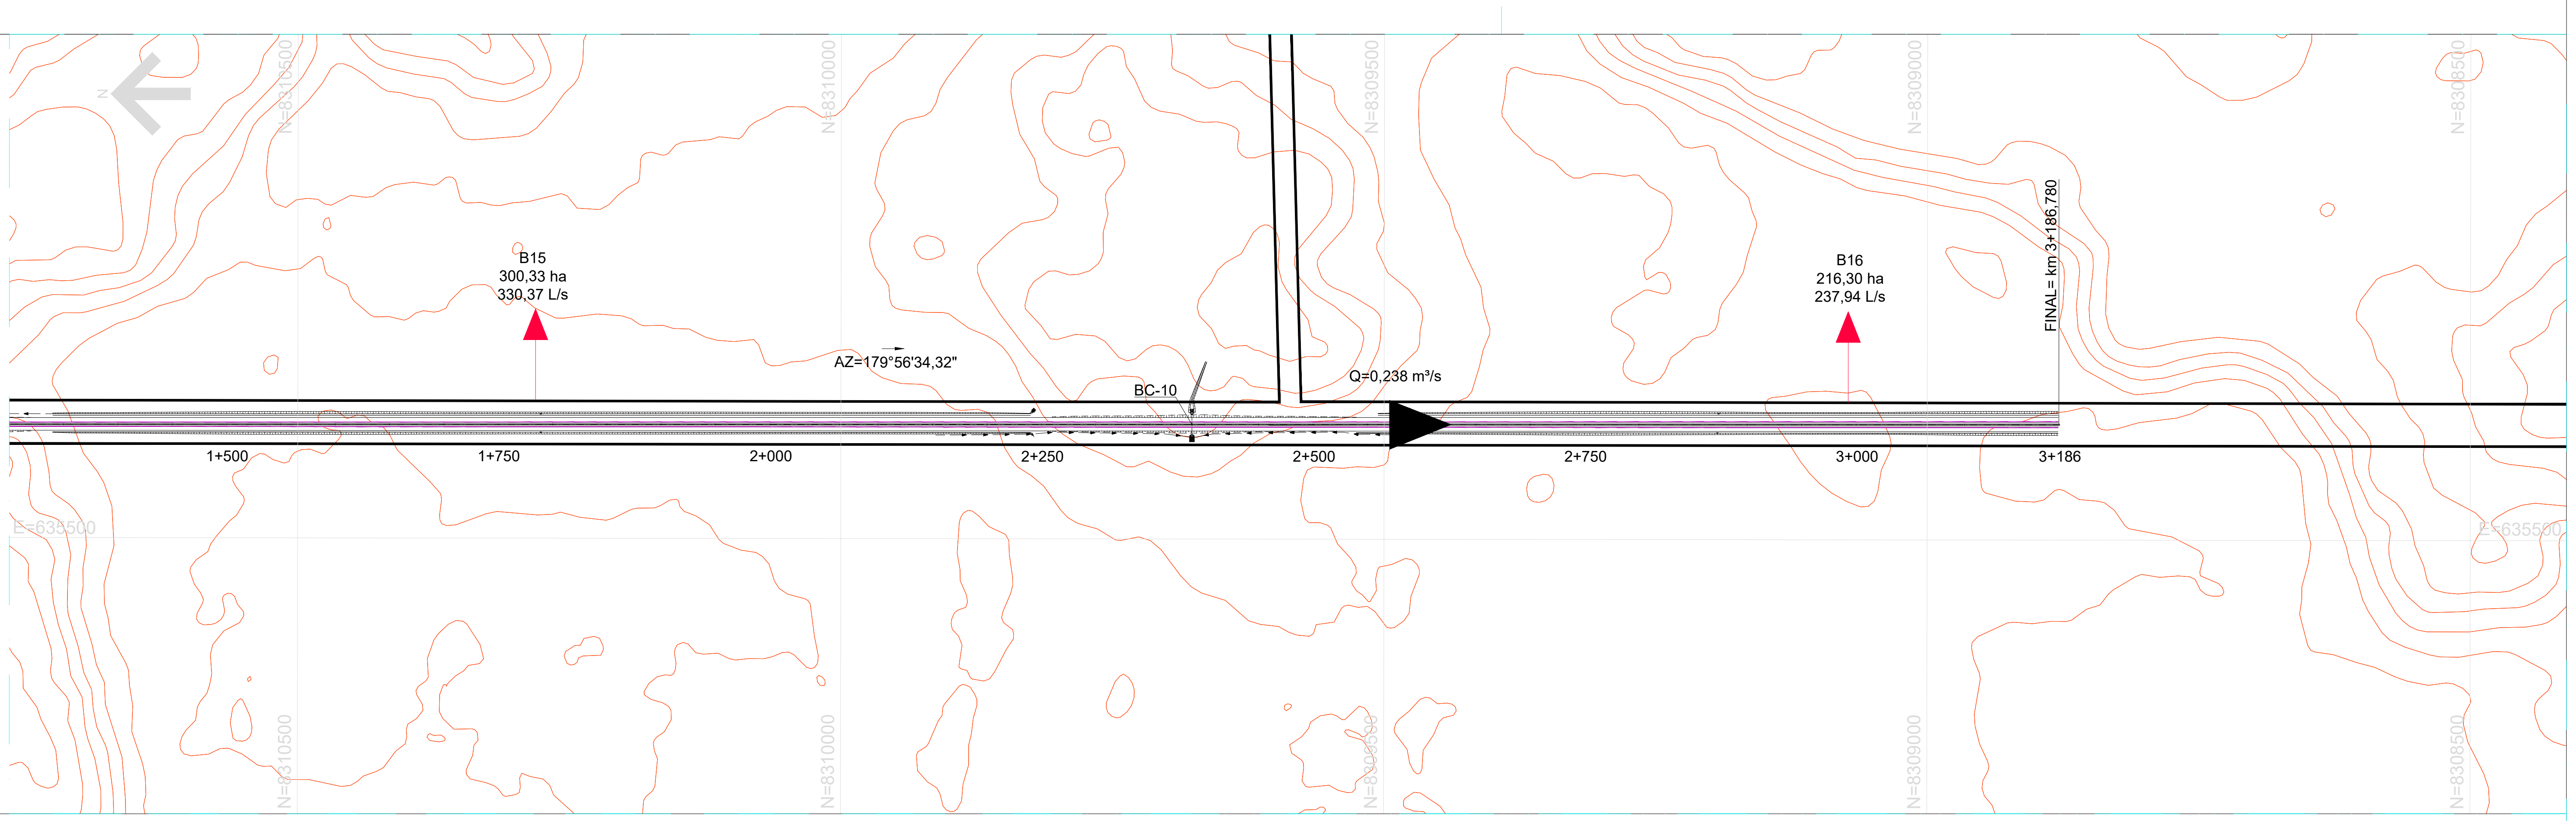
B15
300,33 ha
330,37 L/s
B16
216,30 ha
237,94 L/s
FINAL= km 3+186,780
AZ=179°56'34,32"
BC-10
Q=0,238 m³/s
1+500
1+750
2+000
2+250
2+500
2+750
3+000
3+186
N=8310500
N=8310000
N=8309500
N=8309000
N=8308500
E=635500

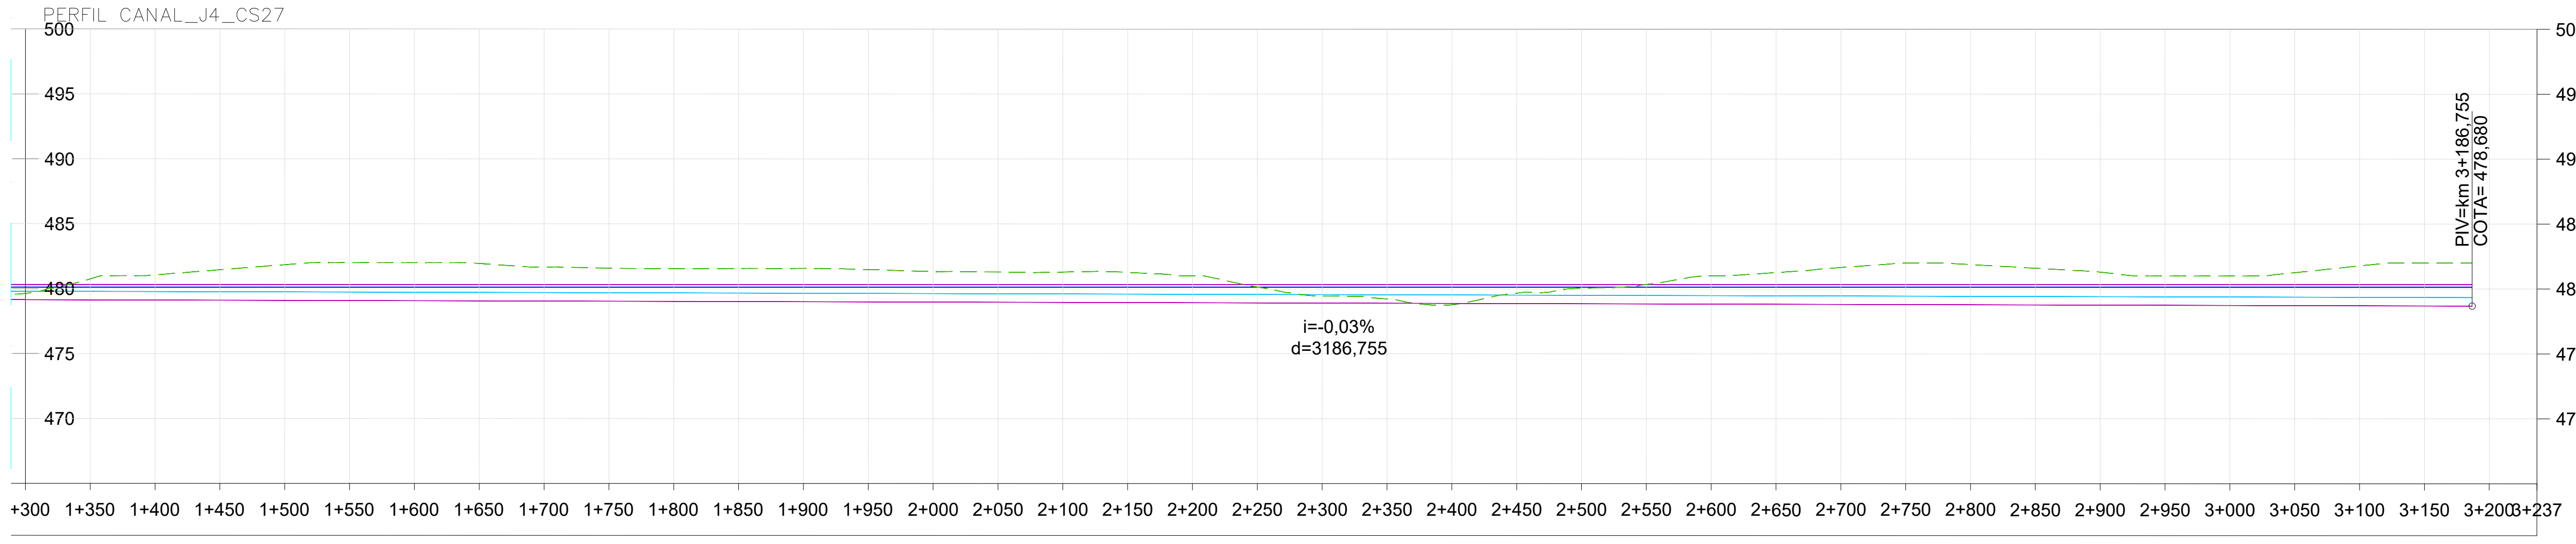
PERFIL CANAL_J4_CS27
500
495
490
485
480
475
470
PIV=km 3+186,755
COTA= 478,680
i=-0,03%
d=3186,755
+300 1+350 1+400 1+450 1+500 1+550 1+600 1+650 1+700 1+750 1+800 1+850 1+900 1+950 2+000 2+050 2+100 2+150 2+200 2+250 2+300 2+350 2+400 2+450 2+500 2+550 2+600 2+650 2+700 2+750 2+800 2+850 2+900 2+950 3+000 3+050 3+100 3+150 3+200 3+237

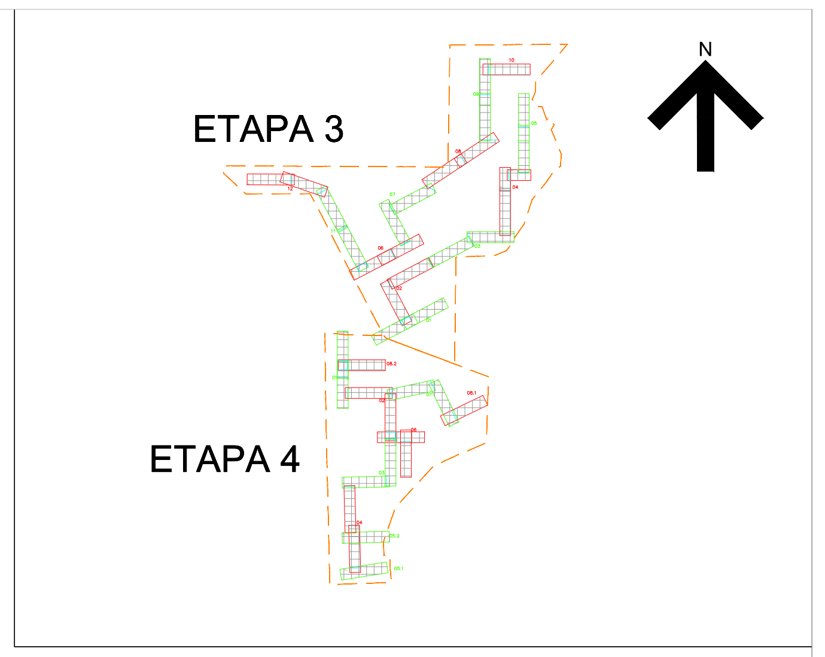
ETAPA 3
ETAPA 4
N

MAPA CHAVE

LEGENDA:

PLANTA:

- Canal Adutor
- Curvas de Nível Mestra
- Curvas de Nível Intermediárias
- Cursos d'Água
- Estradas
- Estrutura de Controle
- Valeta de Proteção de Corte e de Aterro
- Sarjeta Triangular de Corte
- Dissipador de Energia
- Bueiro Simples Tubular de Concreto
- Boca Simples
- Bacia de Captação

PERFIL:

- Terreno Natural
- Topo da Berma
- Nível D'água Dinâmico
- Nível D'água Estático
- Fundo do Canal
- Estrutura de Controle

NOTAS:

01 - MEDIDAS EM METROS, EXETO INDICAÇÃO CONTRÁRIA;
02 - SISTEMA DE COORDENADAS: DATUM SIRGAS 2000, UTM-23S;
03 - TERRENO OBTIDO DO LEVANTAMENTO TOPOGRÁFICO;

-	-	-	-	-	-	-
-	-	-	-	-	-	-
-	-	-	-	-	-	-
-	-	-	-	-	-	-
00	21/11/25	EMISSÃO INICIAL	JOP	AHL	EDK	-
Revisão	Data	Descrição	Elab.	Verif.	Aprov.	Aut.

FUNDO DE DESENVOLVIMENTO DA INFRAESTRUTURA
REGIONAL SUSTENTÁVEL - FDIRS

ESTRUTURAÇÃO DE PROJETO DE CONCESSÃO DO
PERÍMETRO IRRIGADO DO JAÍBA (ETAPAS 3 E 4)

ANTEPROJETO

SISTEMA ADUTOR
PLANTA E PERFIL - ETAPA 4
FOLHA 06

Finalidade de Emissão	1 Para Informação	2 Para Comentários	3 Para Aprovação	4 Para Execução	5 Como Construído	6 Para Utilização	7 Para Providências

Moysés & Pires Sociedade de advogados
ENGECORPS GrupoTYPSA
A&M
Plena Consultoria e Projetos

Data: 21/11/25
Escala: 1:500 / 1:500 (H:V)
Elaboração:
Verificação:
Aprovação - -
Autorização - -
Referência:
Revisão: 00
Desenho nº J4-DS-HI-005